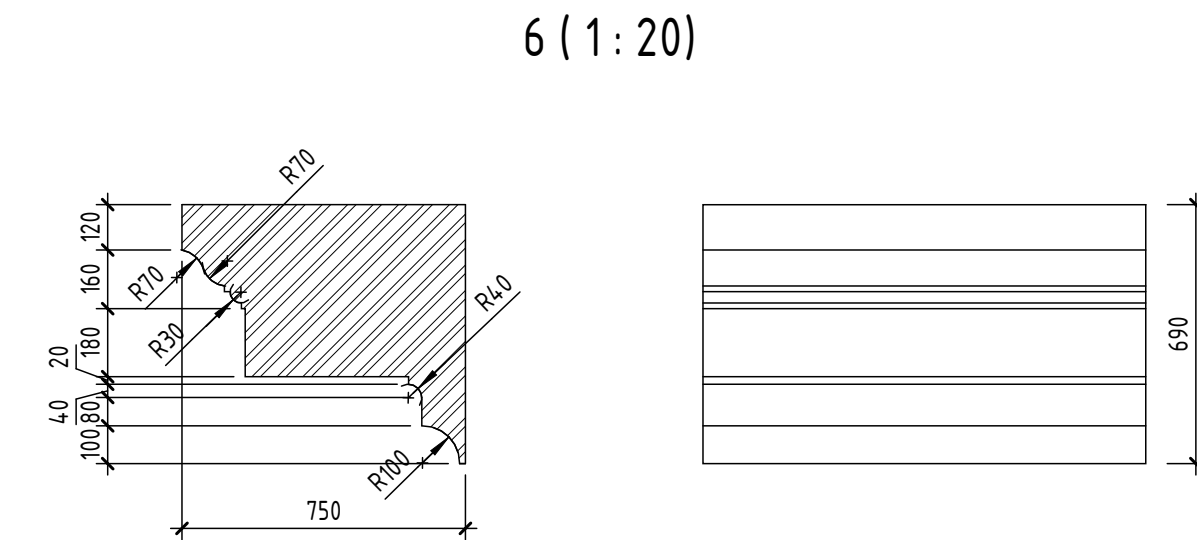
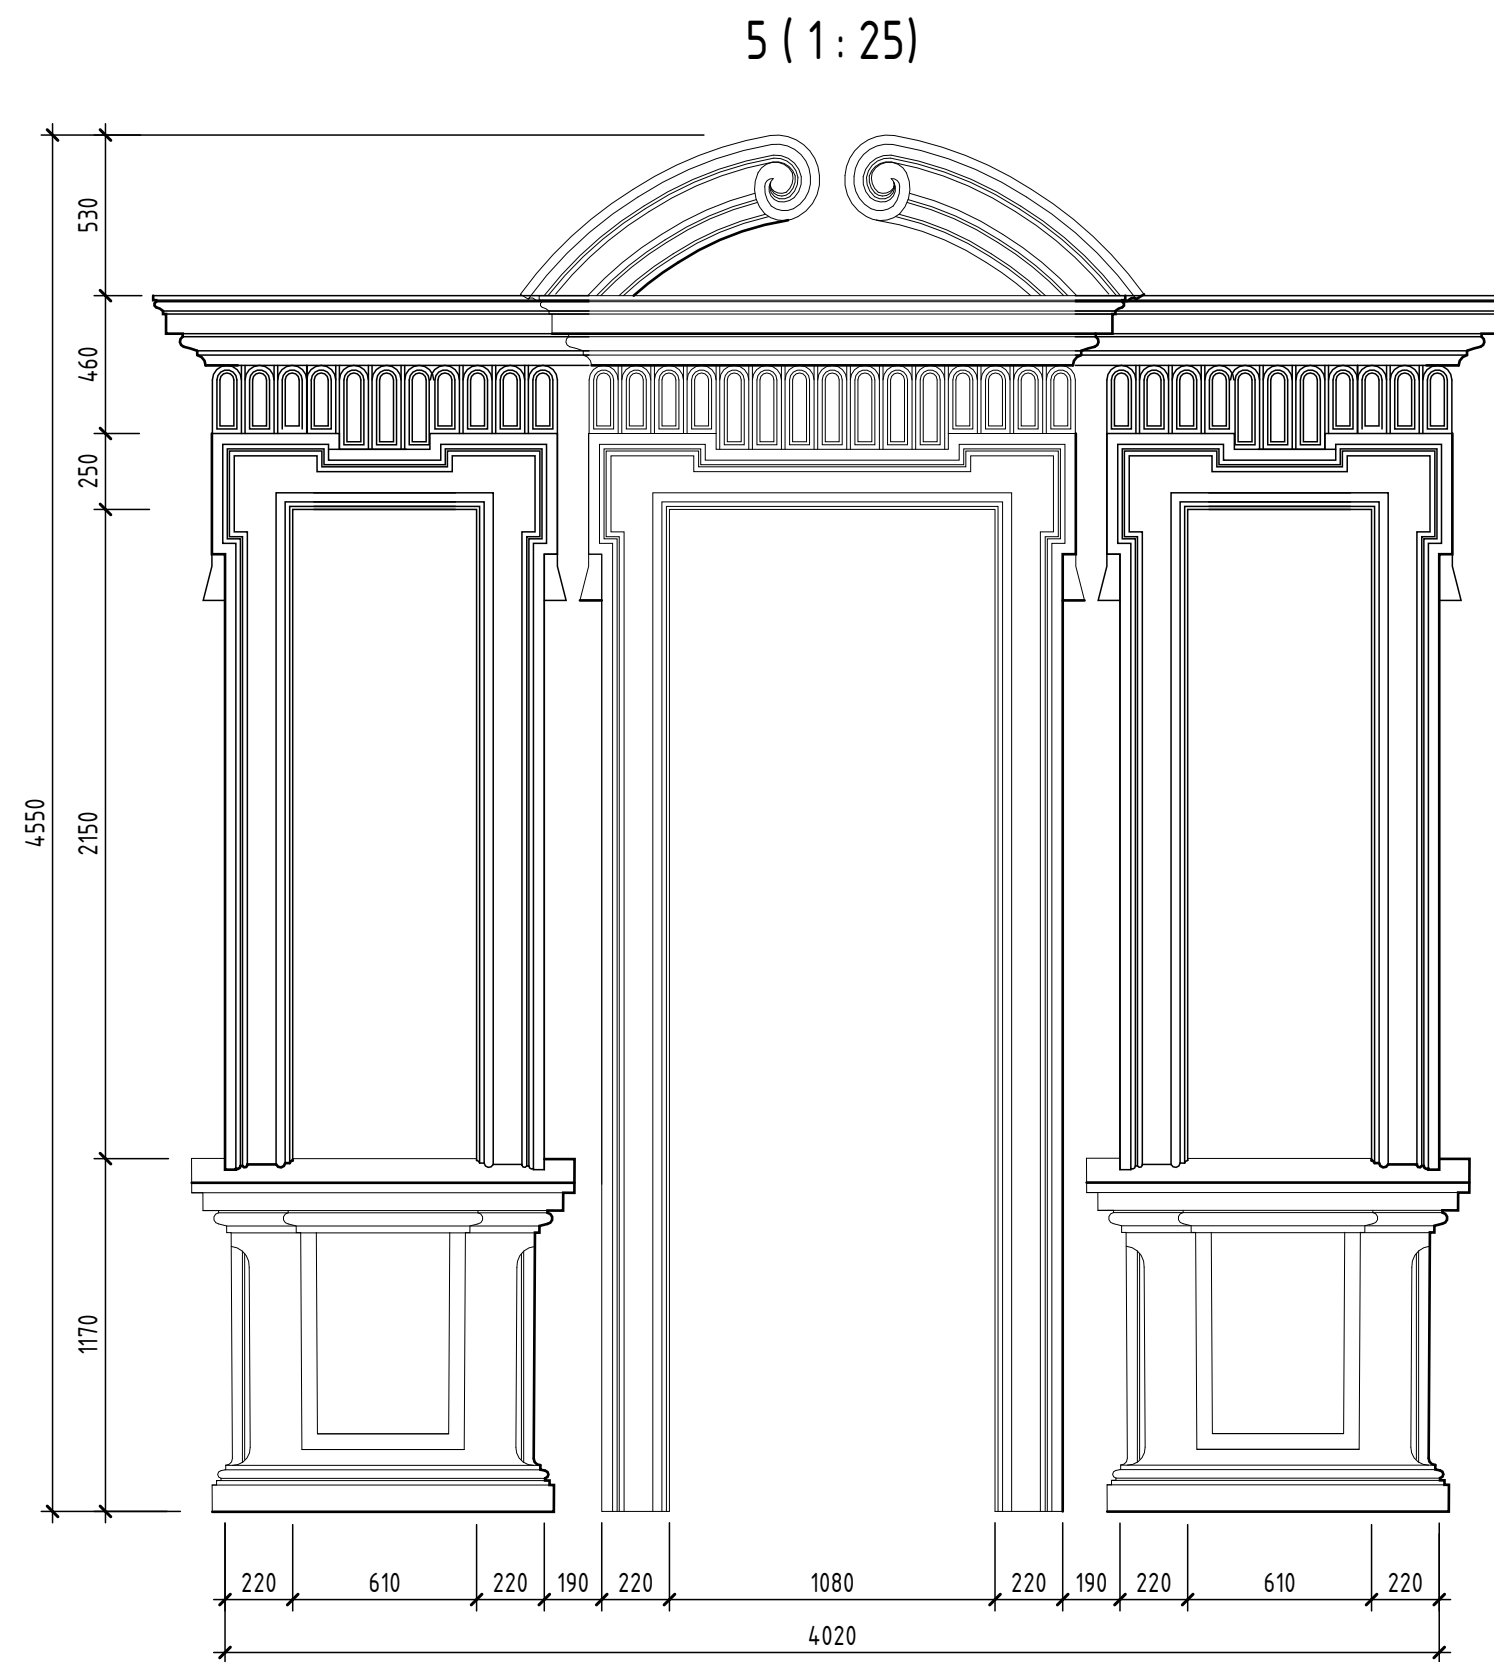


[illegible]

						006/01/0048-20 – AP			
						Капитальный ремонт здания ФГБУ РФБ по адресу: г. Москва, ул Воздвиженка 1			
Изм.	Кол.чл.	Лист	№ док.	Подп.	Дата	Корпус К.	Стандарт	Лист	Листов
							РД	30	110
ГИП		Григорьев К.С.				Фасад 1 (24-1) Монтаж.	 ИНСТИТУТ ПРОЕКТИРОВАНИЯ И СТРОИТЕЛЬСТВА		
ГАП		Щетинин А.В.							
Разработал		Щетинин А.В.							
Н. контр.		Рожков А. Ф.							