
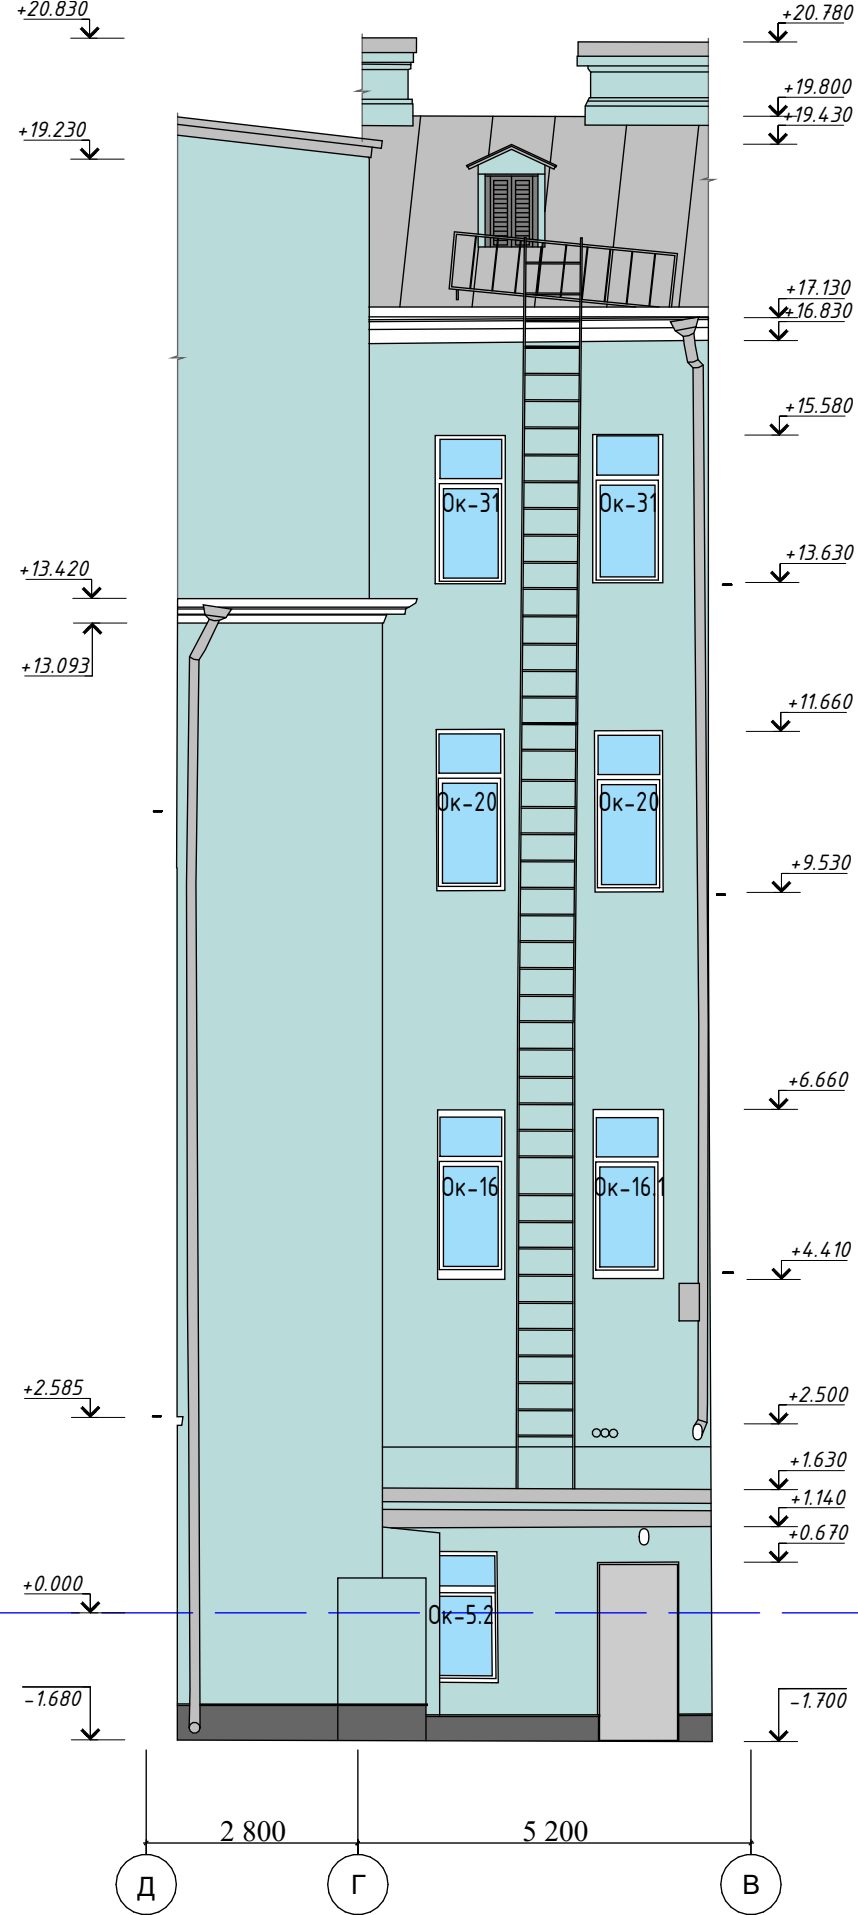


Фасад 8 (В-И) после ремонта. (1 : 100)

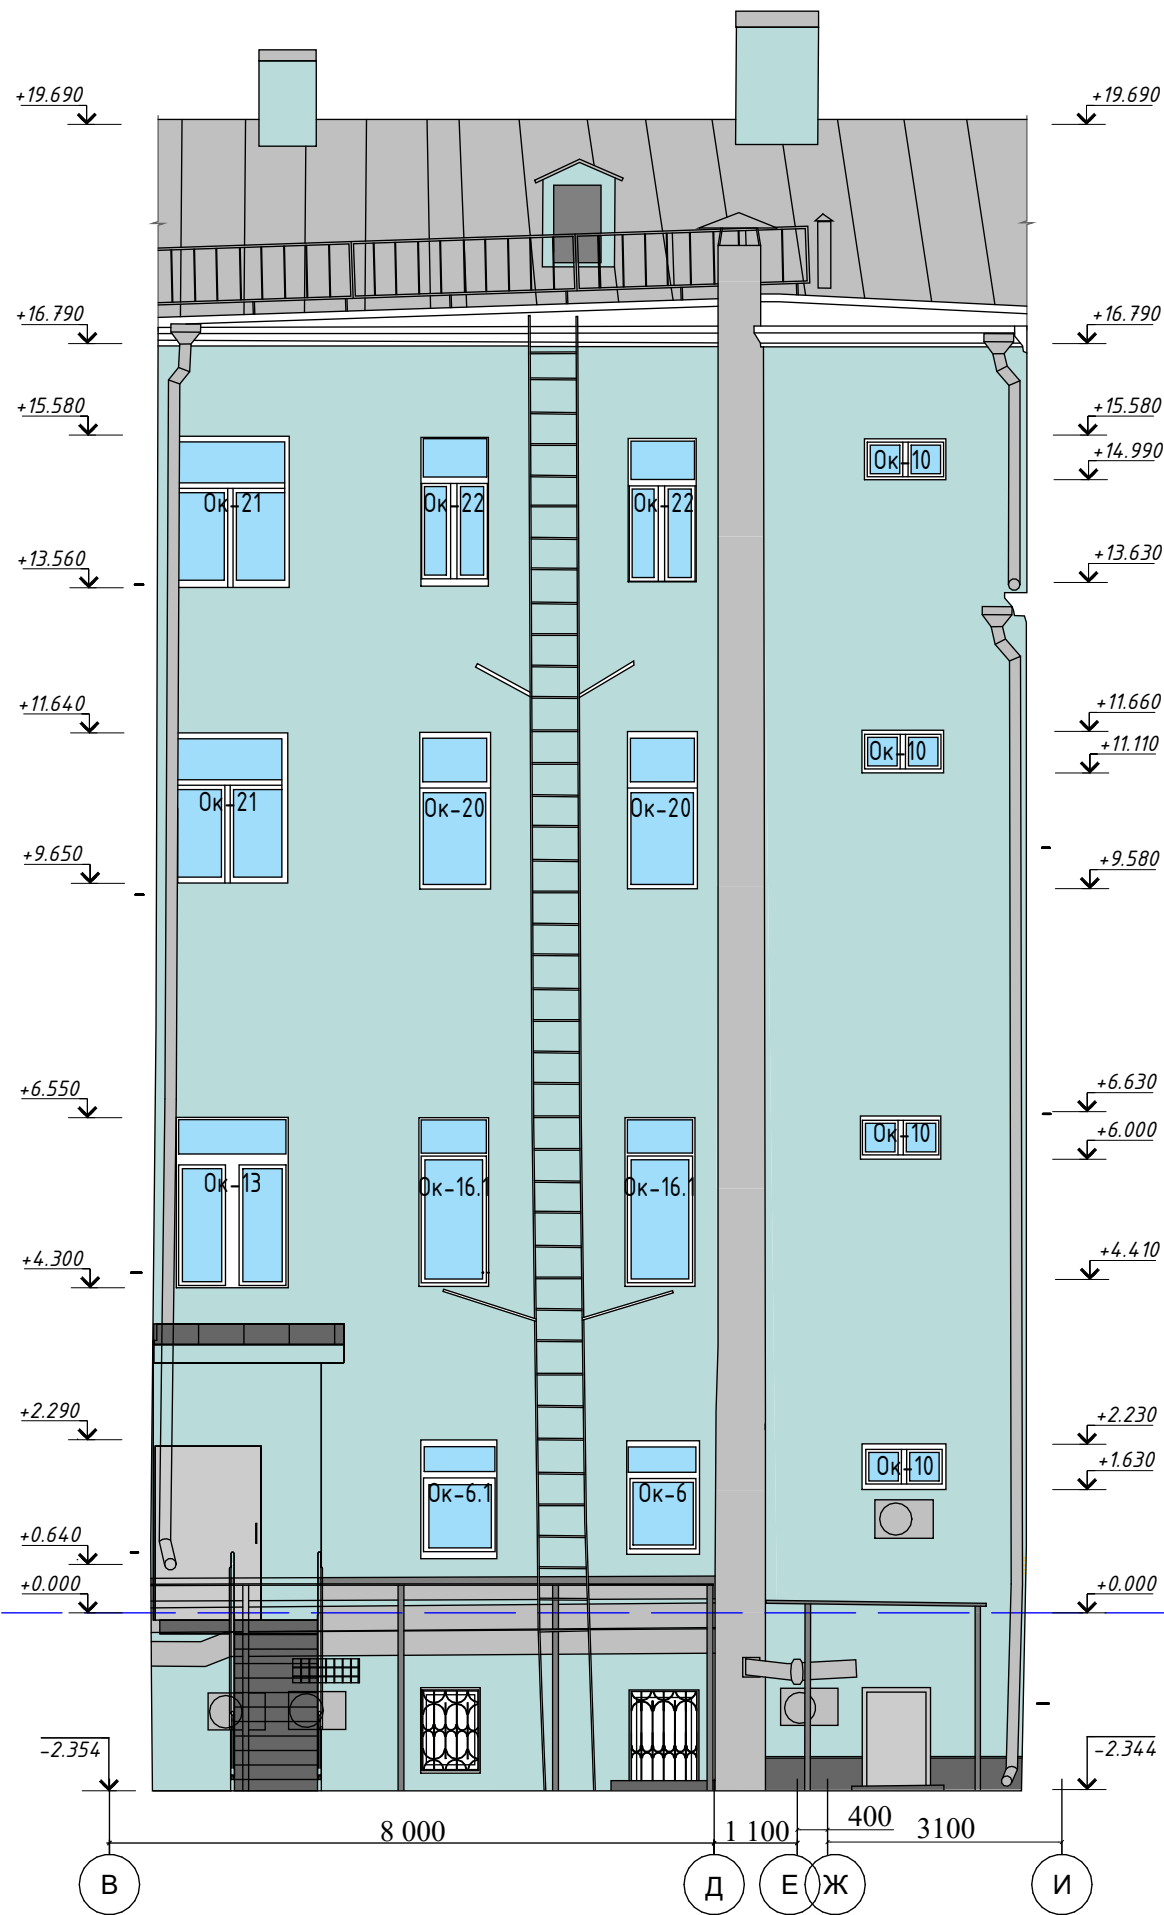

- УСЛОВНЫЕ
ОБОЗНАЧЕНИЯ**
- серый
 - гранит
 - лепнина (RAL 9010)
 - основной цвет фасада (RAL 6027)
 - цвет кровли (оцинкованный металл)

Ведомость отделки Фасада 8 (В-И)				
Наименование фасада	Площадь стен	Площадь отделки и покраски силиконовой краской RAL9010	Площадь отделки и покраски силиконовой краской RAL6027	Площадь полного восстановления утраченной отделки
Фасад 8 (В-И)	259,55	112,90	184,28	103,82
Общий итог	259,55	112,90	184,28	103,82

Ведомость отделки Фасада 9 (Д-В)				
Наименование фасада	Площадь стен	Площадь отделки и покраски силиконовой краской RAL9010	Площадь отделки и покраски RAL6027	Площадь полного восстановления утраченной отделки
Фасад 9 (Д-В)	166,40	82,37	111,49	66,56
Общий итог	166,40	82,37	111,49	66,56

						006/01/0048-20 - АР			
						Капитальный ремонт здания ФГБУ РГБ по адресу: г. Москва, ул Воздвиженка 1			
Изм.	Кол.уч.	Лист	№ док.	Подп.	Дата	Корпус К.	Стадия	Лист	Листов
ГИП		Григорьев К.И.					РД	41	110
ГАП		Щетинин А.В.							
Разработал		Щетинин А.В.							
Н. контр.		Рожков А.Ф.				Фасады 8,9 (В-И, Д-В) после ремонта.		 ИНСТИТУТ ПРОЕКТИРОВАНИЯ И СТРОИТЕЛЬСТВА	