



Фасад Северный (1 : 100)

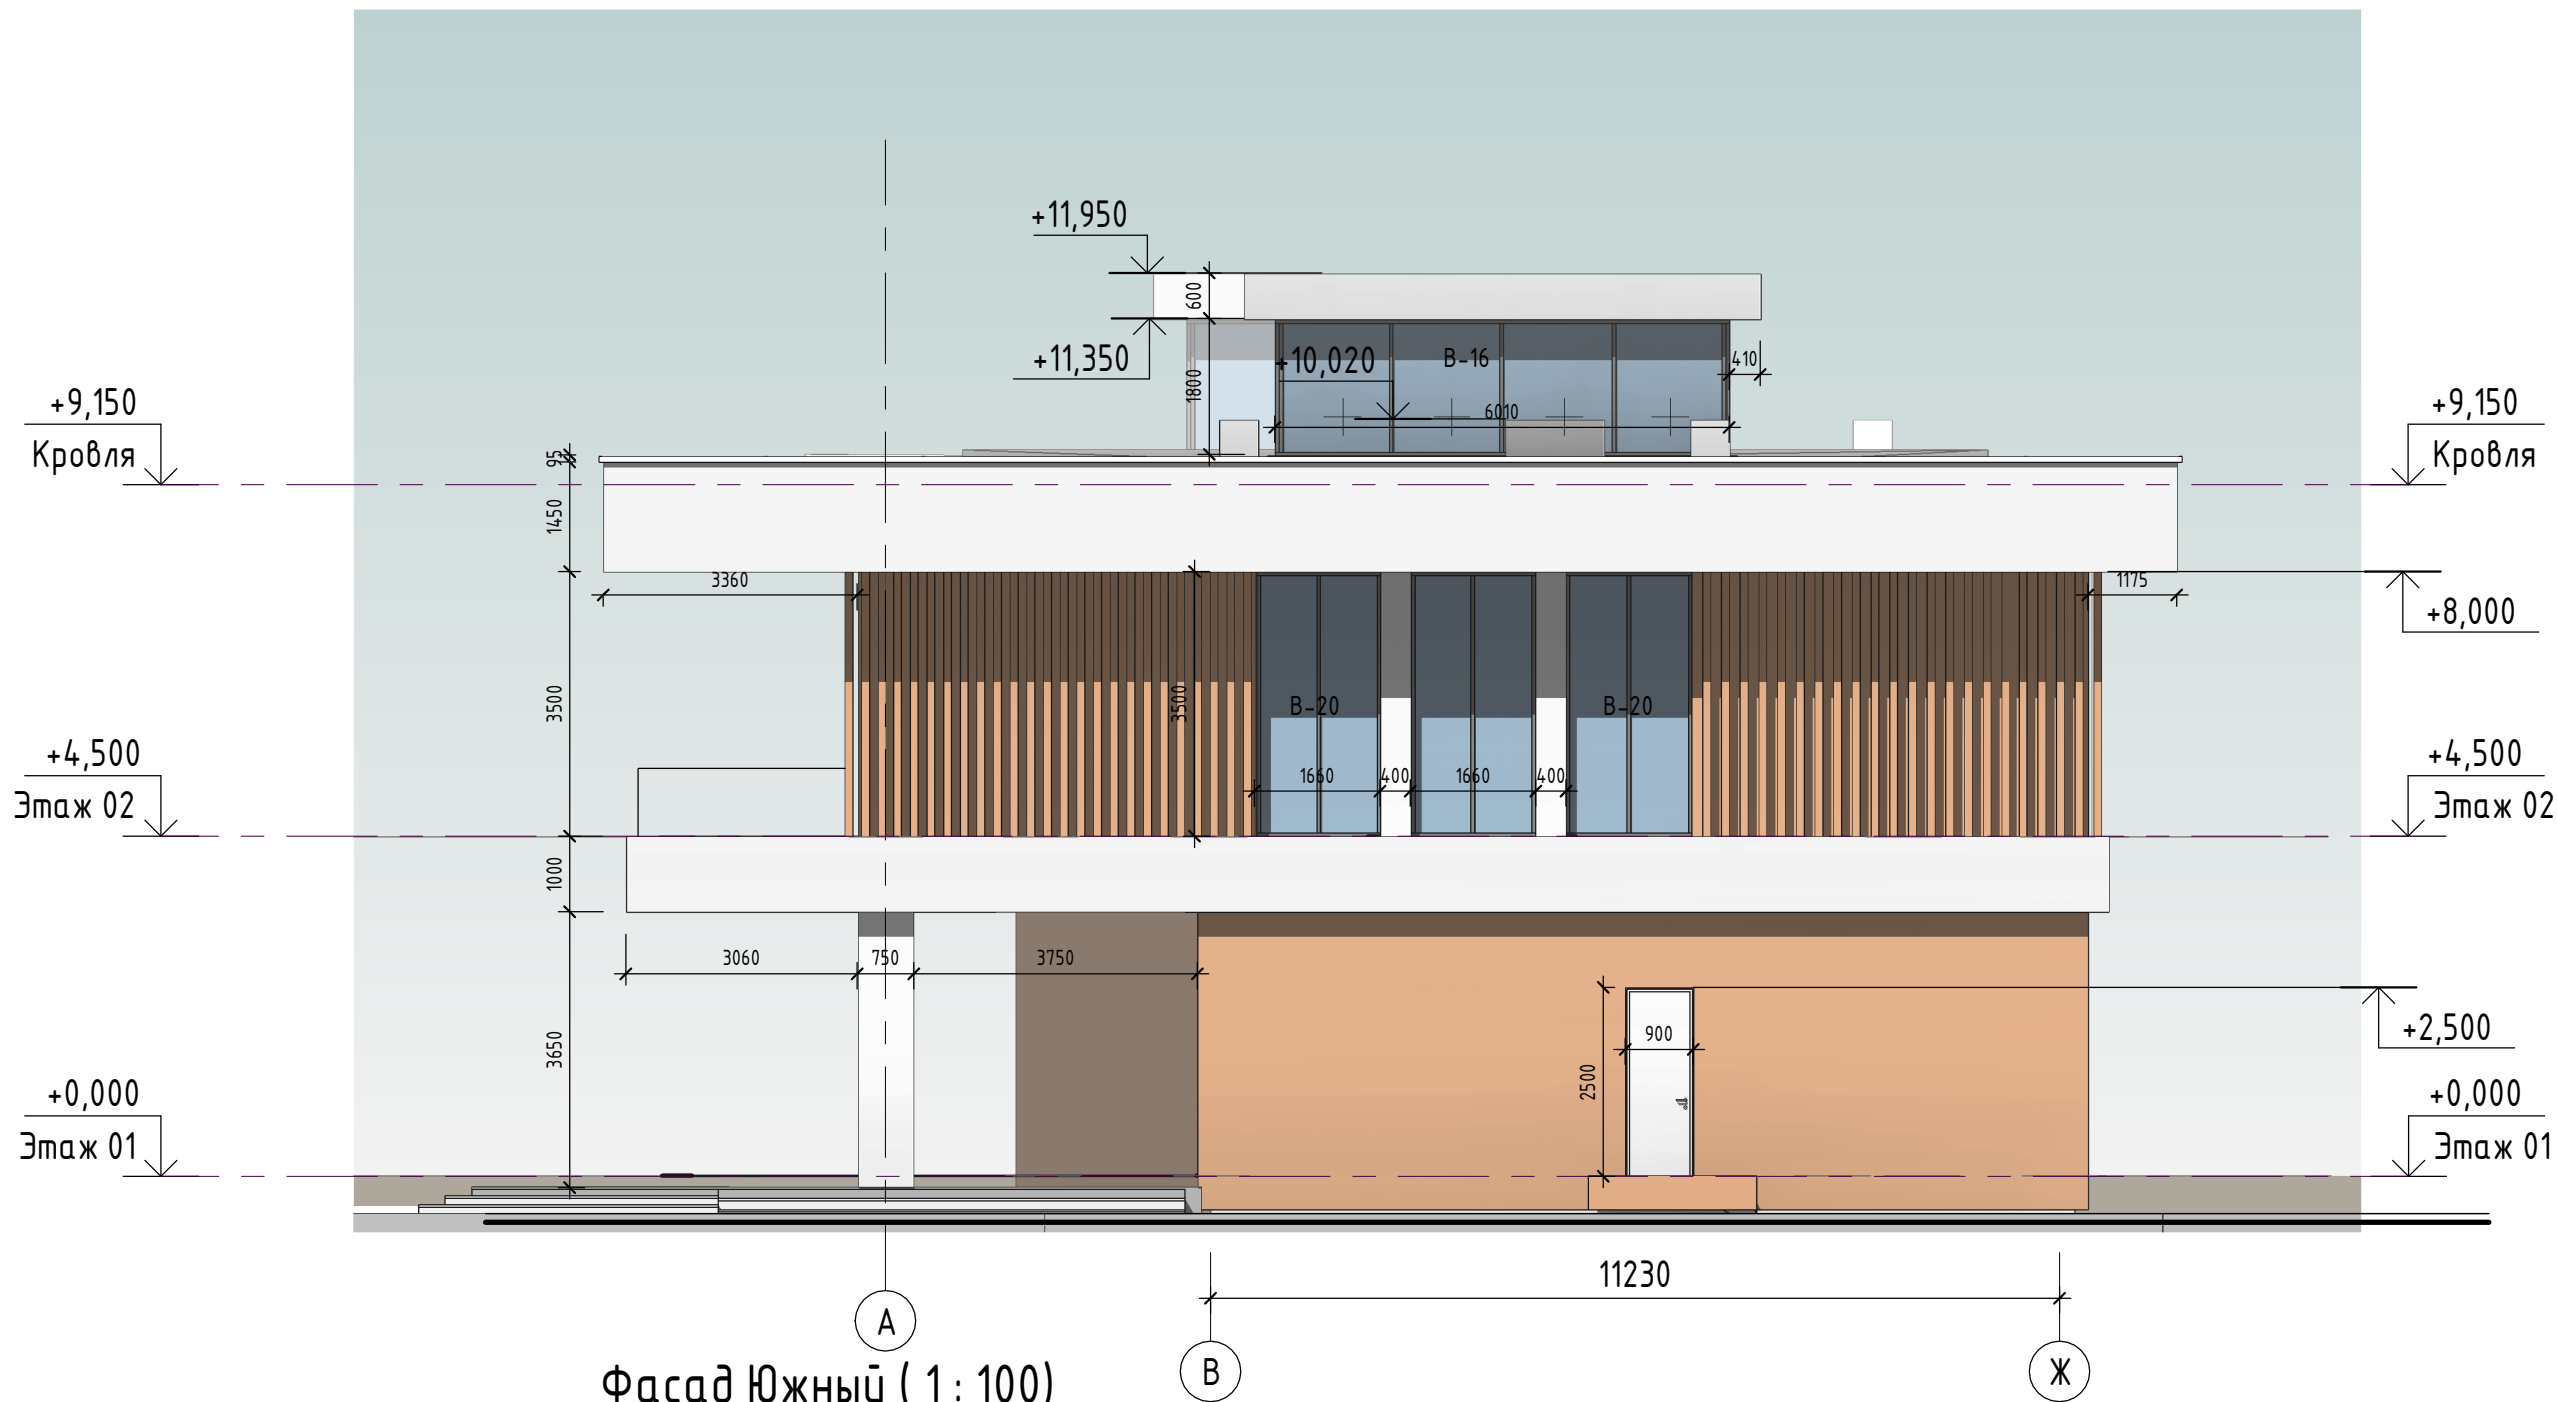

Декоративные решетки из обработанного дерева, брус 100х100 с шагом 200мм

Фасад Восточный.....24 м2
Фасад Западный.....12 м2
Фасад Южный.....59 м2
Фасад Северный.....38 м2

Фасад Южный (1 : 100)

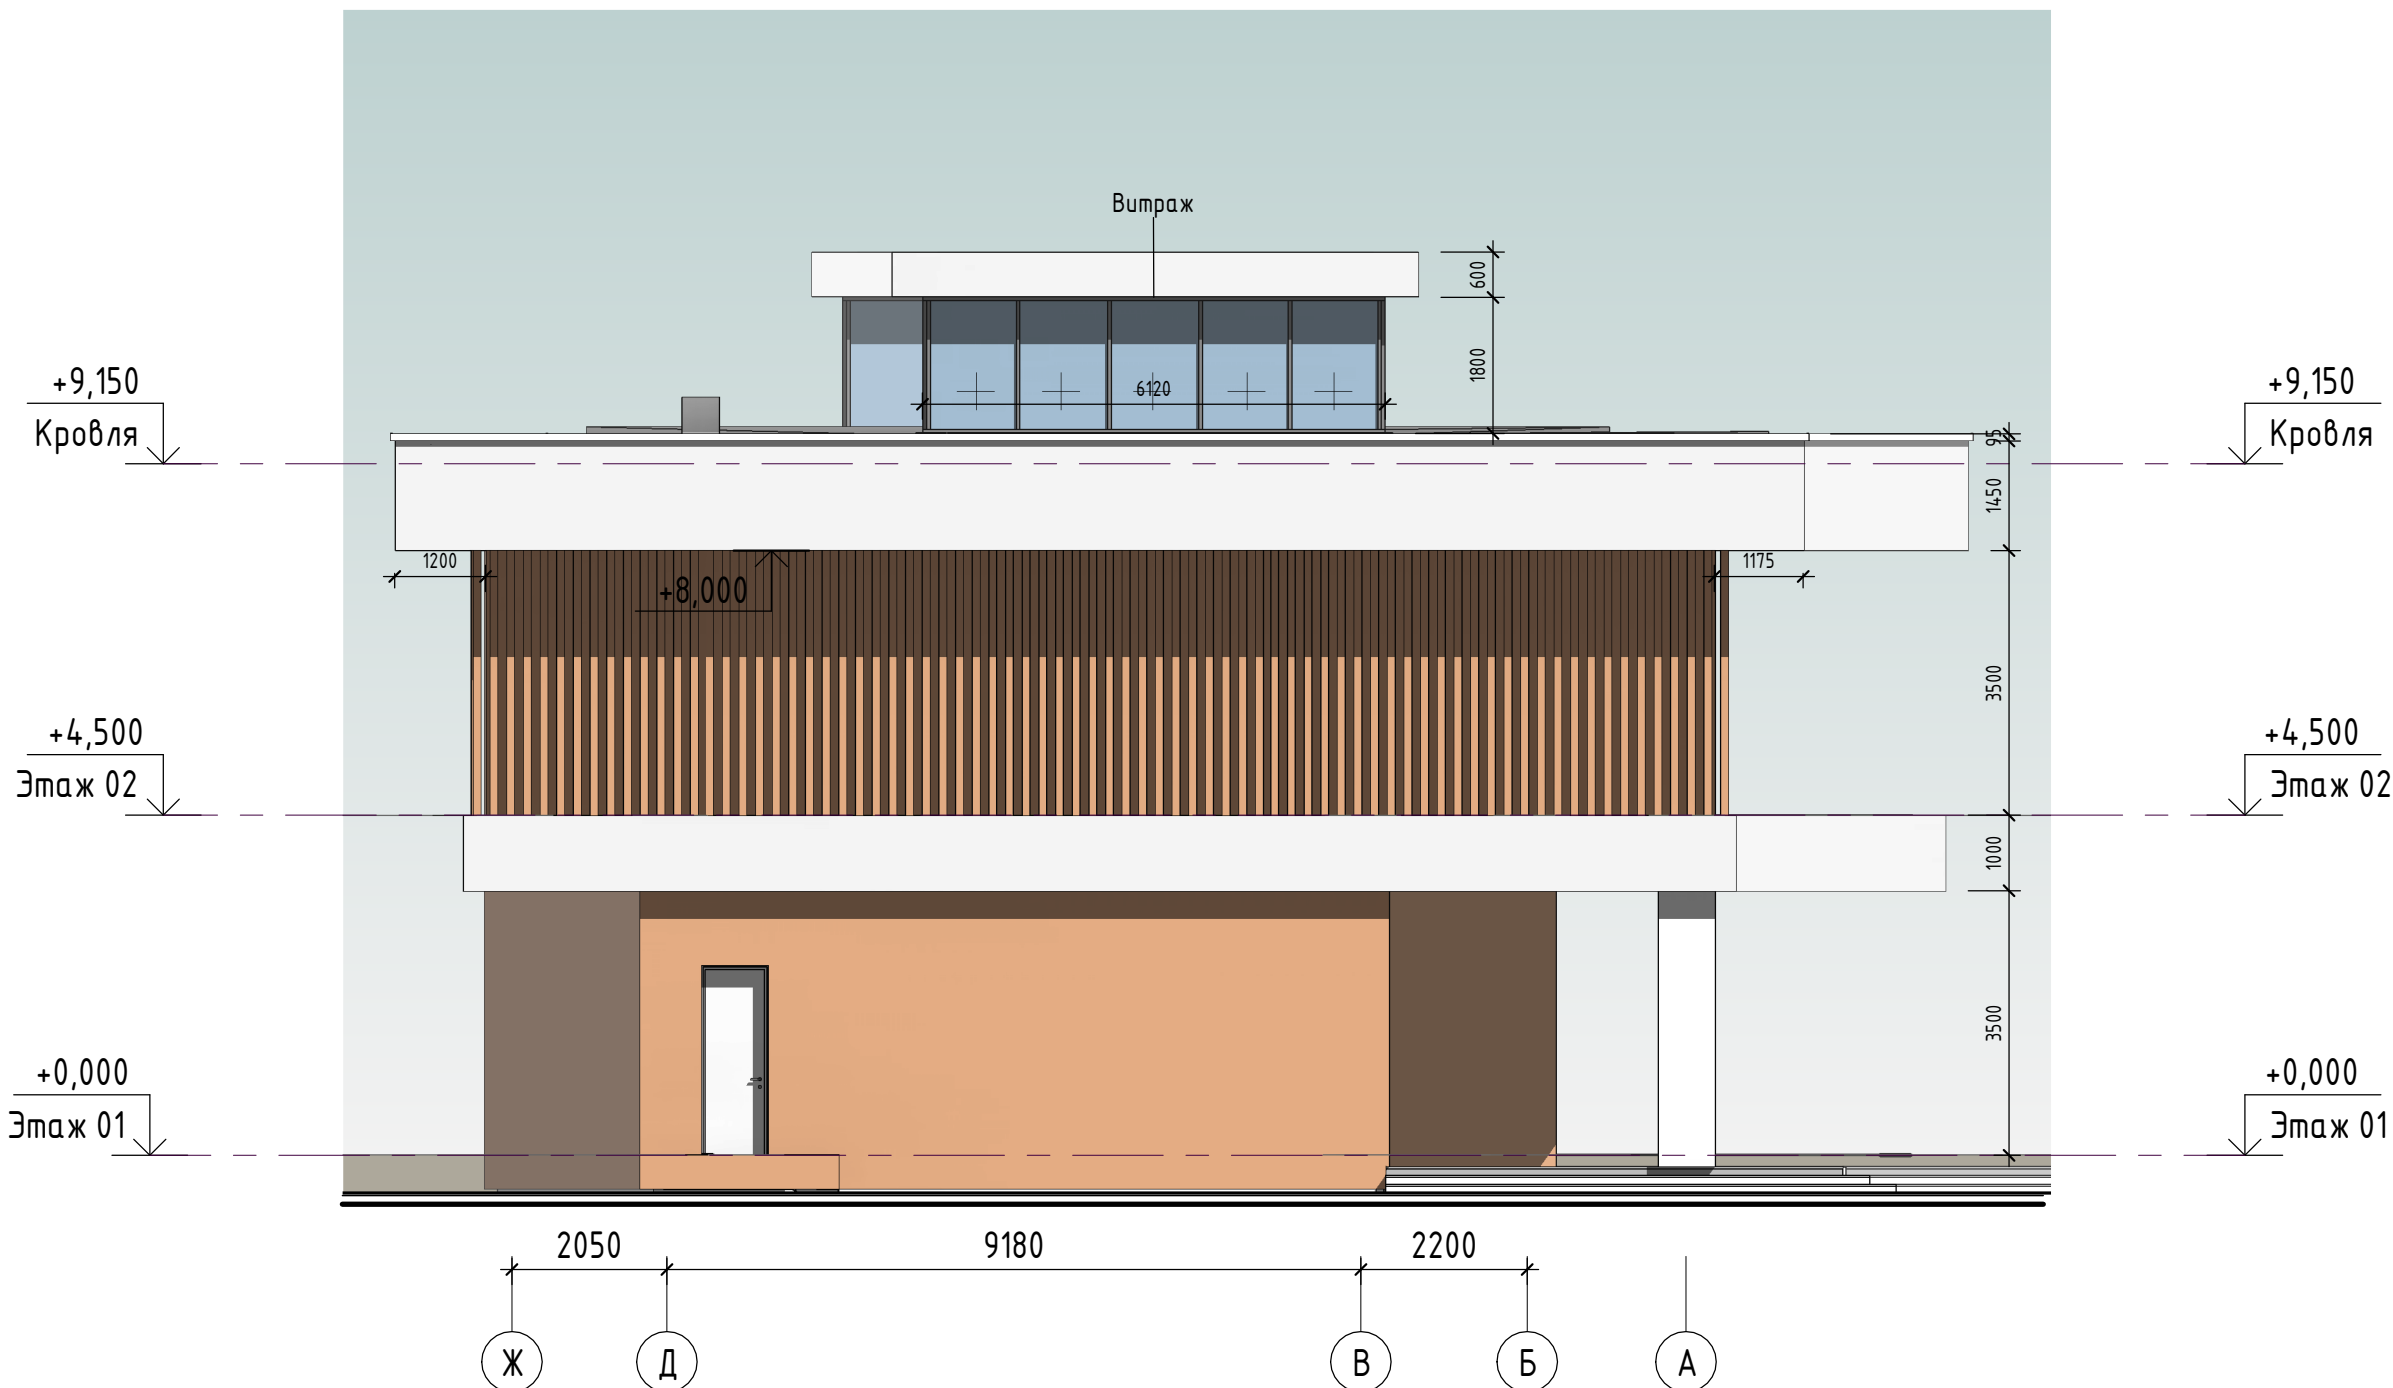

Ведомость отделки фасадов				
Тон	Наименование	Тип стены	Длина мм	Площадь м2
Свет				
	Керамогранит MATERICA BIANCO	См175Свет	18834	49,58
	Керамогранит MATERICA BIANCO	См615Свет	83470	149,29
			102304	198,87
Темный				
	Керамогранит MATERICA TORTORA	СмБКС75Темн	2400	10,32
	Керамогранит MATERICA TORTORA	См300КТемн	7413	3,16
	Керамогранит MATERICA TORTORA	См175Темн	70803	21,24
	Керамогранит MATERICA TORTORA	См615Темн	159165	562,28
			239780	597,00
			342084	795,87

Примечание: Данный лист смотреть с листами 18, 20, 21

						05-05/18 - АРРП			
						Московская область, городской округ Красногорск, коттеджный поселок Кристалл Истра			
Изм.	Кол.уч.	Лист	№ док.	Подп.	Дата	Индивидуальный 2х этажный жилой дом.	Стадия	Лист	Листов
Директор	Костин С.						РП	24.	18
ГАП	Щетинин А.								
ГИП	Тепляков К.								
Архитектор	Коновалов В.					Фасады Южный и Северный			
Проверил	Тепляков К.								