



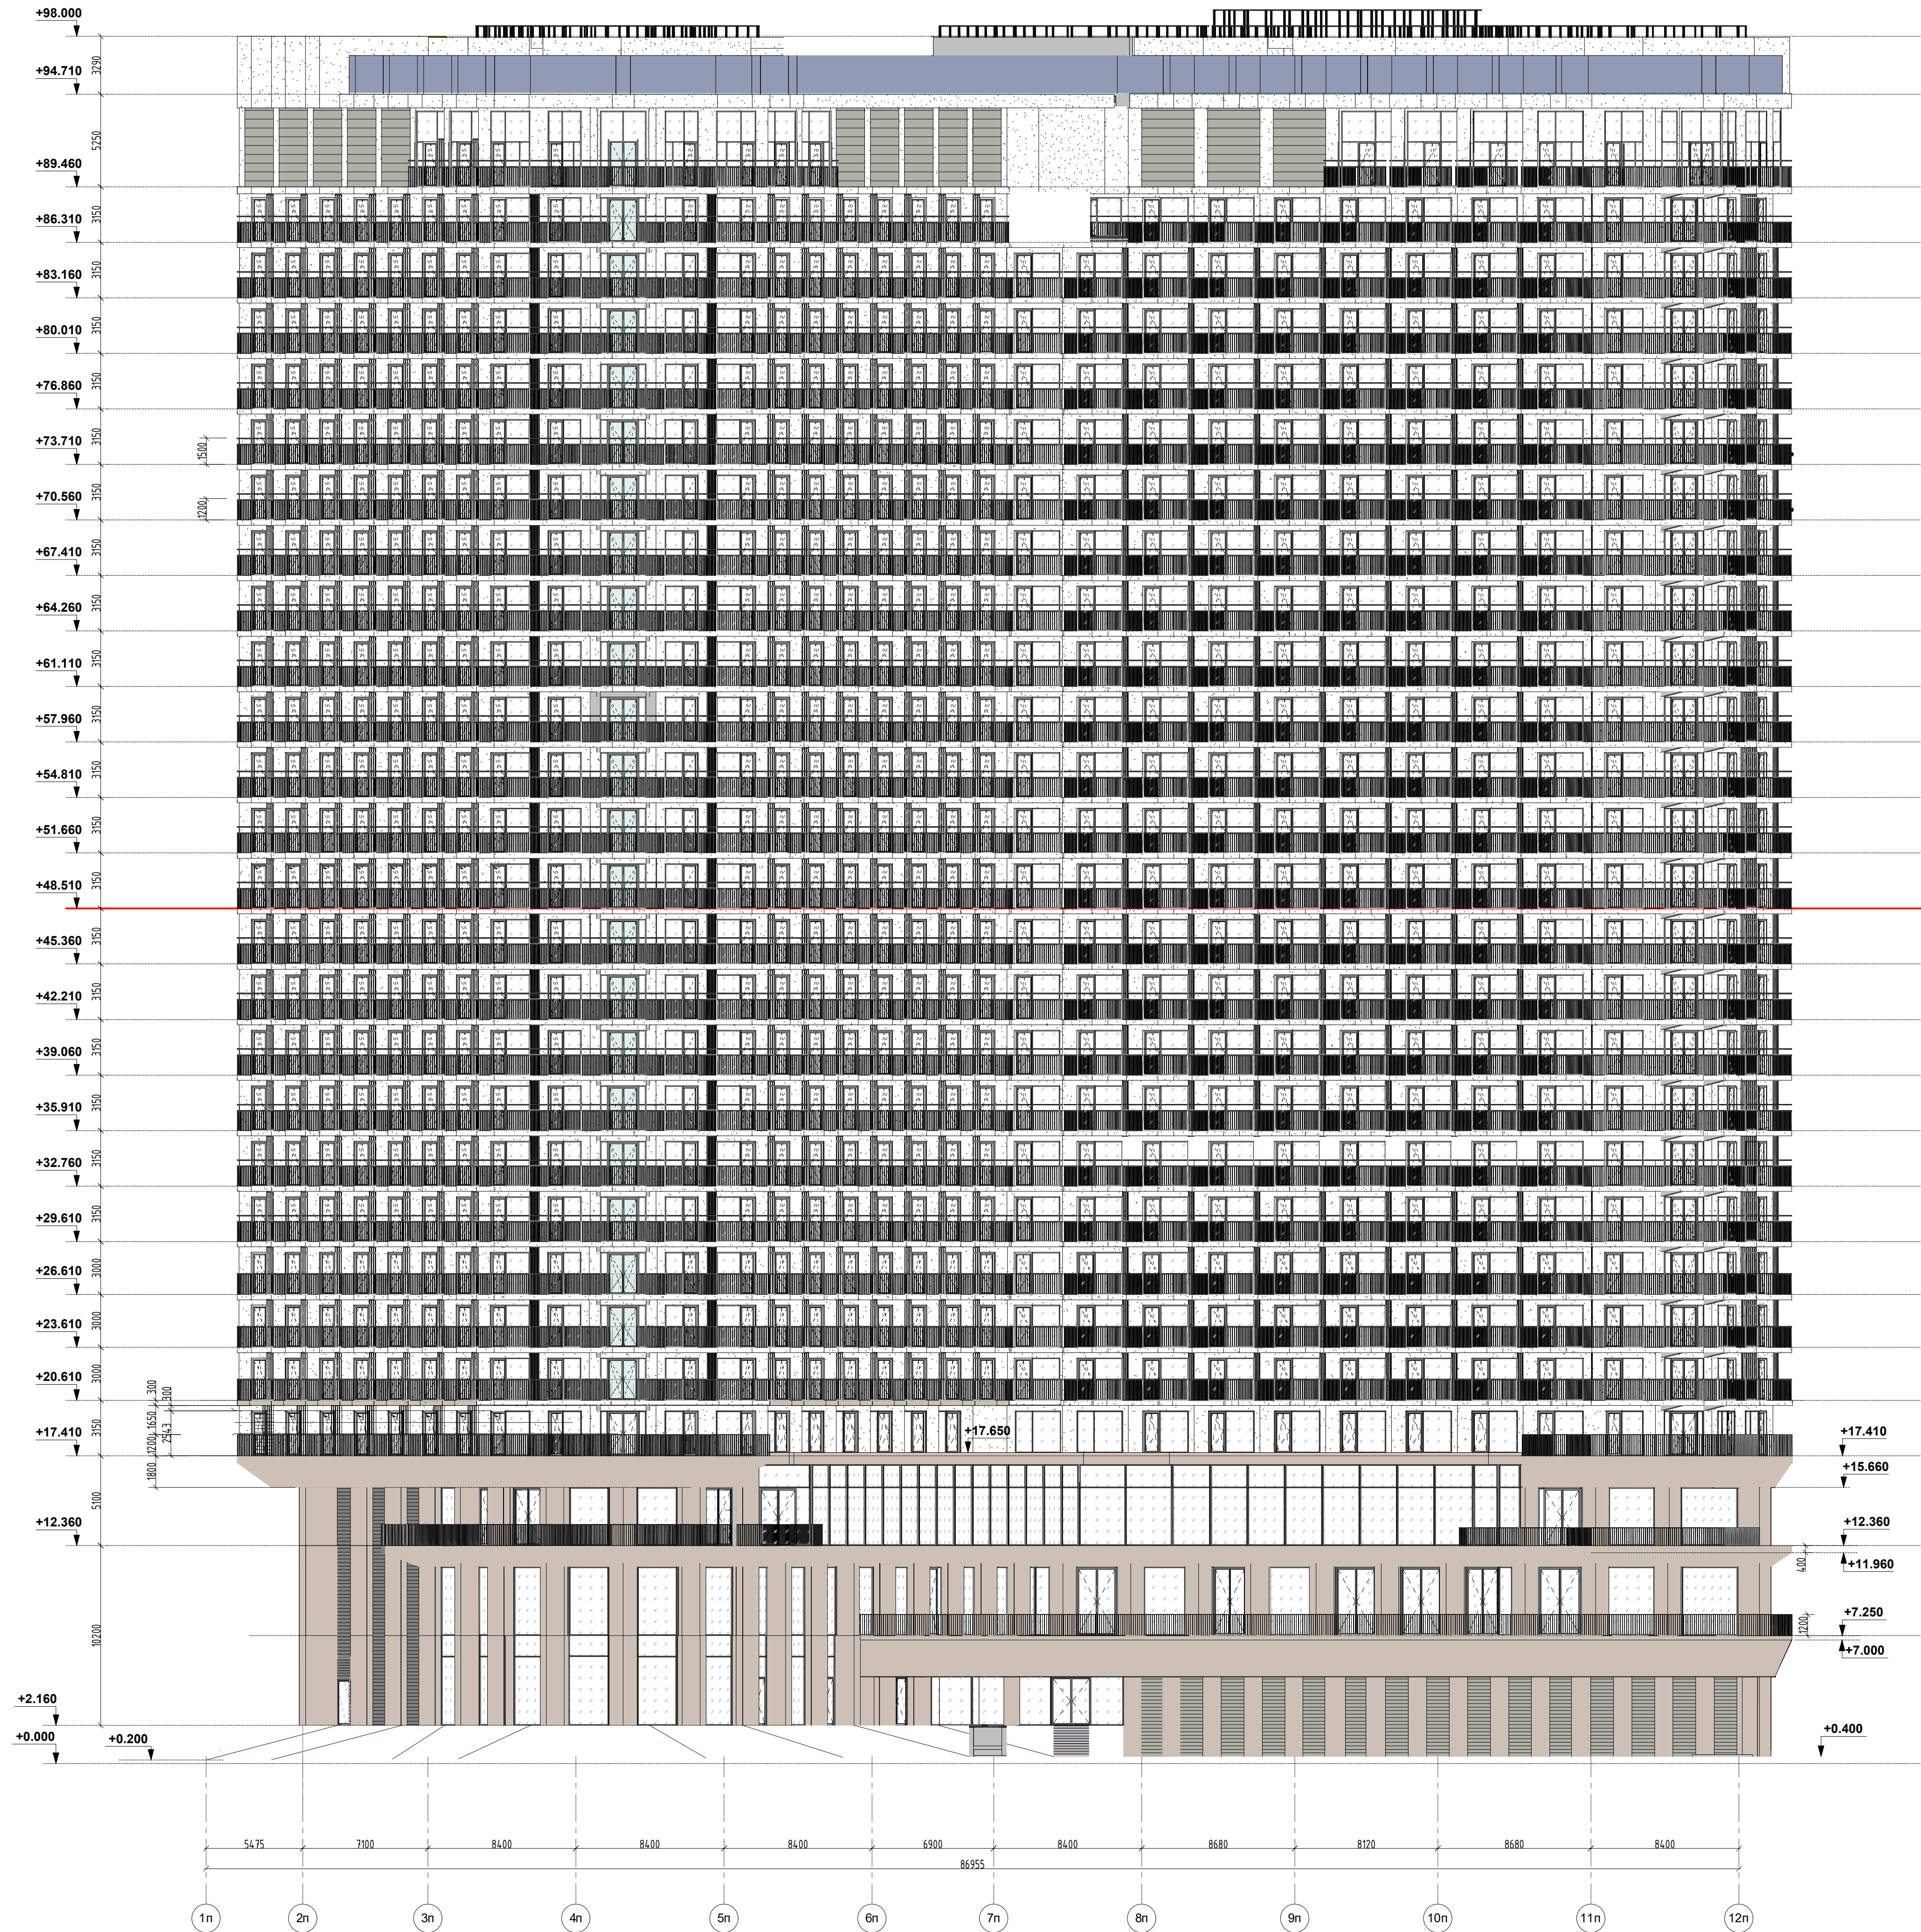

Условные обозначения:

- Декоративная фасадная "камешковая" штукатурка по технологии CERESIT WM, окраска силиконовой фасадной краской (Ral 0908505) по согласованному образцу. (1.1 - стены 4-28 этаж; 1.2 - потолки балконов 5-28 этажей)
- Панели из высокопрочного архитектурного бетона Армбетоника RAL с индексом EG-45 П SCH1687 на подсистеме HiTi" max. высота вертикального заборота 5100 мм (или аналог) по согласованному образцу на фасадной системе HiTi VFH ArchBeton (или аналог) в системе навесного фасада на подсистеме со скрытым креплением
- Стеклалит RAL по согласованию с Заказчиком в составе стеклопакета в системе витражного остекления
- Прозрачное стекло в составе стоечно-ригельного остекления
- Рамы стоечно-ригельных стеклопрозрачных конструкций (Стилобат, 4-27 этажи) Ral 1035
- Ограждение металлическое балконов и отливов торцов балкона, окраска AkzoNobel код: YW358F, цвет блеск: GRIS2500 муар, описание: YW358F INTD2525 SABLE GRIS2500 FM10
- Жалюзированная декоративная фасадная безрамная вентрешетка, алюминиевый профиль ламели типа RENSON , порошковая окраска по согласованию с Заказчиком Коэффициент живого сечения решеток не ниже 0,5. По всей плоскости - стальная сетка 3х3мм , порошковая окраска в цвет ламелей , крепление по технологии подрядчика
- Жалюзированная решетка в структуре стоечно-ригельного остекления- ламелей типа RENSON , порошковая окраска по согласованию с Заказчиком Коэффициент живого сечения решеток не ниже 0,5. По всей плоскости - стальная сетка 3х3мм , порошковая окраска в цвет ламелей , крепление по технологии подрядчика по витражам
- Ограждение кровель окраска по RAL 1035 матовый, образец по согласованию Заказчика
- Ограждение стеклянное (триплекс) 28 этажа

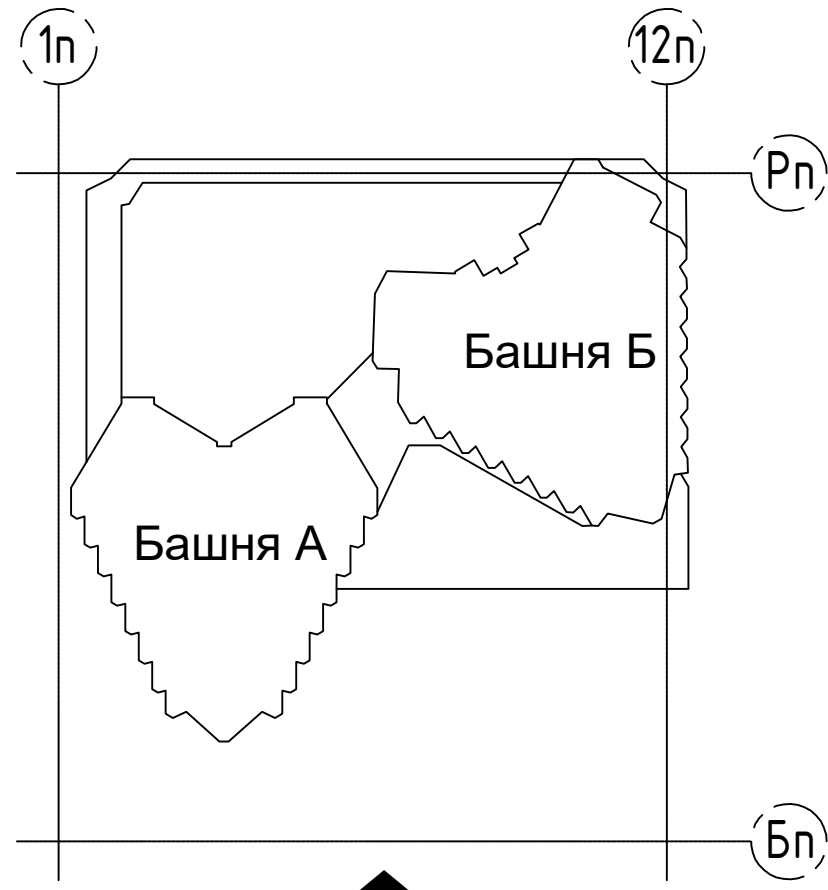

						MP-1535-01-AP			
						Развитие гостиницы «Приморская» в г. Сочи. Строительство нового корпуса гостиницы, расположенного по адресу: г. Сочи, Центральный район, ул. Соколова, д. 1. Этап 3			
6	-	Зам.	0372-26	<i>Подпись</i>	12.05.26	Архитектурные решения	Стадия	Лист	Листов
Изм.	Кол.уч.	Лист	№ док.	Подпись	Дата		П	27	34
Разраб.		Корнеев		<i>Подпись</i>	12.05.26		METROPOLIS		
Проверил		Галабузда		<i>Подпись</i>	12.05.26				
Н.контр.		Гордеев		<i>Подпись</i>	12.05.26				