
Фасад в осях 8-1

М 1 : 200

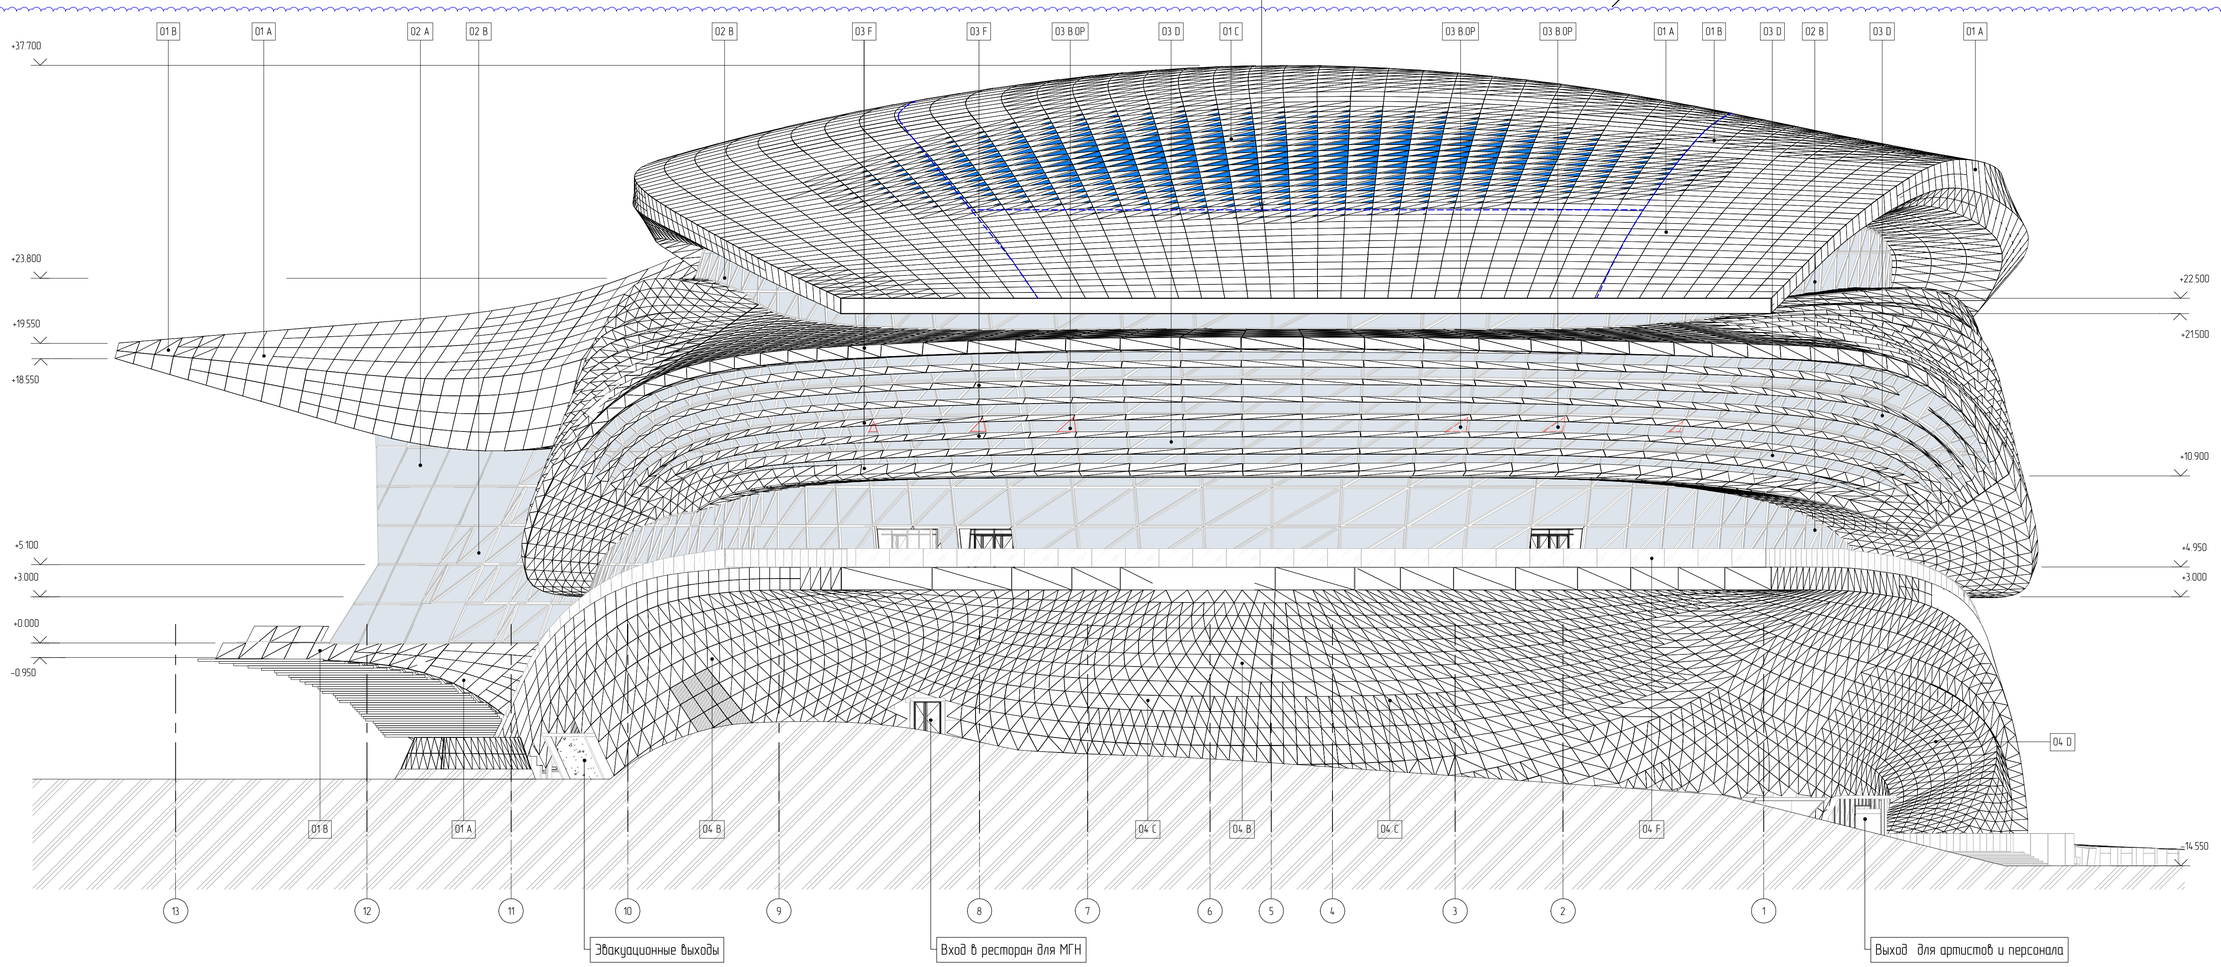


12

Ведомость отделки фасадов

Обозн.	Часть здания	Материал	Описание	Цвет	RAL	Артикул		Лист	Справочная информация
01 A	Кровля	Zanette Панель	Панель 4 ребра, белая, матовое покрытие		9016 Traffic White	Zanette GRC ZIP		S 33 S 25.2	R1B R9A F3A F7A
01 B	Кровля	Zanette Панель	Панель 3 ребра, белая, матовое покрытие		9016 Traffic White	Zanette GRC ZIP		S 33 S 25.2	R1B R9A F3A
01 C	Кровля	Фальш-фонарь	Фальш-фонарь			Индивид. изготовл.		S 33 S 25.2	R1B R9A F3A F7A
02 A	Фойе	Стеклопакет	Структурное остекление, панель 4 ребра			LartaPro HD Light Blue 52		S 34 S 35 S 25.3 S 25.4	F1A F2A F5A
02 B	Фойе	Стеклопакет	Структурное остекление, панель 3 ребра			LartaPro HD Light Blue 52		S 34 S 35 S 25.3 S 25.4	F1A F2A C6A (ii)
02 C	Фойе	Стеклопакет	Структурное остекление, панель 4 ребра с открыванием			LartaPro HD Light Blue 52		S 34 S 35 S 25.3 S 25.4	
02 D	Фойе	Стеклопакет	Структурное остекление, панель 3 ребра с открыванием			LartaPro HD Light Blue 52		S 34 S 35 S 25.3 S 25.4	
03 A	Скоба	Стеклопакет	Панель 3 ребра			LartaPro HD Light Blue 52		S 35 S 39 S 25.5	C6A (i) C5A C6A (ii)
03 B	Скоба	Стеклопакет	Панель 3 ребра с открыванием			LartaPro HD Light Blue 52		S 35 S 39 S 25.5	
03 C	Скоба	Стеклопакет	Остекление офисов, с открыванием			LartaPro HD Light Blue 52		S 35 S 39 S 25.5	
03 D	Скоба	Стемалит	Непрозрачная панель 3 ребра			LartaPro HD Light Blue 52		S 35 S 39 S 25.5	
03 E	Скоба	Zanette панель	Панель 4 ребра, белая, матовое покрытие		9016 Traffic White	Zanette GRC ZIP		S 35 S 39 S 25.5	C5A
03 F	Скоба	Zanette панель	Панель 3 ребра, белая, матовое покрытие		9016 Traffic White	Zanette GRC ZIP		S 35 S 39 S 25.5	
03 G	Скоба	Армированное стекло	Армированное стекло с покрытием black-out			LartaPro HD Light Blue 52 GP-3		S 35 S 39 S 25.5	
04 A	Цоколь	Zanette панель	Панель 4 ребра, белая, матовое покрытие		9016 Traffic White	Zanette GRC ZIP		S 40	P5B F4A
04 B	Цоколь	Zanette панель	Панель 3 ребра, белая, матовое покрытие		9016 Traffic White	Zanette GRC ZIP		S 40	P5B F4A
04 C	Цоколь	Zanette панель	50% перфорации, белый, матовое покрытие		9016 Traffic White	Zanette GRC ZIP		S 40	
04 D	Цоколь	Стеклопакет Перфорир. металл	51% перфорации, алюминий		9016 Traffic White	LartaPro HD Light Blue 52 R6T8		S 40	P6B
04 E	Цоколь	Мощение из натурального камня	Пешеходная зона			LartaPro HD Light Blue 52		S 40	
04 F	Цоколь	Стекло	Ограждение			Zanette GRC ZIP		S 40	
05 A	Вход	Zanette панель	Козырек, белый, матовое покрытие		9016 Traffic White	Zanette GRC ZIP		S 34 S 25.6	E4B E3B E5B
05 B	Вход	Стеклопакет	Остекление входного тамбура			LartaPro HD Light Blue 52		S 34 S 25.6	
05 C	Вход	Стеклопакет	Остекление, панель 4 ребра с открыванием			LartaPro HD Light Blue 52		S 34 S 25.6	
05 D	Вход	Металл	Облицовочная алюминиевая панель		9016 Traffic White	Color to Match Fibre C		S 34 S 25.6	
08 A	Хладоцентр	Zanette панель	Панель 4 ребра, белая, матовое покрытие		9016 Traffic White	Zanette GRC ZIP		S 40	
08 B	Хладоцентр	Zanette панель	Панель 3 ребра, белая, матовое покрытие		9016 Traffic White	Zanette GRC ZIP		S 40	

Объем материалов см. ведомость на листе 29.1»

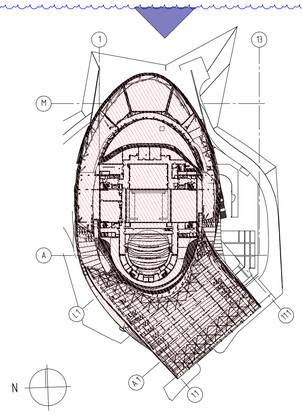

±0.000= 30.000

0.000=30.00

DESIGN ARCHITECT
COOPHIMMELB(L)AU
Wolf D. Prix & Partner ZT GmbH
TEL +43 (1) 546 60-0
FAX +43 (1) 546 60-600
SPENGERGASSE 37 A – 1050 WIEN
CONSULTANTS

Изм.	Кол.уч.	Лист	№ докум.	Подпись	Дата
5	-	Зам	0919-25		02.06.25
4	-	Зам	0864-25		26.05.25
7	-	Зам	1234-25		28.07.25
6	2	Зам	1006-25		16.06.25
Разраб.		Семенов В			16.06.25
Проверил		Иванов			16.06.25
ГАП		Павлов			16.06.25
ГИП		Головин			16.06.25
Н.контр.		Пронин			16.06.25
Нач. отд.		Пронин			16.06.25

МР-1468П-00- АР1

«Театр оперы и балета»
по адресу Российская Федерация, г. Севастополь

Стадия	Лист	Листов
П	28	

Подраздел 1. Архитектурные решения.

Фасад в осях 8-1

Engineering and Research
METROPOLIS

Формат А1

Согласовано

Инв.№ подл. | Подп. и дата | Взам. инв.№