

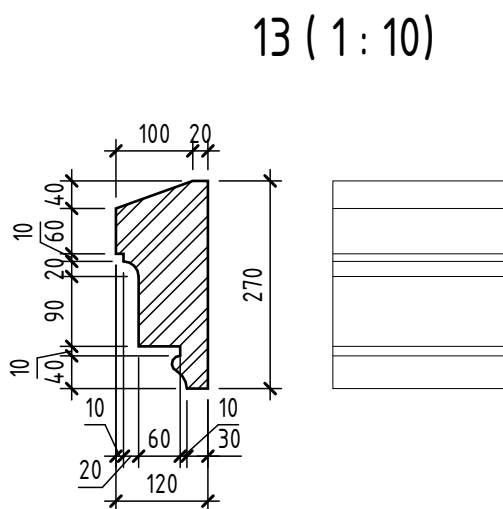
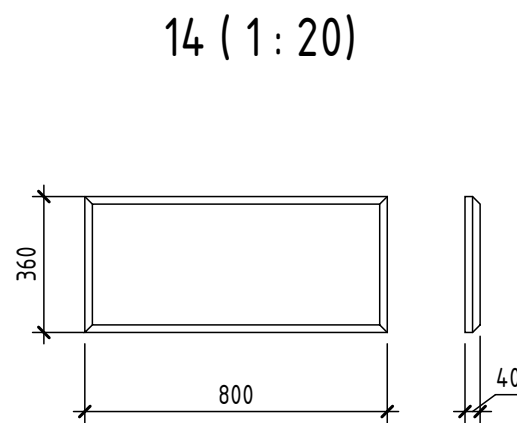
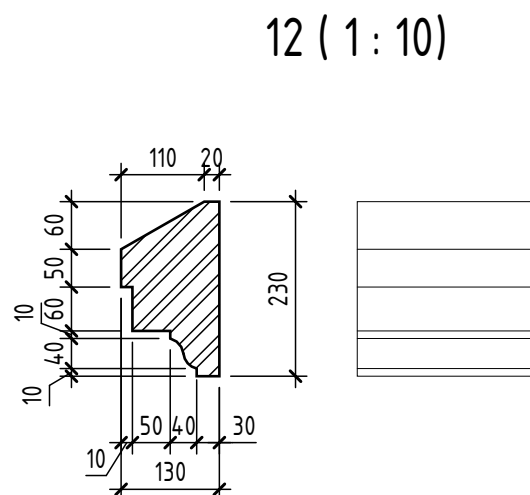


Фасад 3 (А-К') монтаж (1 : 100)

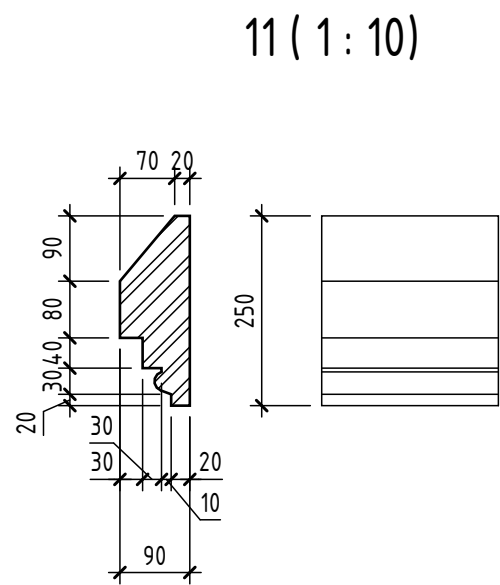

Ведомость архитектурных элементов фасада

№ поз.	Наименование	Ед. изм.	Количество	Примечание
2	Кронштейн, 800х530 (h)	шт.	4	
3	Тумба, 420х1030 (h)	шт.	14	
4	Карниз, 420х1030 (h)	шт.	14	
5	Оконное обрамление, 4020х4550 (h)	шт.	1	
6	Карниз подкровельный, H690	п.м.	121 150	
7	Балясина, H770	шт.	1	
8	Карниз, H690	п.м.	72 900	
9	Филленка, 1660х790 (h)	шт.	1	
10	Карниз, H390	п.м.	121 150	
11	Карниз, H250	п.м.	117 550	
12	Карниз, H230	п.м.	116 050	
13	Карниз, H270	п.м.	116 050	
14	Рустовой камень, 800х360 (h)	м.кв.	630	
15	Фрагмент кованого ограждения , 410х420 (h)	шт.	46	
16	Сандрик с лучковым фронтоном на кронштейнах, 1940х910 (h)	шт.	4	

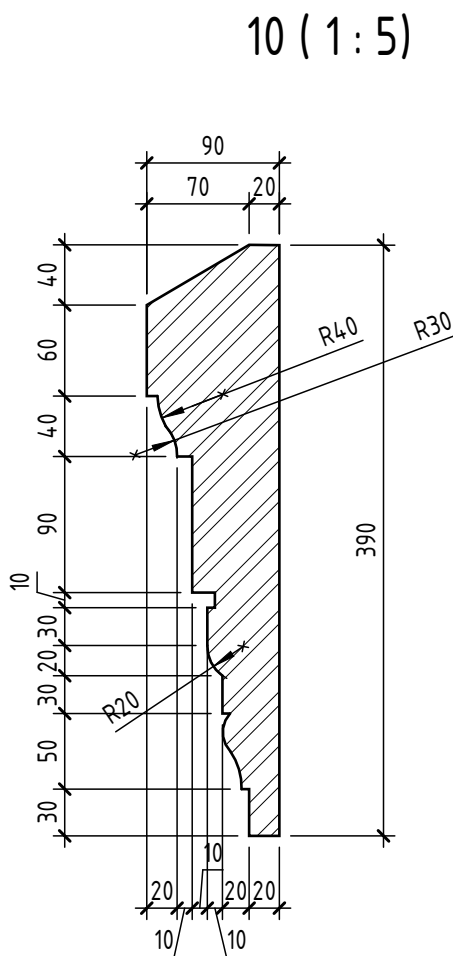

УСЛОВНЫЕ
ОБОЗНАЧЕНИЯ




- заменяемые и дополняемые элементы

15 (1 : 10)



16 (1 : 20)

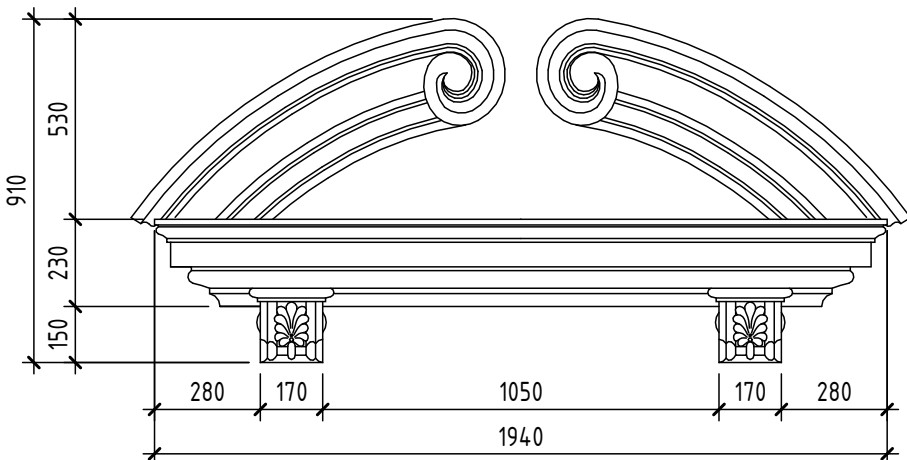

006/01/0048-20 - АР

Капитальный ремонт здания ФГБУ РГБ по адресу: г. Москва, ул Воздвиженка 1

Изм.	Кол.уч.	Лист	№ док.	Подп.	Дата	Корпус К.	Стадия	Лист	Листов
ГИП	Григорьев К.И.						РД	35	110
ГАП	Щетинин А.В.								
Разработал	Щетинин А.В.								
Н. контр.	Рожков А.Ф.								

Фасад 3 (А-К') Монтаж.



Формат А2А