




Сечение Е-Е
(1 : 100)

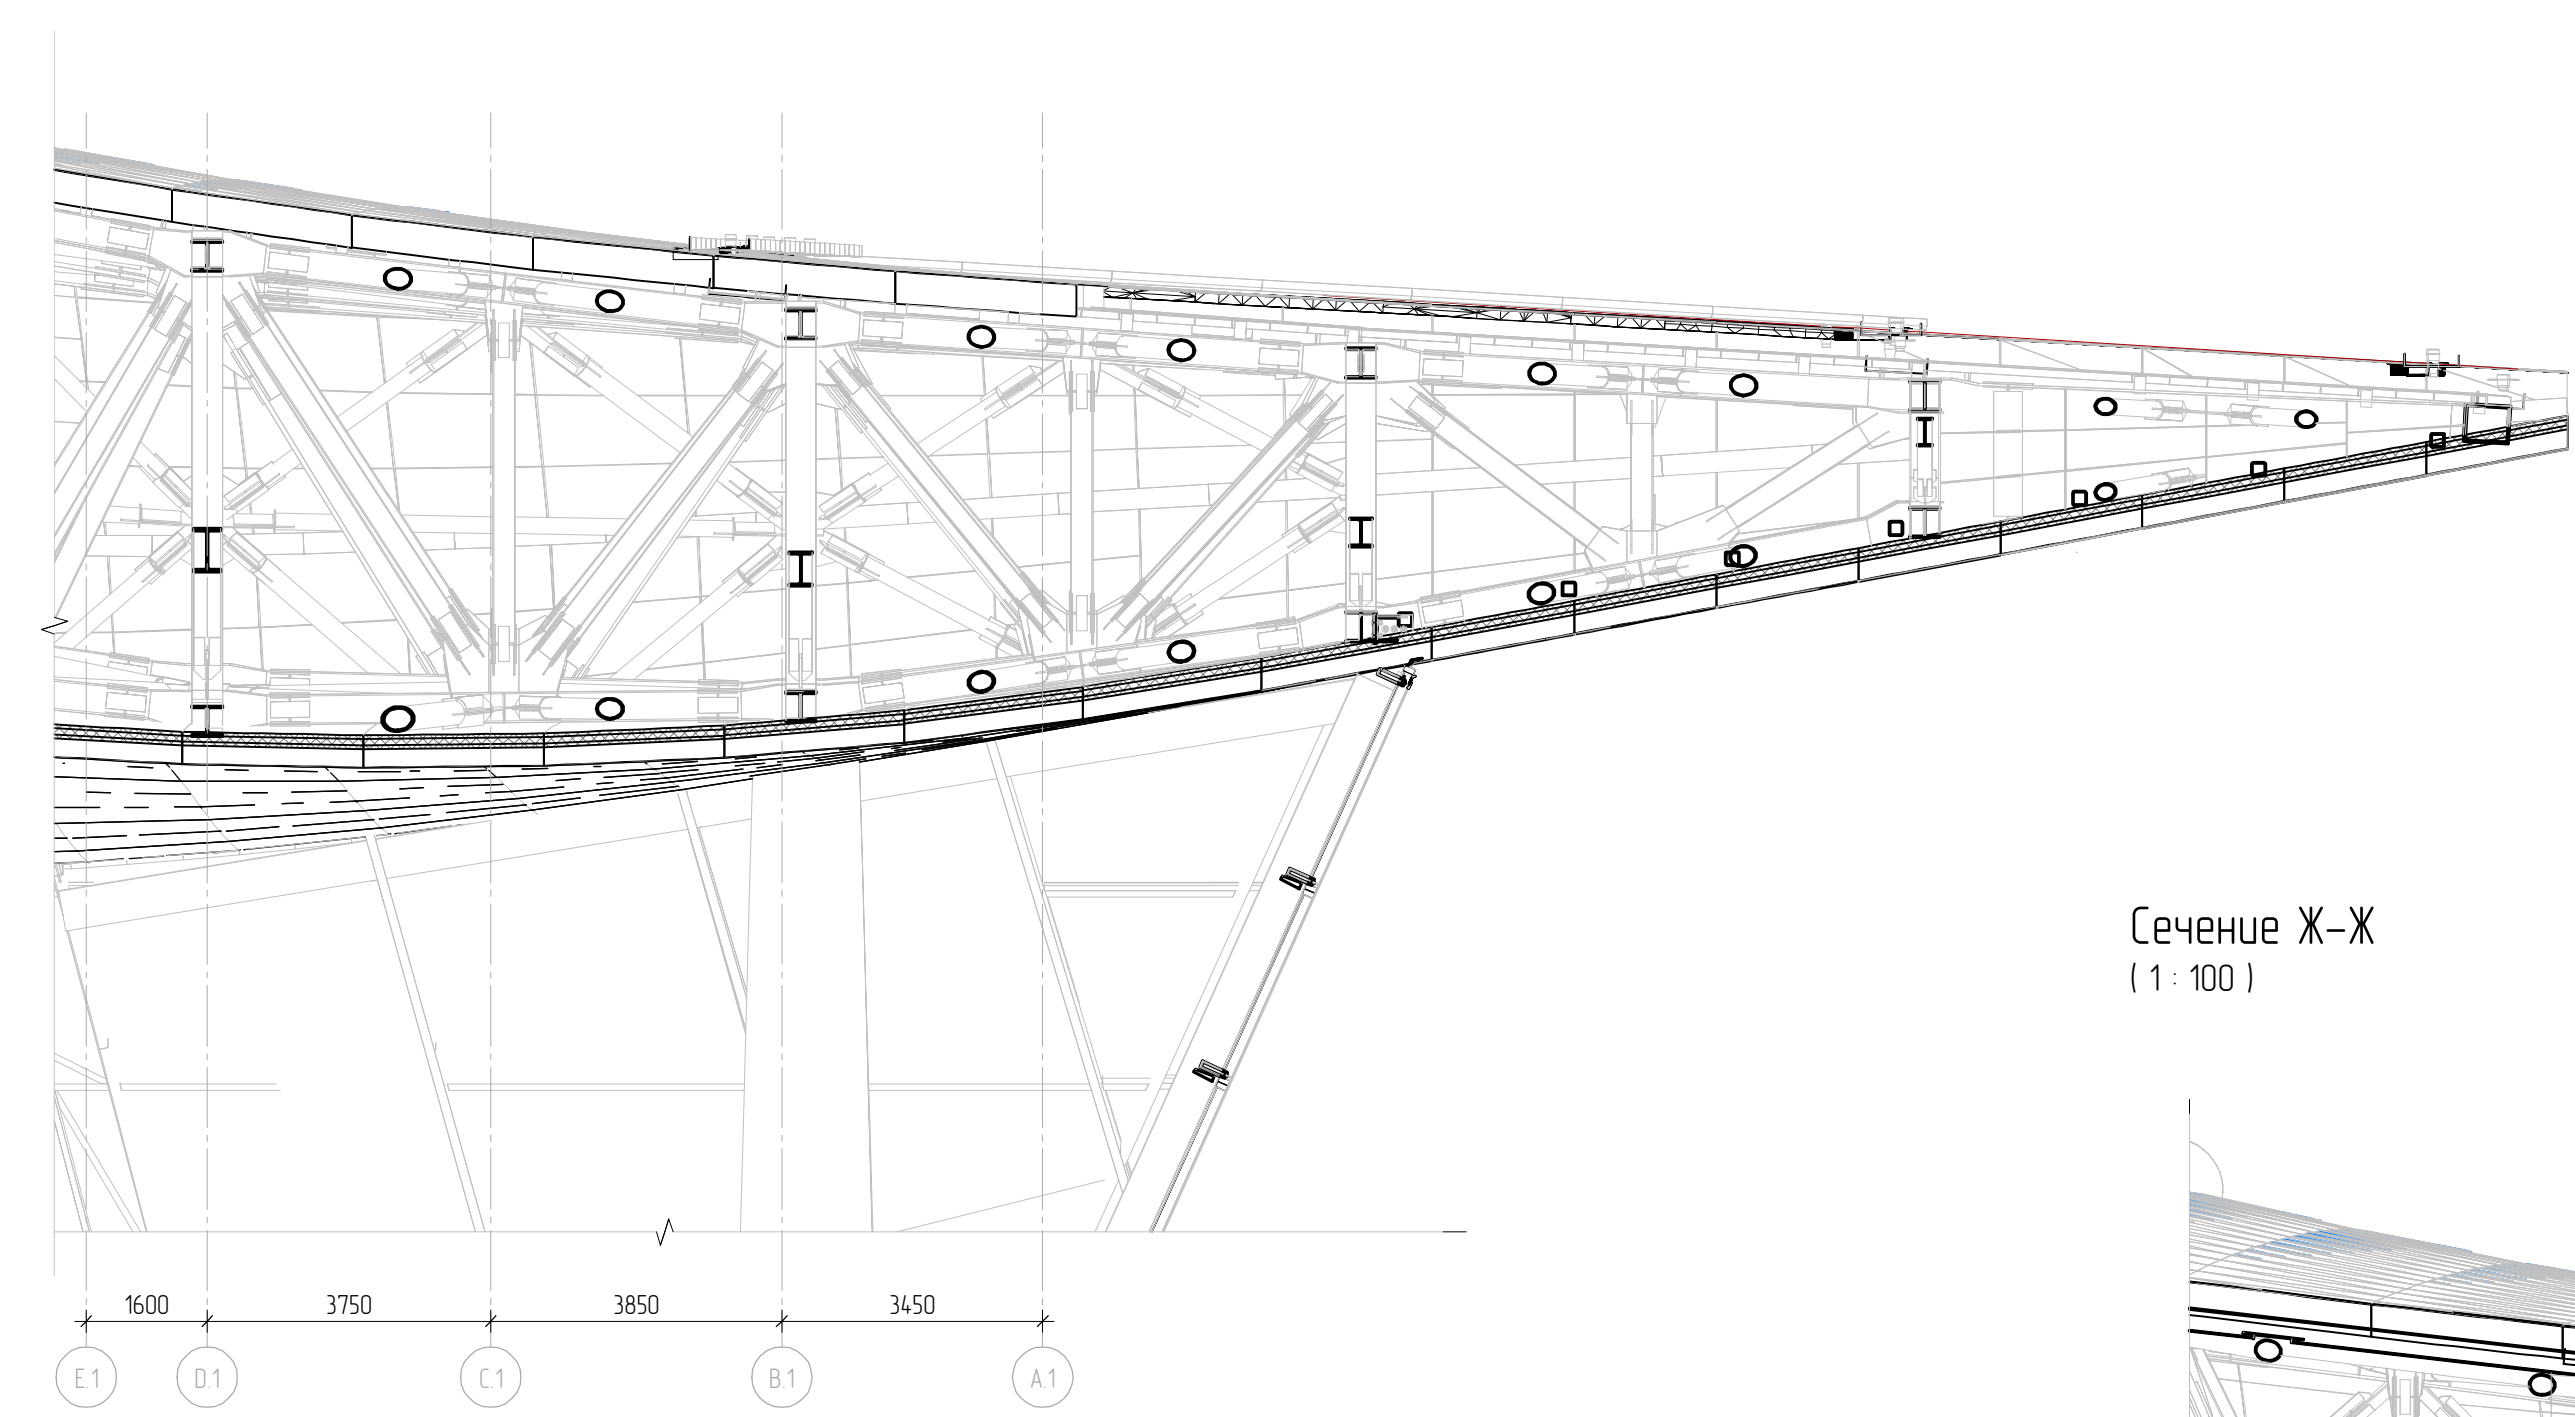


Сечение Ж-Ж
(1 : 100)

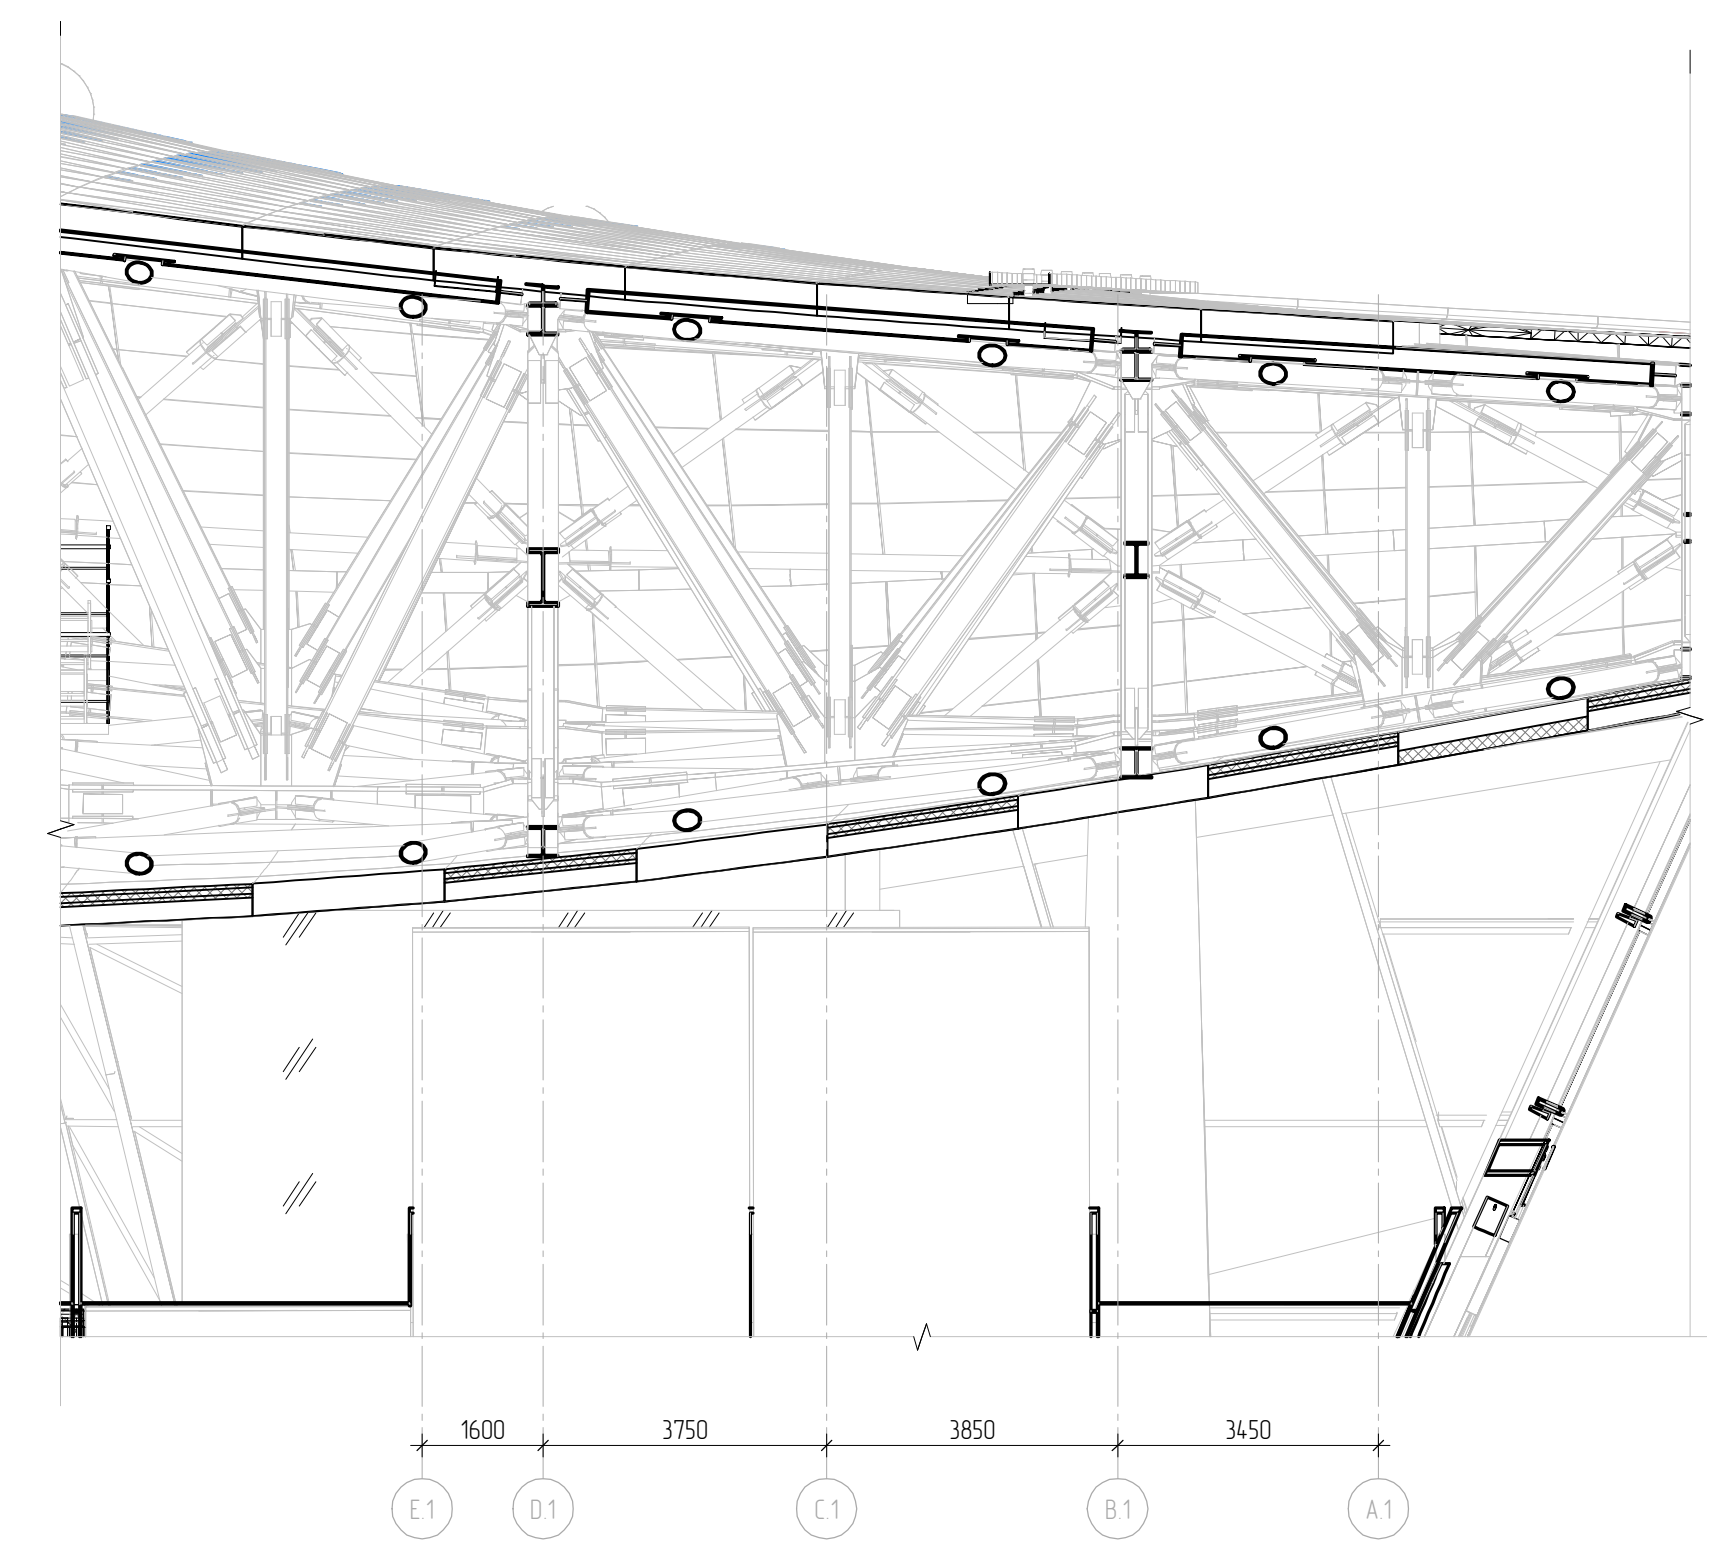

Сечение Д-Д
(1 : 100)

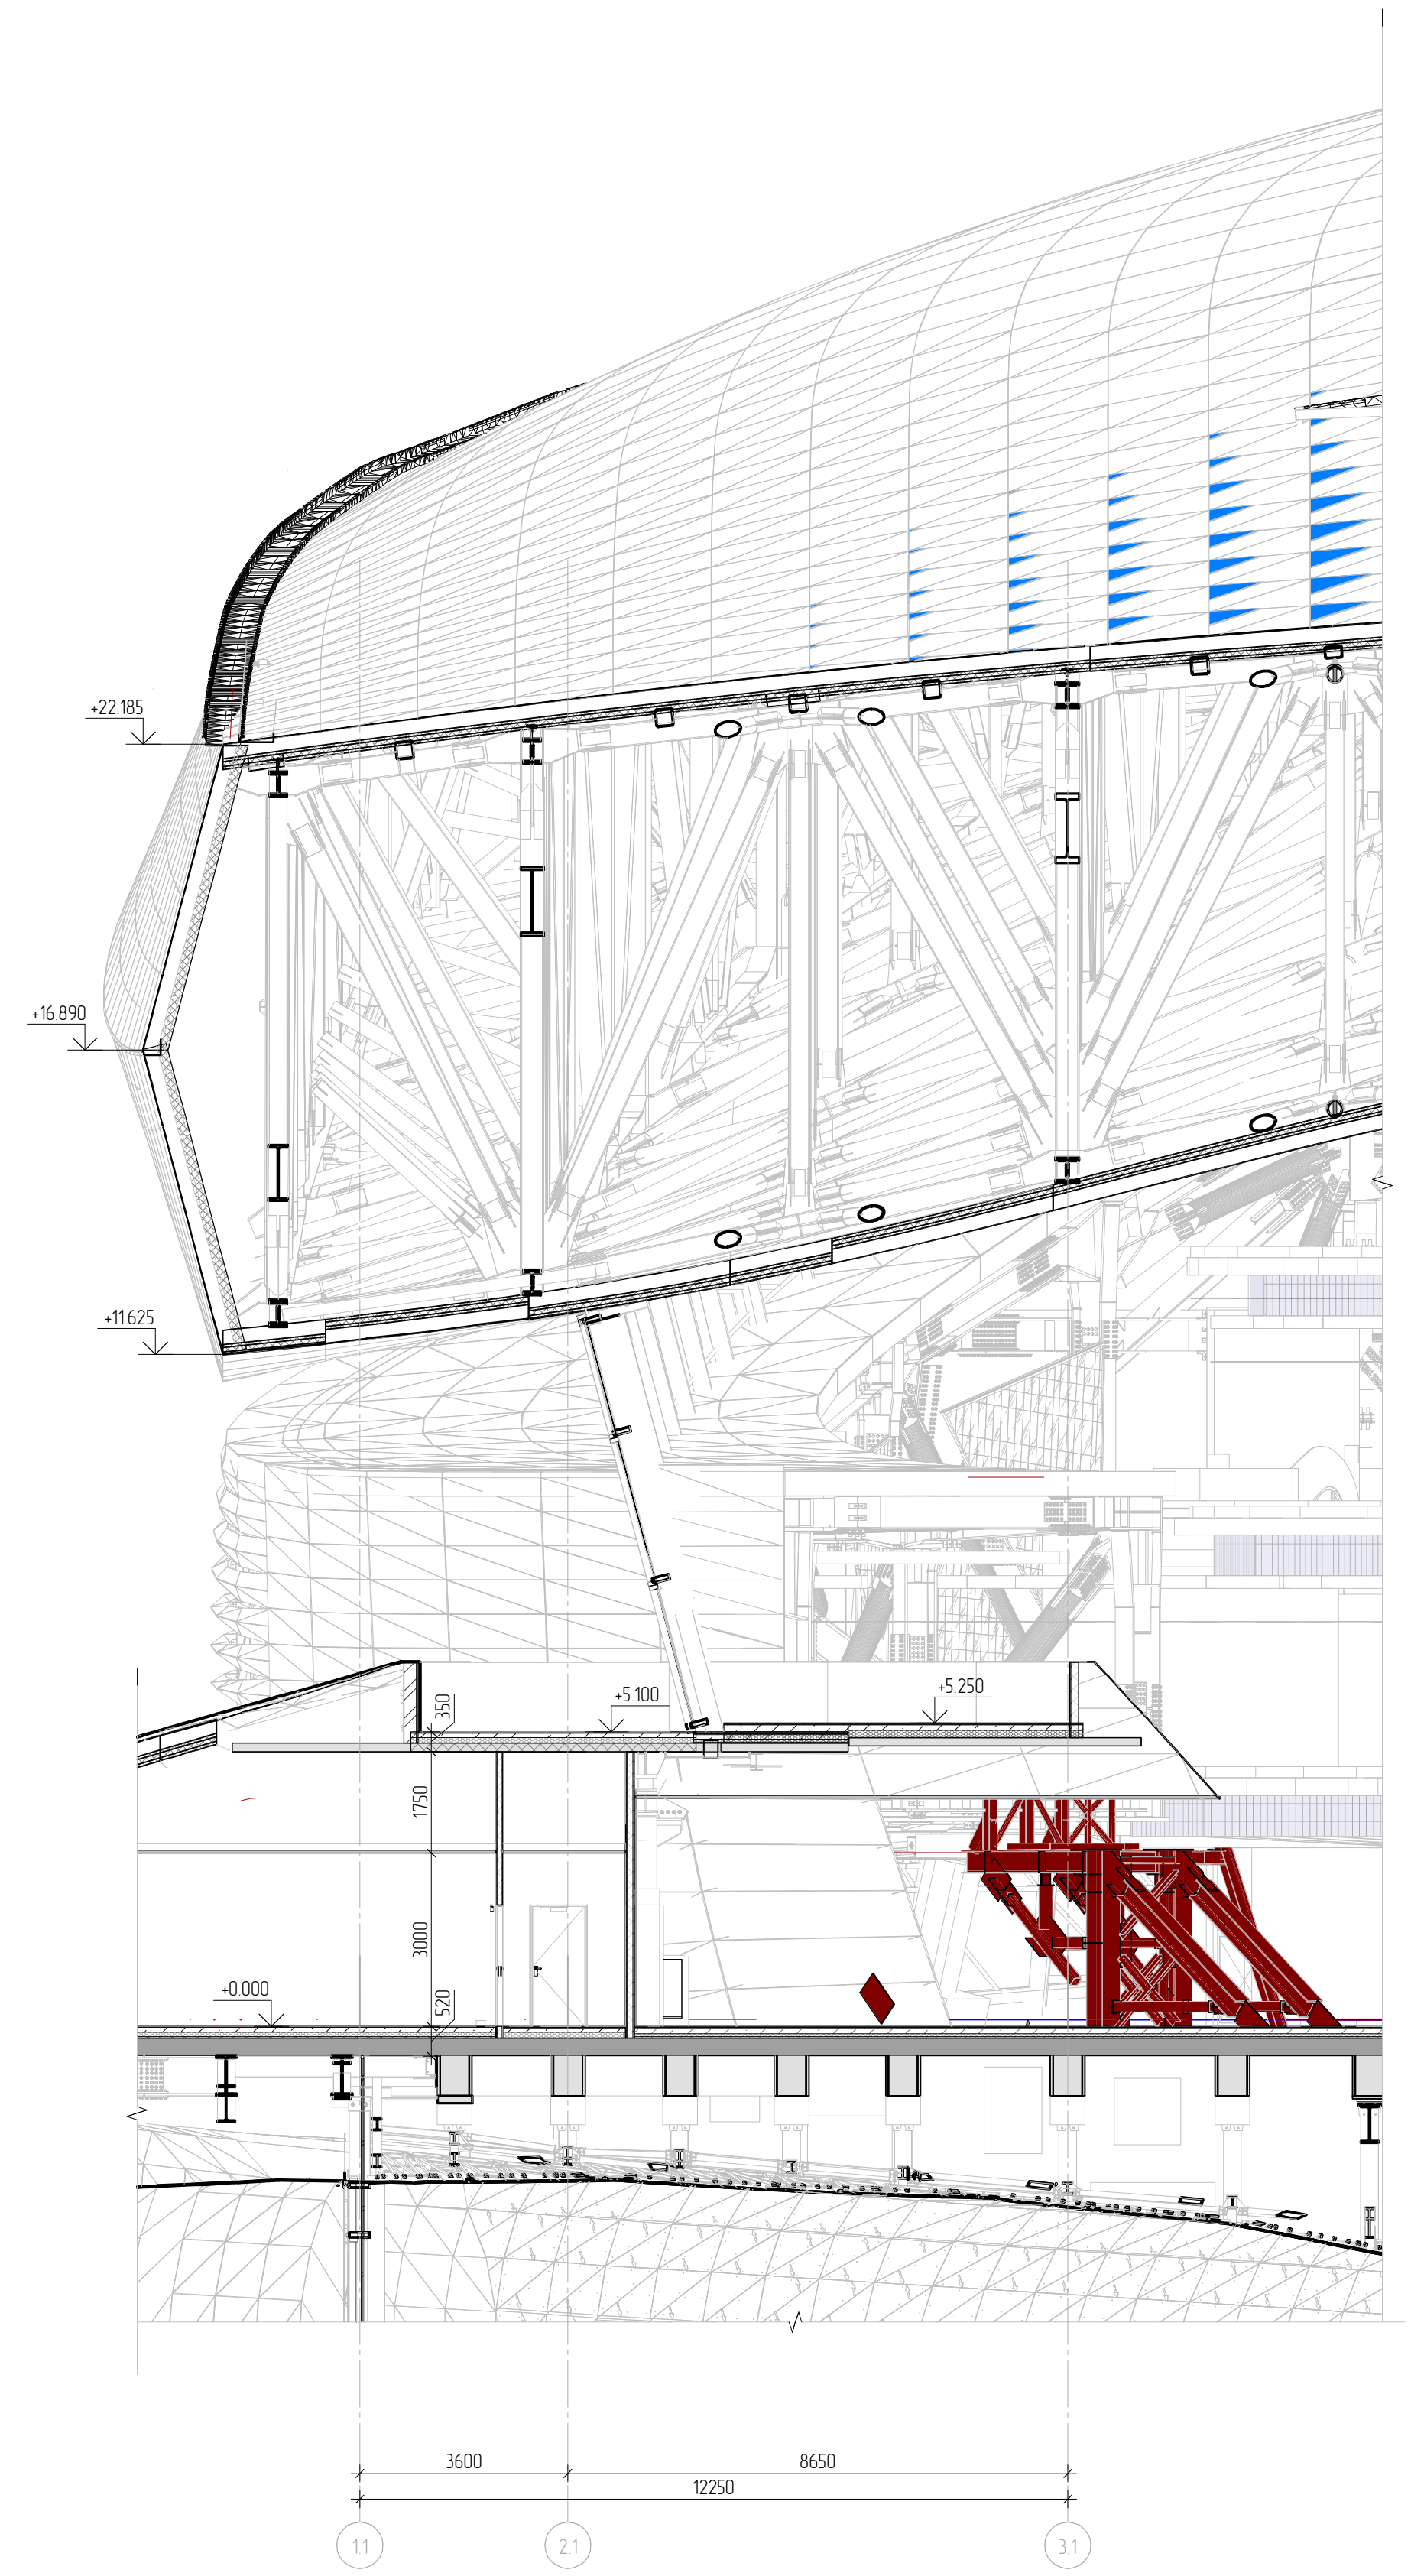

Сечение Г-Г
(1 : 100)

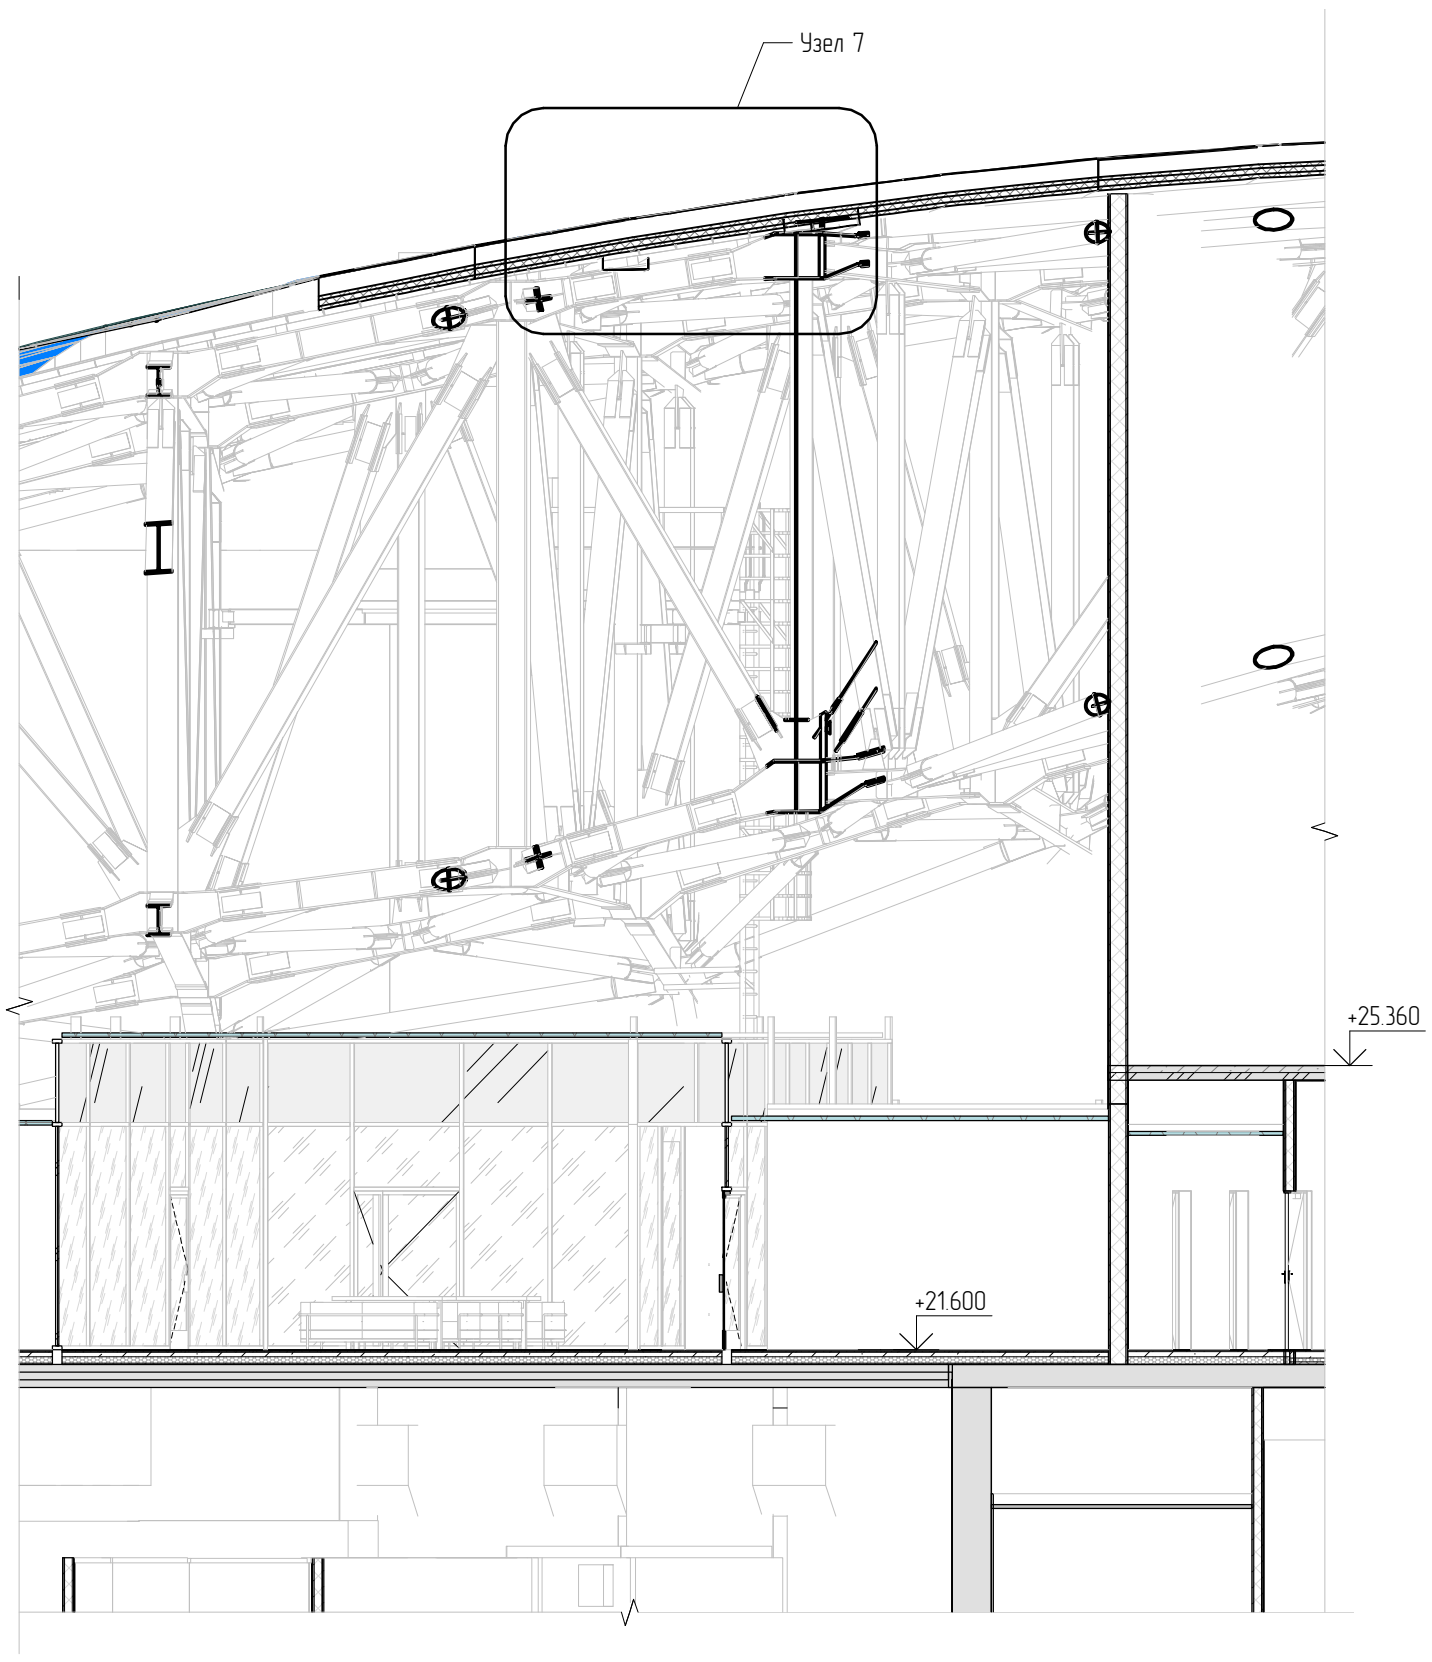

5	-	Зам	0919-25		02.06.25	MP-1000-1468П-00- AP1		
4	-	Зам	0864-25		26.05.25			
7	-	Зам	1234-25		28.07.25			
6	-	Зам	1006-25		16.06.25			
Изм	Колуч	Лист	На док	Подпись	Дата	По адресу: Российская Федерация, г. Севастополь		
Разработ	Семенов В			16.06.25				
Проверил	Иванов			16.06.25				
Главпр	Павлов			16.06.25				
ГИП	Голован			16.06.25				
Инж. контр.	Пронин			16.06.25		Узлы водоприемных лотков. Сечения оболочки (окончание)		
Нач. отд.	Пронин			16.06.25				
						Стация	Лист	Листов
						П	17	39
						Формат А1		