



Фасад Восточный (1 : 100)

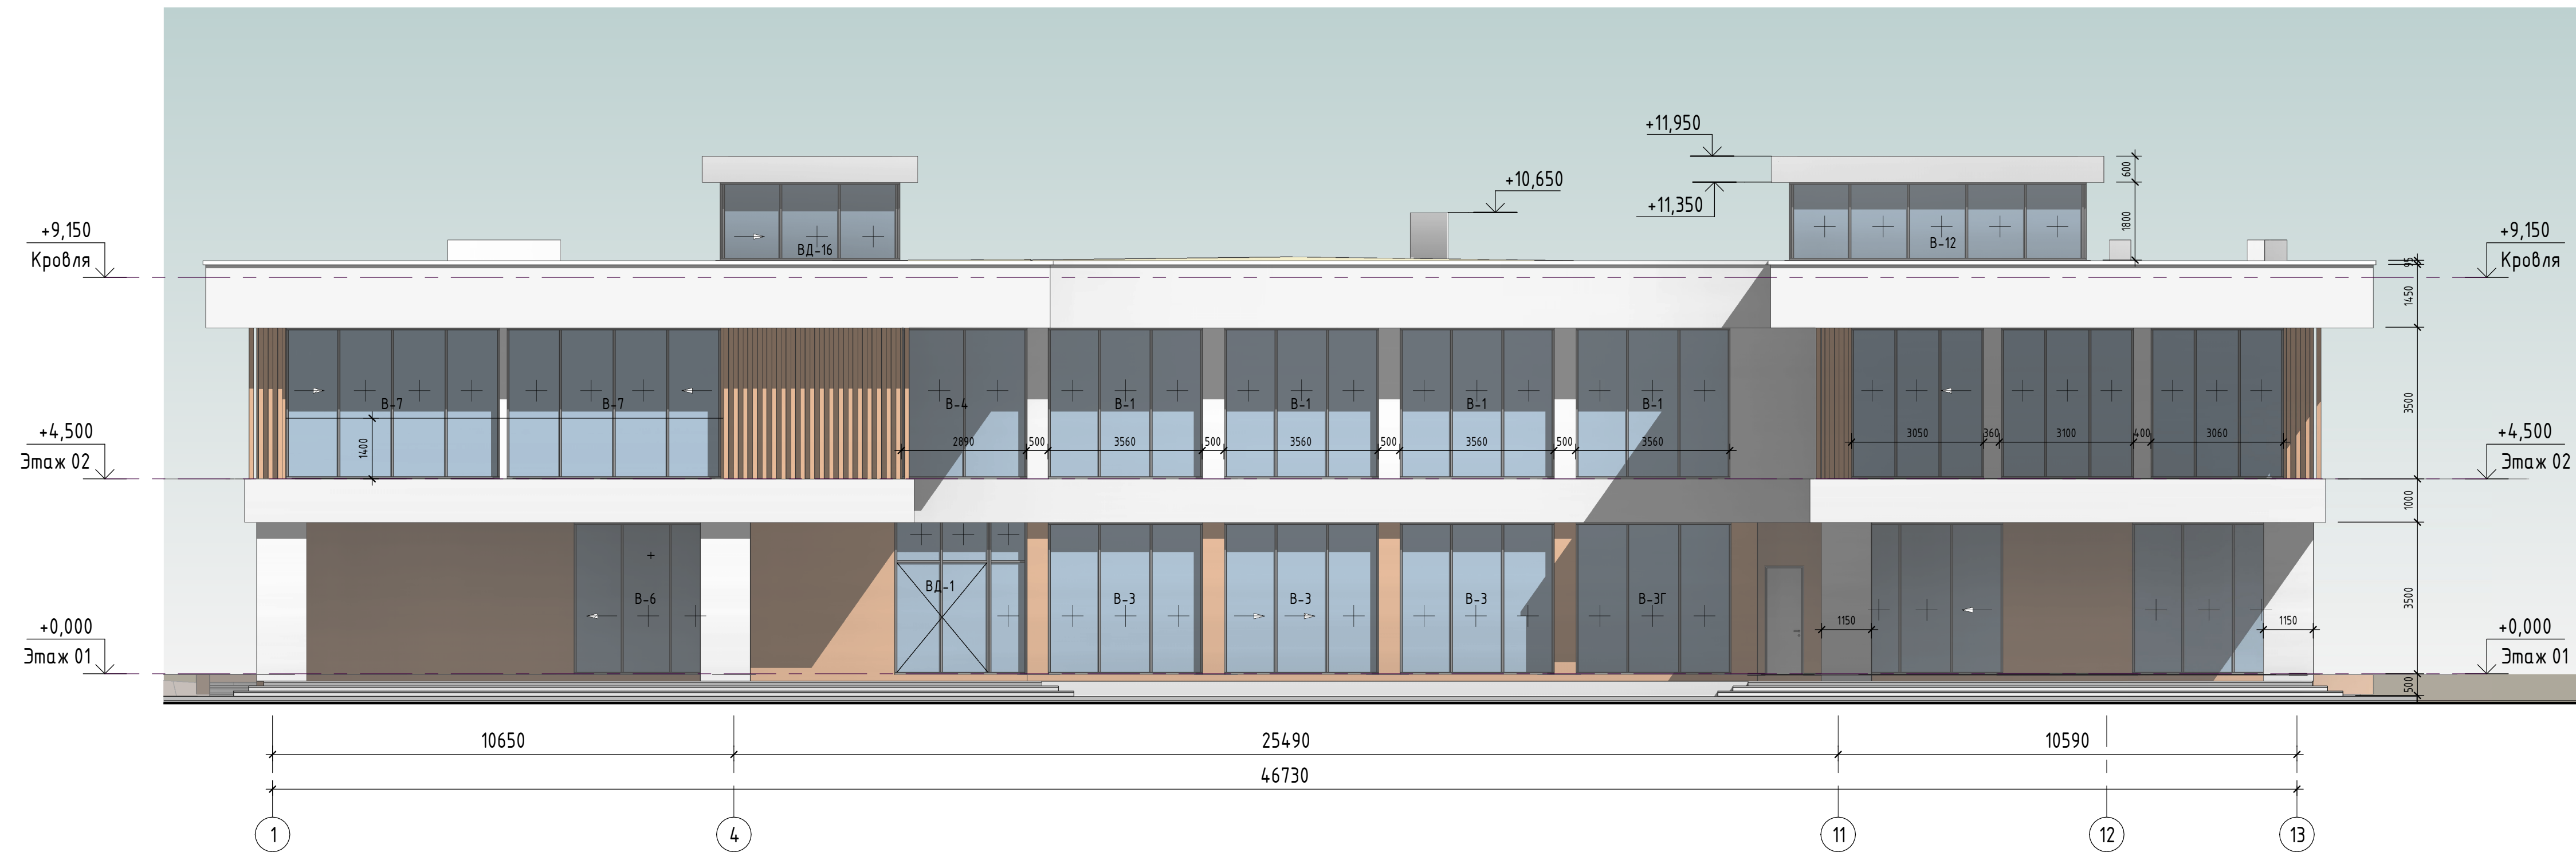

Фасад Западный (1 : 100)

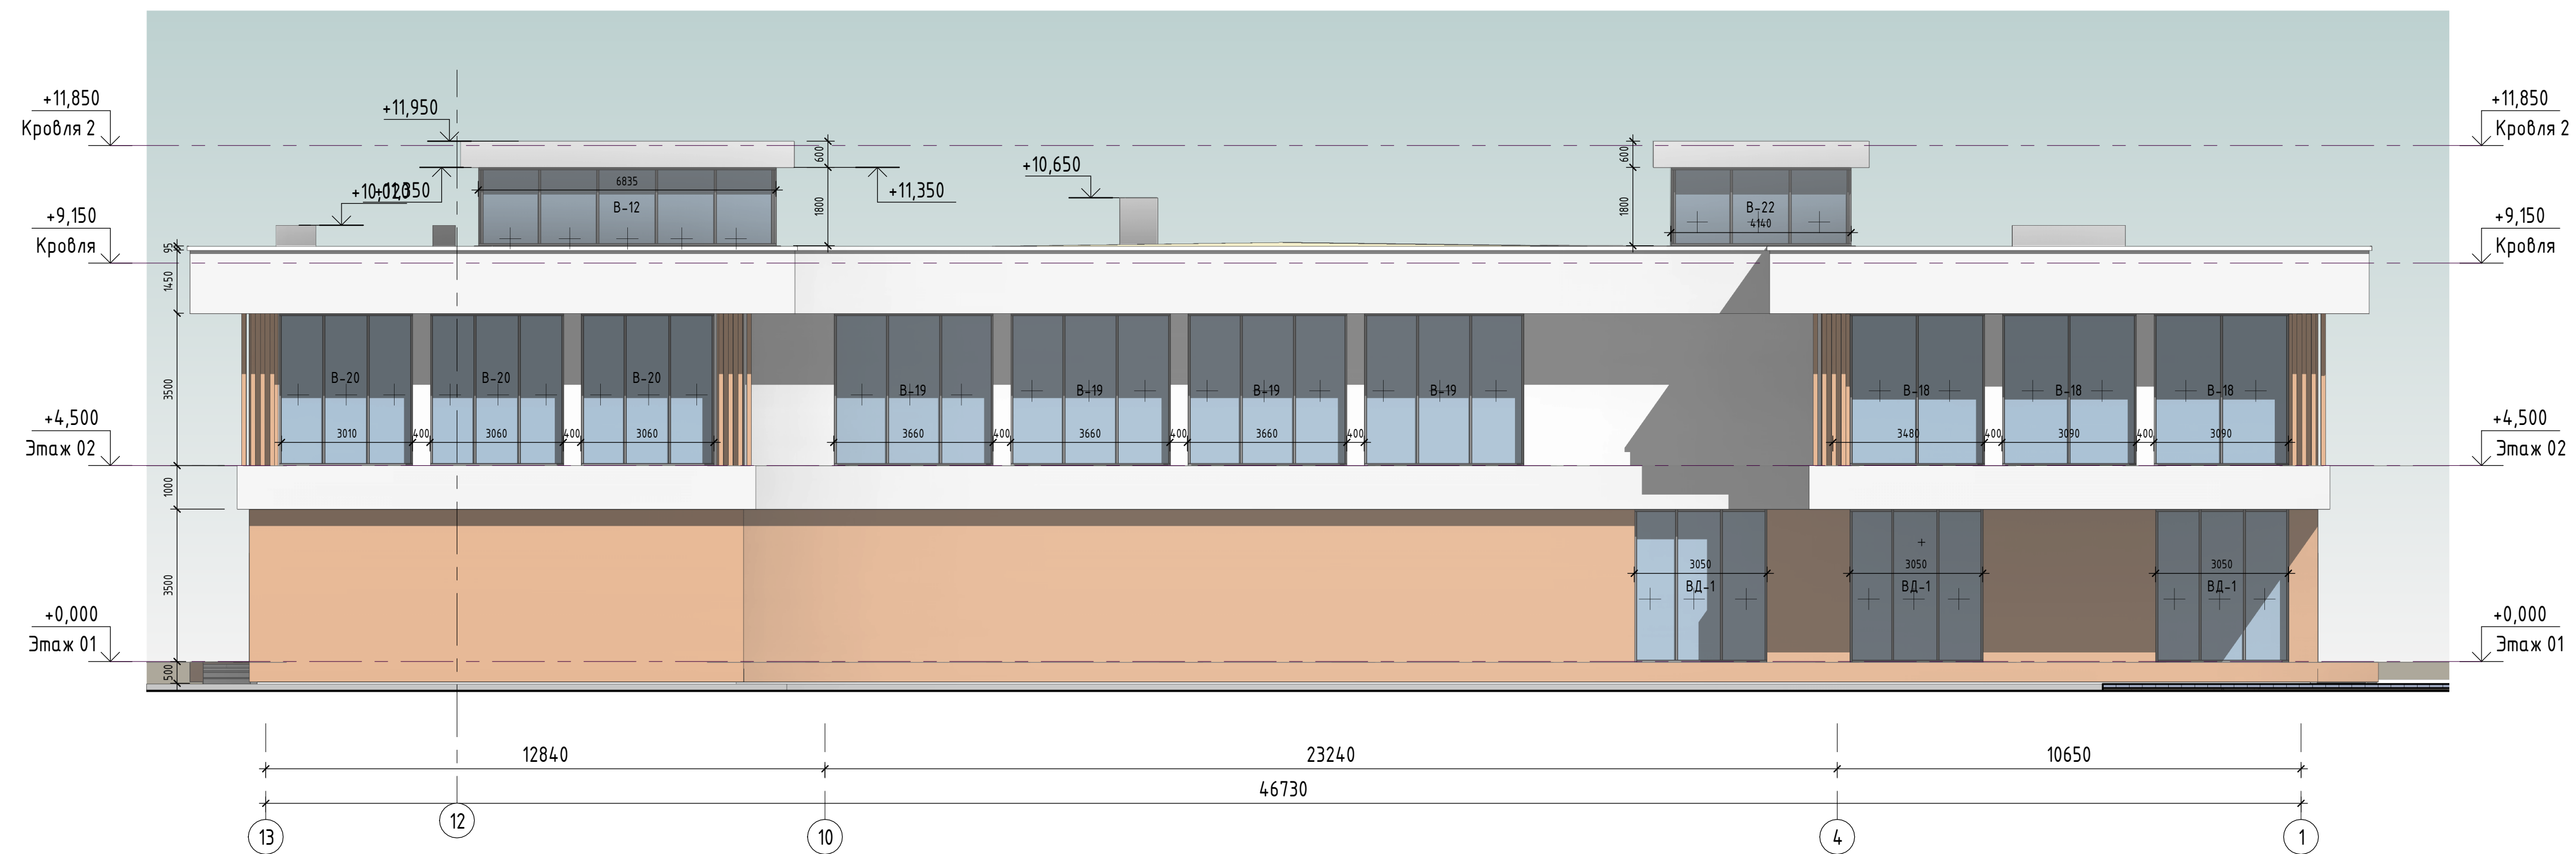

Ведомость отделки фасадов				
Тон	Наименование	Тип стены	Длина мм	Площадь м2
Свет				
	Керамогранит MATERICA BIANCO	См175Свет	18834	4,9,58
	Керамогранит MATERICA BIANCO	См615Свет	83470	14,9,29
			102304	198,87
Темный				
	Керамогранит MATERICA TORTORA	См6К575Темн	2400	10,32
	Керамогранит MATERICA TORTORA	См300КТемн	7413	3,16
	Керамогранит MATERICA TORTORA	См175Темн	70803	21,24
	Керамогранит MATERICA TORTORA	См615Темн	159165	562,28
			239780	597,00
			342084	795,87

Декоративные решетки из обработанного дерева, брус 100х100 с шагом 200мм

Фасад Восточный.....	24 м2
Фасад Западный.....	12 м2
Фасад Южный.....	59 м2
Фасад Северный.....	38 м2

Примечание: Данный лист смотреть с листами 19, 20, 24, 34

						05-05-18 - АРРП			
						Московская область, городской округ Красногорск, коттеджный поселок Кристалл Испра			
Изм.	Колуч.	Лист	№ док.	Подп.	Дата				
Директор	Космын С.							Статья	Лист
ГАП	Щетинин А.					Индивидуальный 2х этажный жилой дом.		РП	23.
ГИП	Теляков К.								18
Архитектор	Коналов В.								
Проверил	Теляков К.					Фасады Восточный и Западный			