


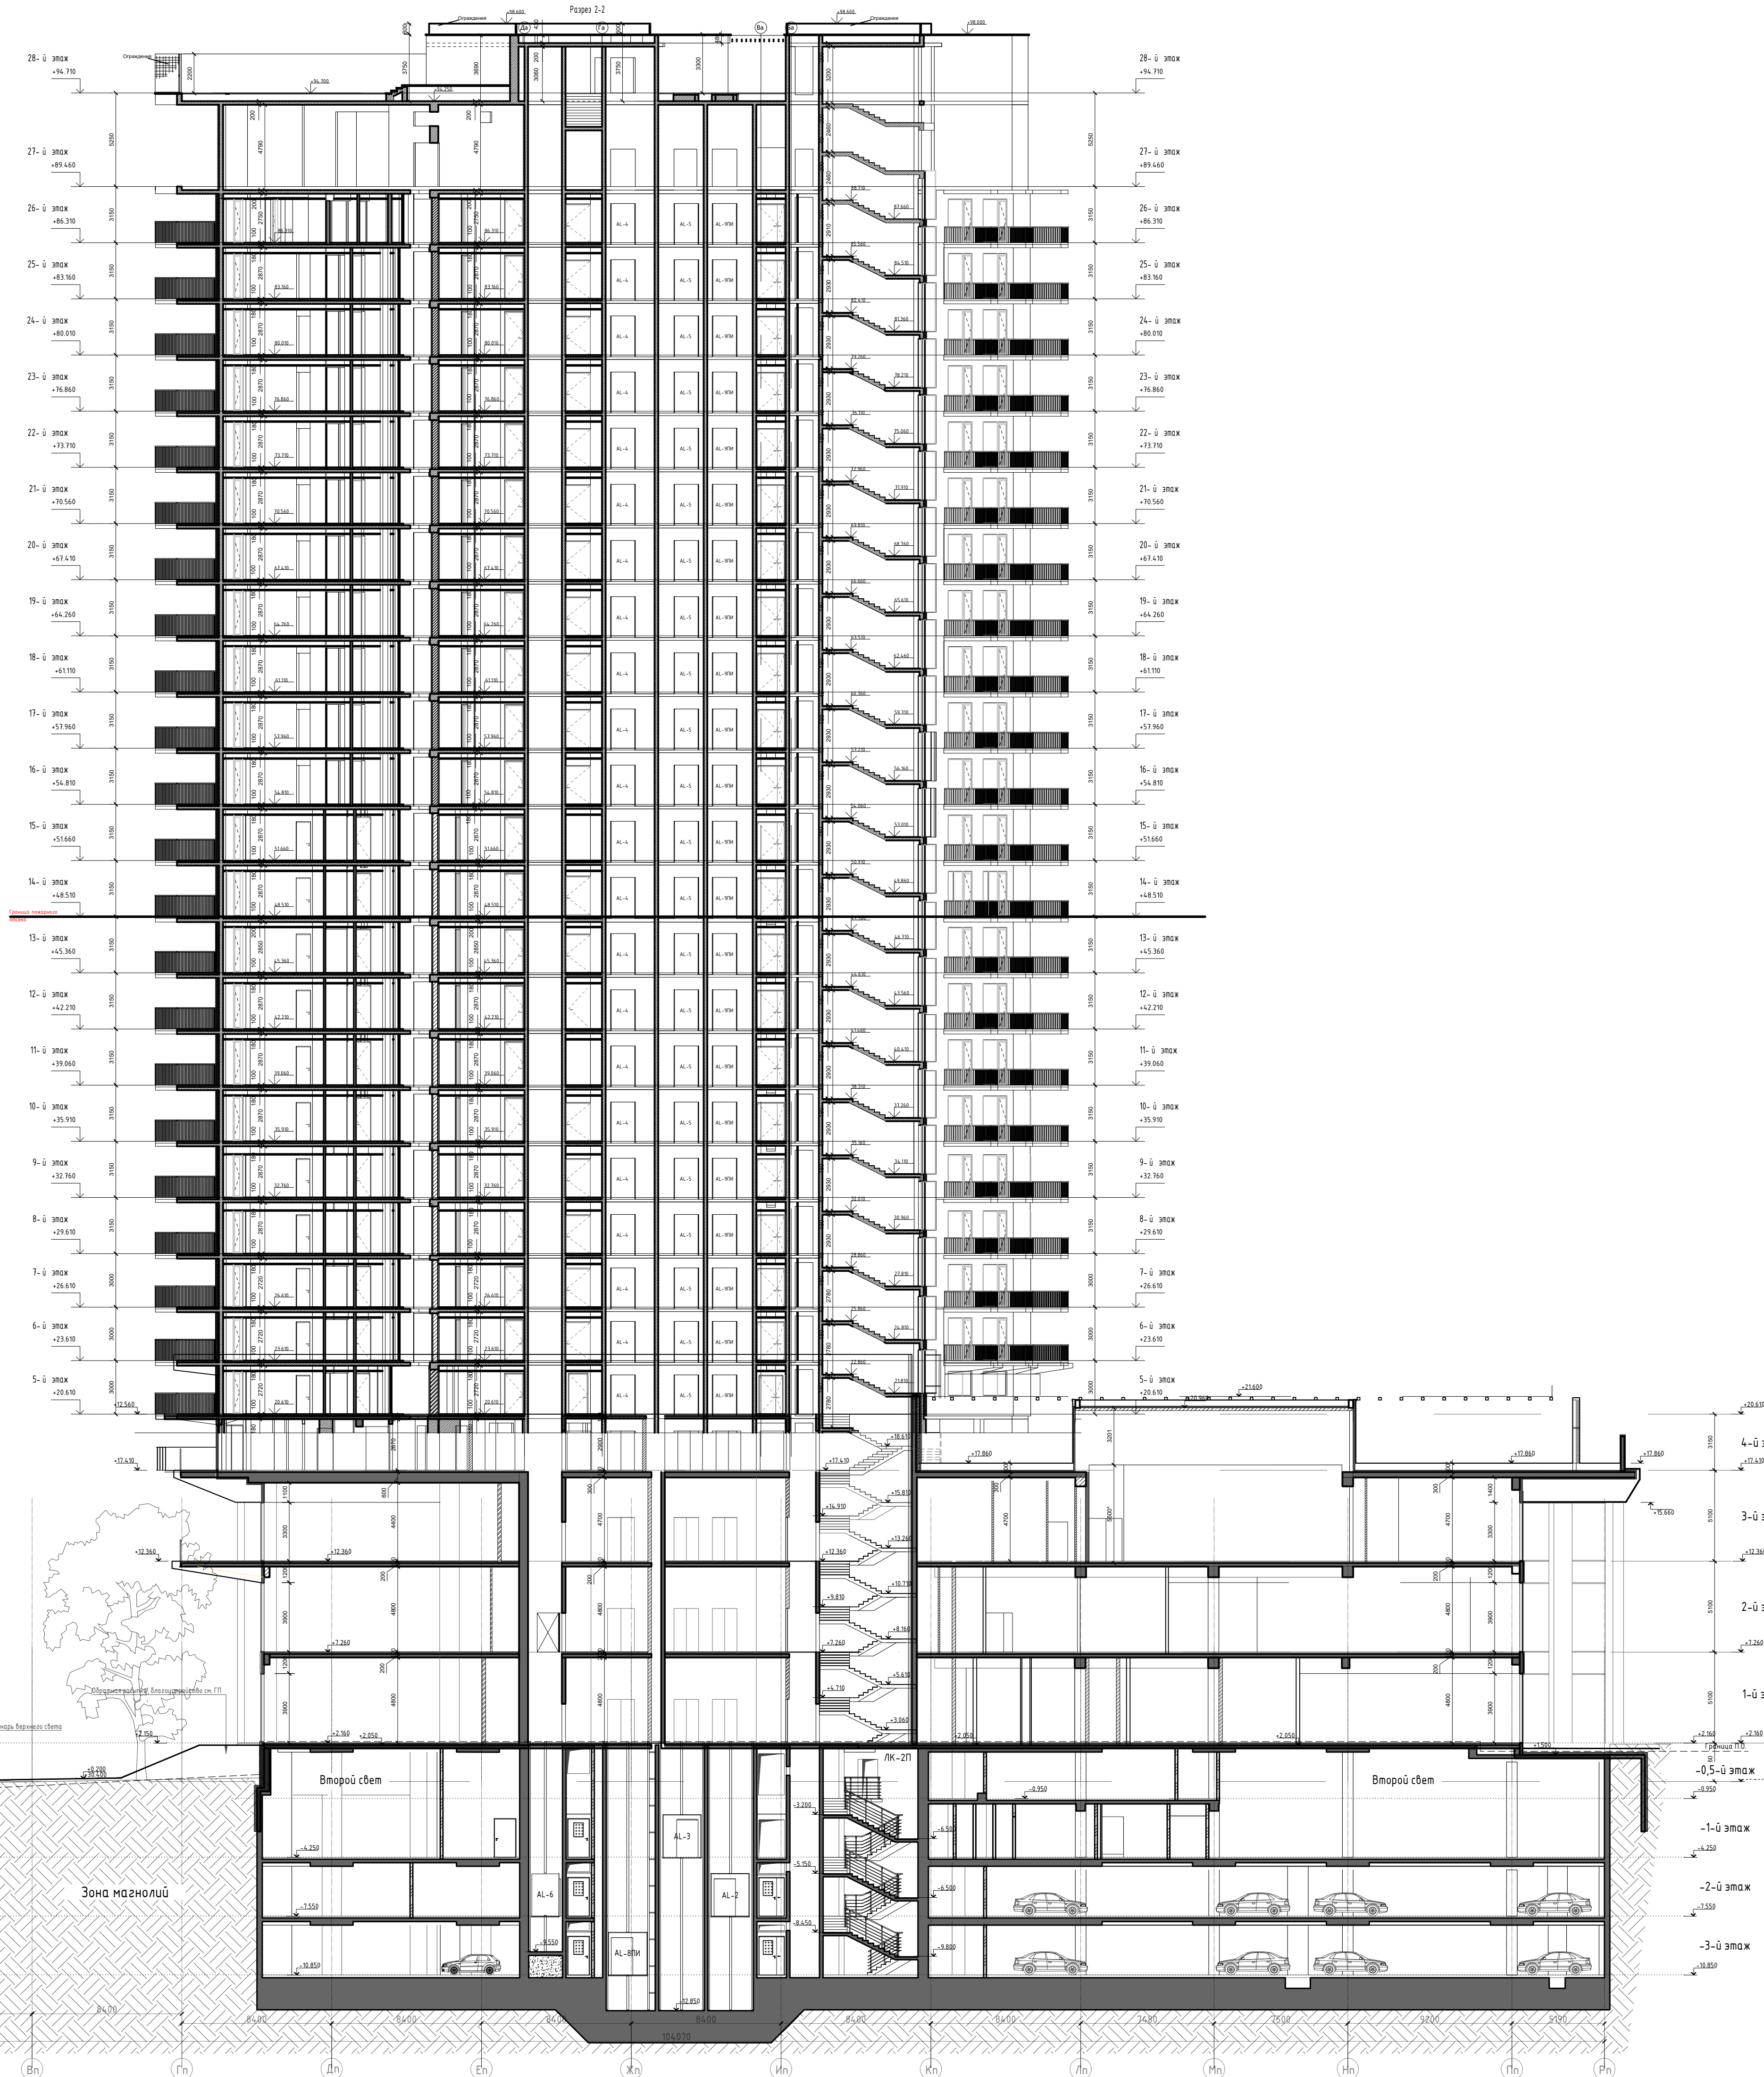

УСЛОВНЫЕ ОБОЗНАЧЕНИЯ:

- Ж/б конструкции
- Кладка из газобетонных блоков
- Перегородки по системе Кнауф или аналогичной
- Утеплитель - минераловатная плита
- 1. Внутренние и наружные многослойные горизонтальные и вертикальные конструкции см. АР1, лист 29
- 2. Размеры со * уточняются на стадии РД
- Ф5 Тип конструкции см. лист 34, АР1



						MP-1535-01-AP				
						Развитие гостиницы «Приморская» в г. Сочи. Строительство нового				
						корпуса гостиницы, расположенного по адресу: г. Сочи, Центральный район, ул. Соколова, д. 1. Этап 3				
6	-	Зам.	0372-26	<i>Лав</i>	12.05.26					
Изм.	Кол.уч.	Лист	№ док.	Подпись	Дата					
Разраб.		Корнеев		<i>Корнеев</i>	12.05.26					
Проверил		Галабузда		<i>Лав</i>	12.05.26					
						Архитектурные решения		Стадия	Лист	Листов
								П	26	34
Н.контр.		Гордеев		<i>Гордеев</i>	12.05.26	Разрез 2-2.		METROPOLIS		