
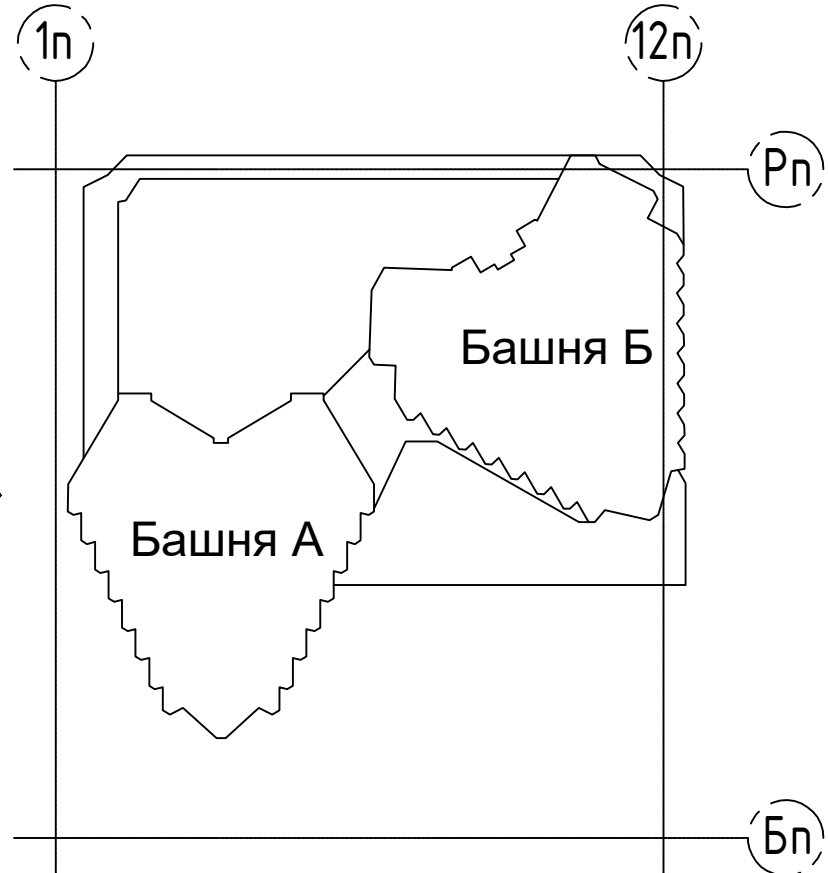


Условные обозначения:

- Декоративная фасадная "камышковая" штукатурка по технологии CERESIT WM, окраска силиконовой фасадной краской (Ral 0908505) по согласованному образцу. (1.1 - стены 4-28 этажи; 1.2 - потолки балконов 5-28 этажей)
- Панели из высокопрочного архитектурного бетона Артбетоника RAL с индексом EG-45 П SCH1687 на подсистеме Hilti" max. высота вертикального габарита 5100 мм (или аналог) по согласованному образцу на фасадной системе Hilti VFH ArchBeton (или аналог) в системе навесного фасада на подсистеме со скрытым креплением
- Стеклалит RAL по согласованию с Заказчиком в составе стеклопакета в системе витражного остекления
- Прозрачное стекло в составе стоечно-ригельного остекления
- Рамы стоечно-ригельных стеклопрозрачных конструкций (Стилобат, 4-27 этажи) Ral 1035
- Ограждение металлическое балконов и отливов торцов балкона, окраска AkzoNobel код: YW358F, цвет блеск: GRIS2500 муар, описание: YW358F INTD2525 SABLE GRIS2500 FM10
- Жалюзированная декоративная фасадная безрамная вентрешетка, алюминиевый профиль ламели типа RENSON , порошковая окраска по согласованию с Заказчиком Коэффициент живого сечения решеток не ниже 0,5. По всей плоскости - стальная сетка 3х3мм , порошковая окраска в цвет ламелей , крепление по технологии подрядчика
- Жалюзированная решетка в структуре стоечно-ригельного остекления- ламелей типа RENSON , порошковая окраска по согласованию с Заказчиком Коэффициент живого сечения решеток не ниже 0,5. По всей плоскости - стальная сетка 3х3мм , порошковая окраска в цвет ламелей , крепление по технологии подрядчика по витражам
- Ограждение карель окраска по RAL 1035 матовый, образец по согласованию Заказчика
- Ограждение стеклянное (триплекс) 28 этажа

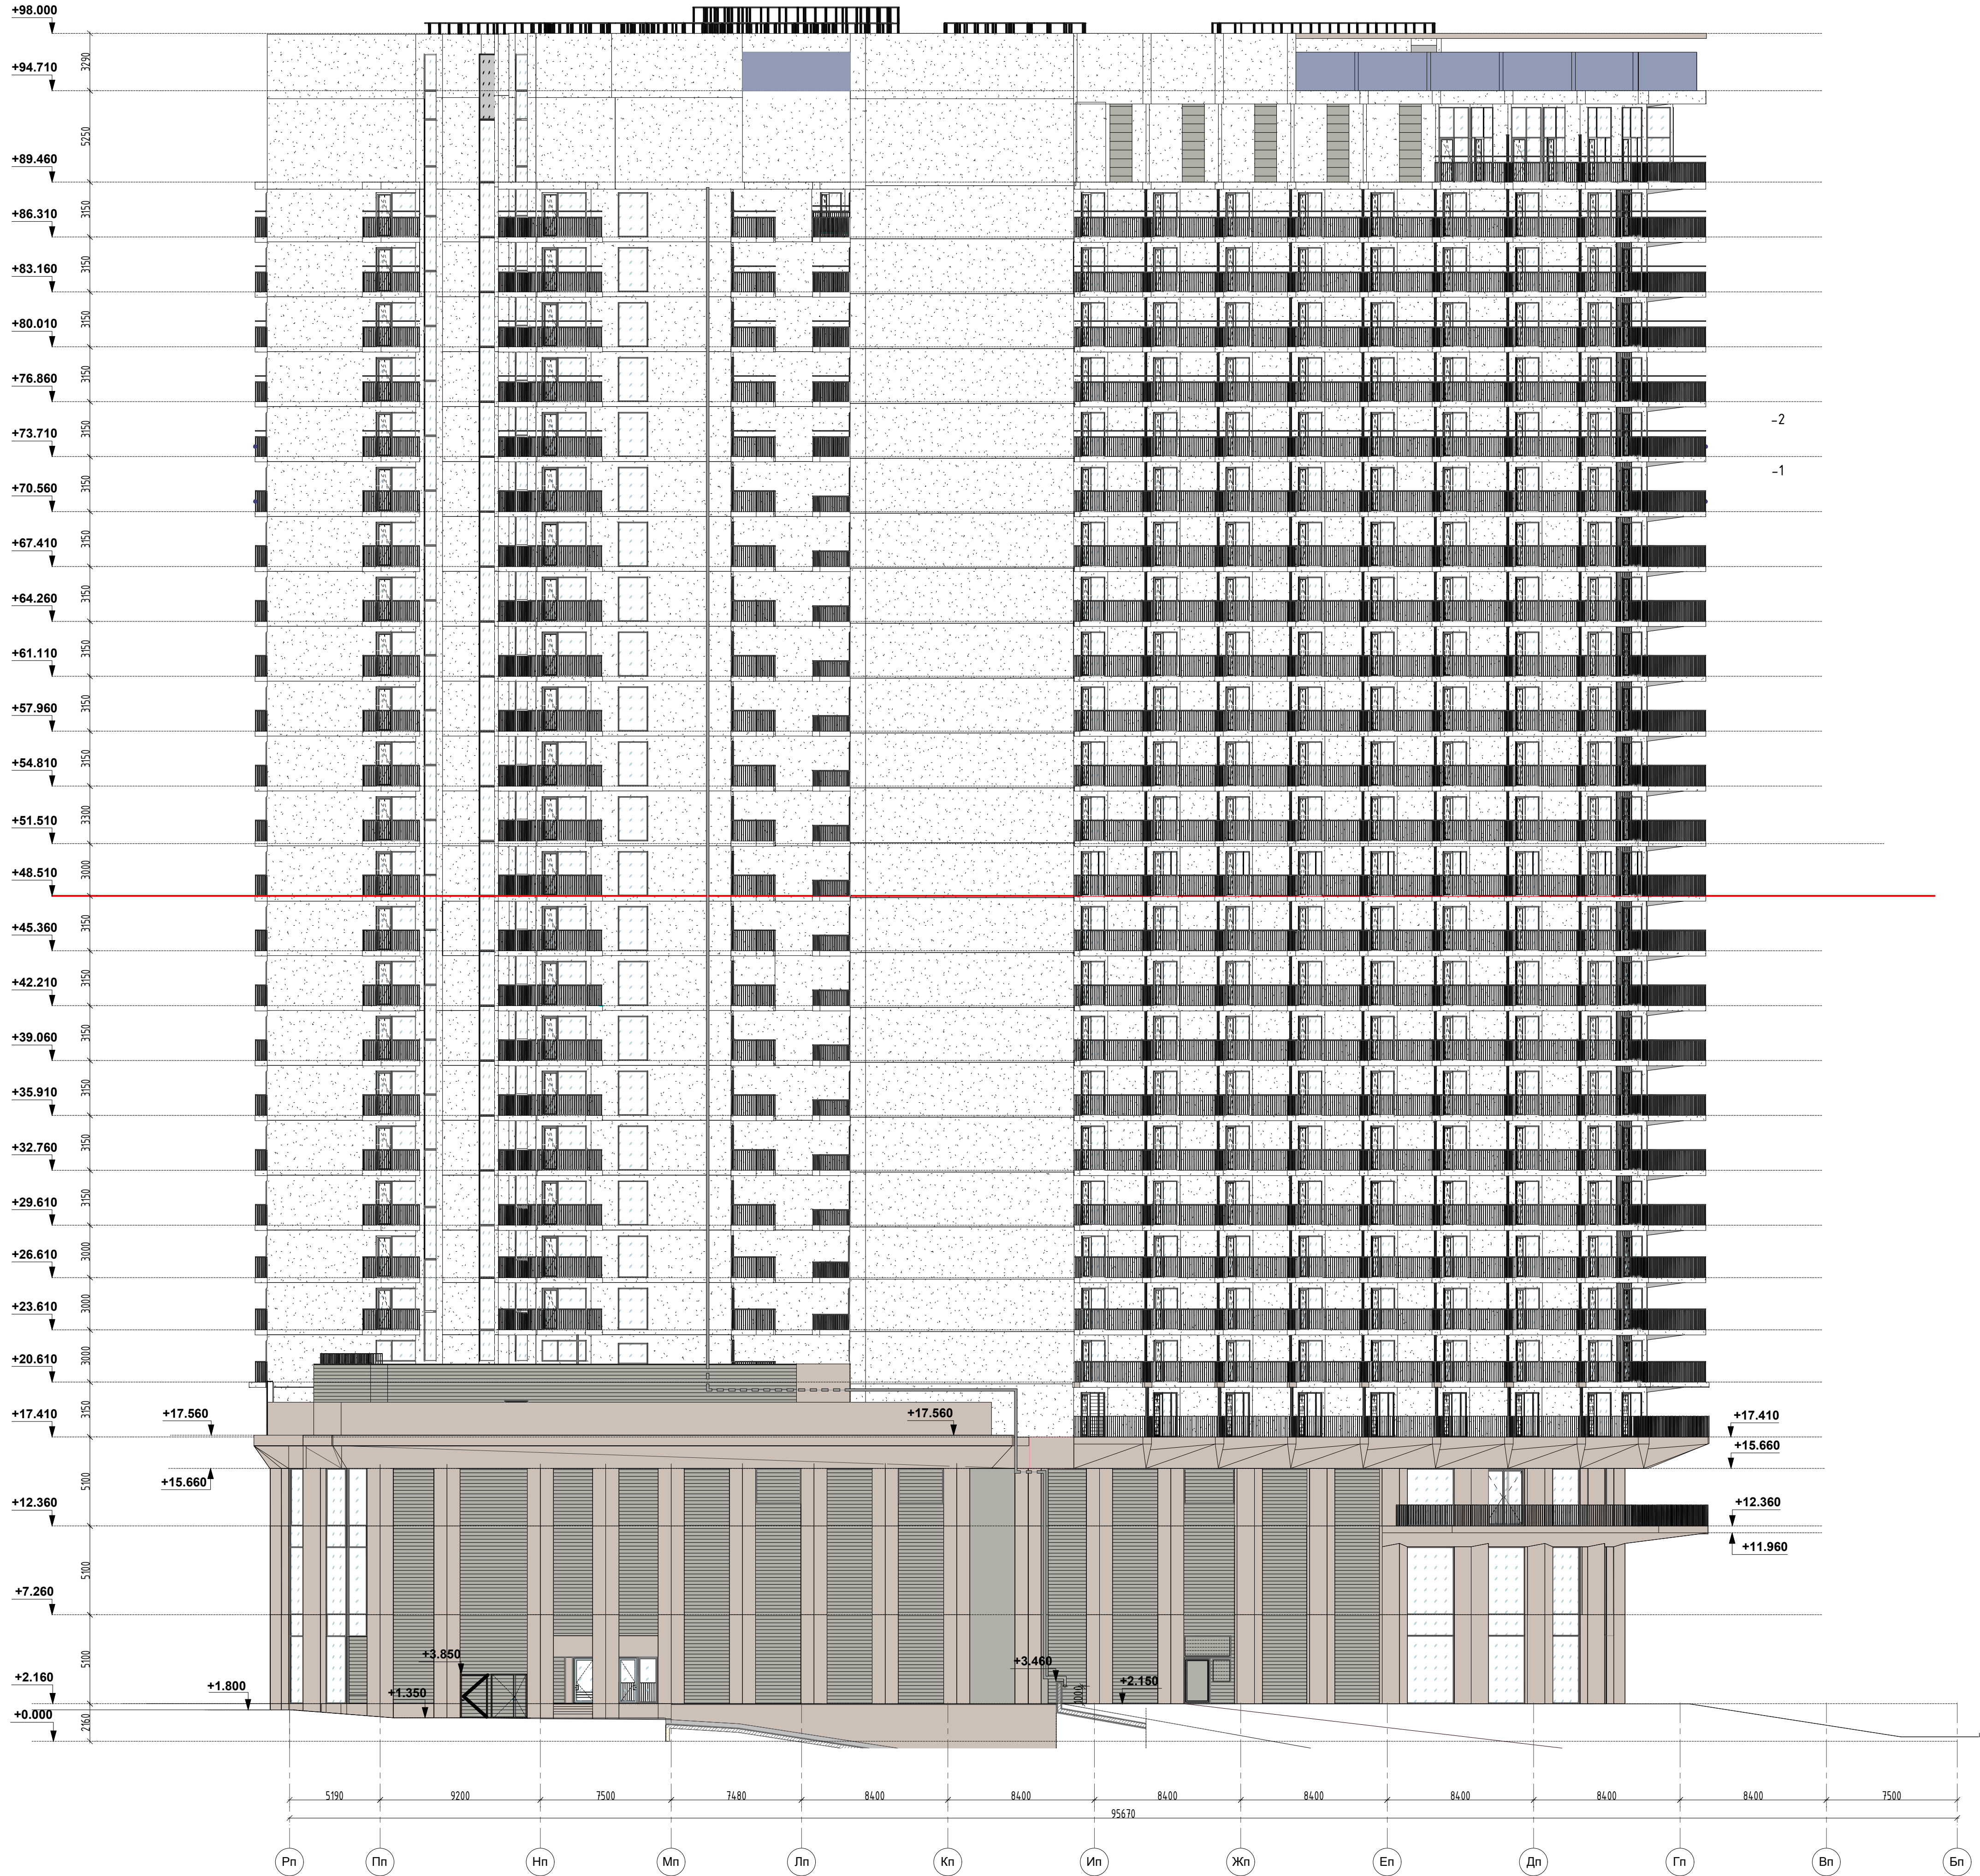

|          |           |      |         |                |          |   |        |            |        |
|----------|-----------|------|---------|----------------|----------|---|--------|------------|--------|
|          |           |      |         |                |          | MP-1535-01-AP   |        |            |        |
|          |           |      |         |                |          | Развитие гостиницы «Приморская» в г. Сочи. Строительство нового корпуса гостиницы, расположенного по адресу: г. Сочи, Центральный район, ул. Соколова, д. 1. Этап 3 |        |            |        |
| 6        | -         | Зам. | 0372-26 | <i>Лев</i>     | 12.05.26 | Архитектурные решения   | Стадия | Лист       | Листов |
| Изм.     | Кол.уч.   | Лист | № док.  | Подпись        | Дата     |   | П      | 30         | 34     |
| Разраб.  | Корнеев   |      |         | <i>Корнеев</i> | 12.05.26 |   |        |            |        |
| Проверил | Галабузда |      |         | <i>Лев</i>     | 12.05.26 |   |        |            |        |
| Н.контр. | Гордеев   |      |         | <i>Гордеев</i> | 12.05.26 | Фасад в осях Рп-Бп.   |        | METROPOLIS |        |