
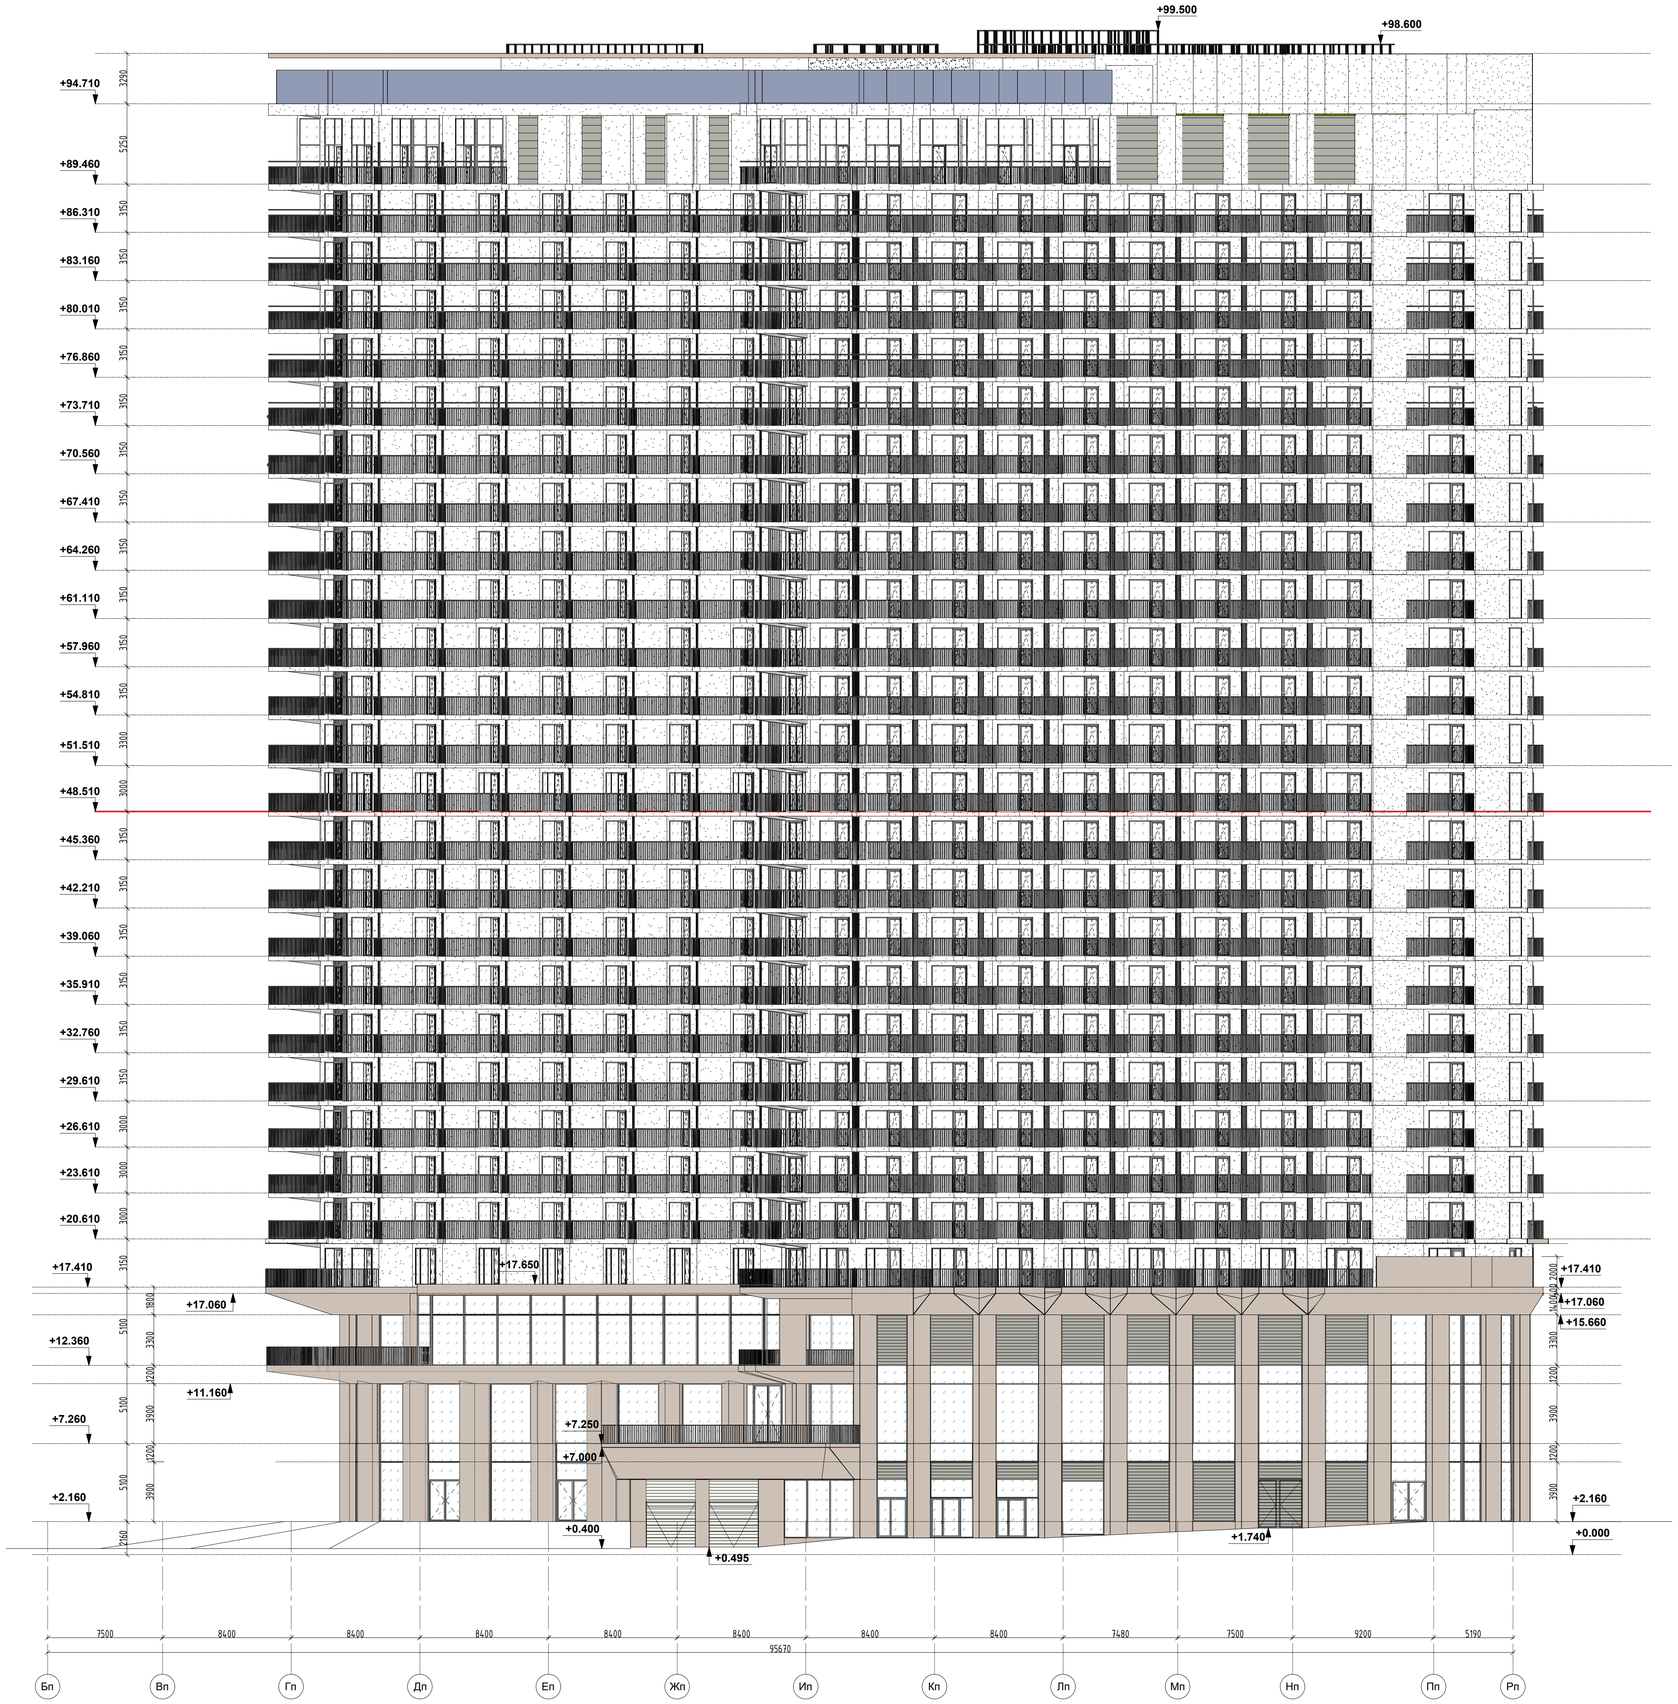


Условные обозначения:

- Декоративная фасадная "камешковая" штукатурка по технологии CERESIT WM, окраска силиконовой фасадной краской (Ral 0908505) по согласованному образцу. (1.1 - стены 4-28 этаж; 1.2 - потолки балконов 5-28 этажей)
- Панели из высокопрочного архитектурного бетона Артбетоника RAL с индексом EG-45 П SCH1687 на подсистеме Hilti" max. высота вертикального габарита 5100 мм (или аналог) по согласованному образцу на фасадной системе Hilti VFH ArchBeton (или аналог) в системе навесного фасада на подсистеме со скрытым креплением
- Стеналит RAL по согласованию с Заказчиком в составе стеклопакета в системе витражного остекления
- Прозрачное стекло в составе стоечно-ригельного остекления
- Рамы стоечно-ригельных стеклопрозрачных конструкций (Стилобат, 4-27 этажи) Ral 1035
- Ограждение металлическое балконов и отливов торцов балкона, окраска AkzoNobel код: YW358F, цвет блеск: GRIS2500 муар, описание: YW358F INTD2525 SABLE GRIS2500 FM10
- Жалюзированная декоративная фасадная безрамная вентрешетка, алюминиевый профиль ламели типа RENSON , порошковая окраска по согласованию с Заказчиком Коэффициент живого сечения решеток не ниже 0,5. По всей плоскости - стальная сетка 3х3мм , порошковая окраска в цвет ламелей , крепление по технологии подрядчика
- Жалюзированная решетка в структуре стоечно-ригельного остекления- ламелей типа RENSON , порошковая окраска по согласованию с Заказчиком Коэффициент живого сечения решеток не ниже 0,5. По всей плоскости - стальная сетка 3х3мм , порошковая окраска в цвет ламелей , крепление по технологии подрядчика по витражам
- Ограждение кровель окраска по RAL 1035 матовый, образец по согласованию Заказчика
- Ограждение стеклянное (триплекс) 28 этажа

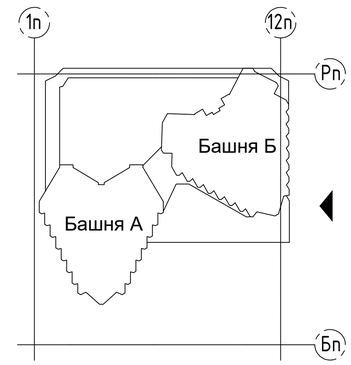

Согласовано

Согласовано

Взам. инв.No.

Подп. и дата

Инв.No. подл.

6	-	Зам.	0372-26		12.05.26
Изм.	Кол.уч	Лист	No.док.	Подпись	Дата
Разраб.		Кормиец			12.05.26
Проверил		Галабурда			12.05.26
Н.контр.		Гордеев			12.05.26

МР-1535-01-АР

Развитие гостиницы «Приморская» в г. Сочи. Строительство нового корпуса гостиницы, расположенного по адресу: г. Сочи, Центральный район, ул. Соколова, д. 1. Этап 3

Архитектурные решения

Стадия	Лист	Листов
П	29	34

Фасад в осях Бп-Рп.

METROPOLIS

Формат А1