


Сечение по входу для артистов

(1:100)

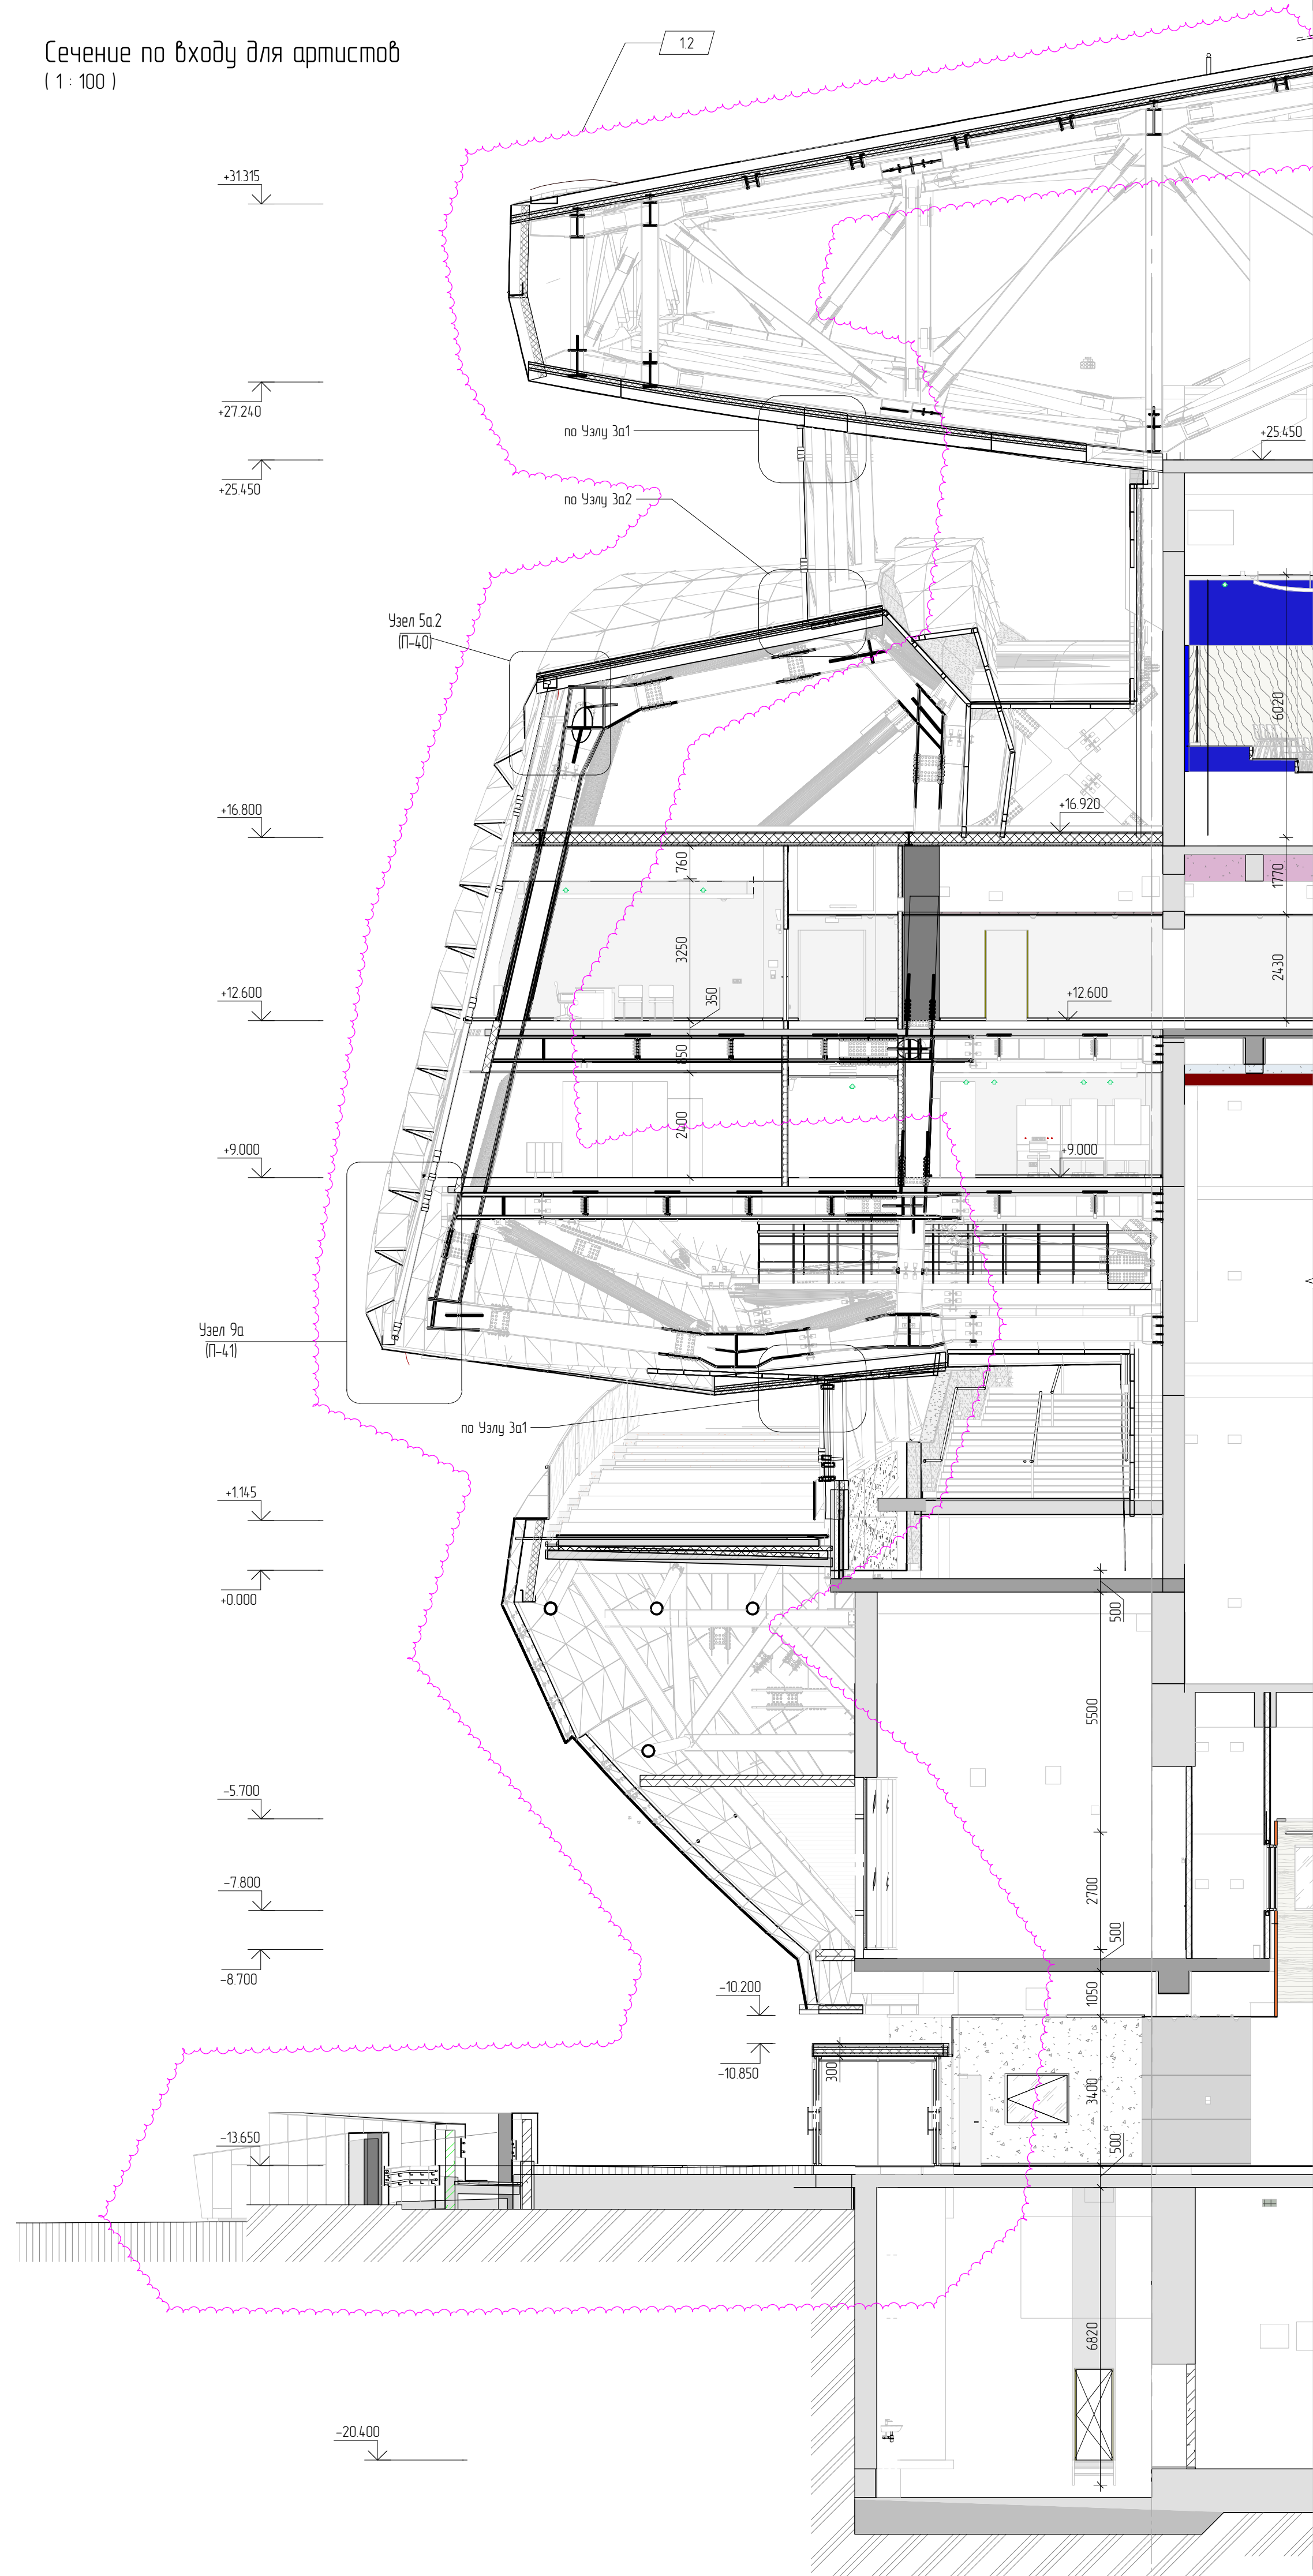

Разрез 4-4


(1:1 200)

Фибробетонные плиты Zolpette или аналог RAL 9016
Фасадная подсистема из нержавеющей стали MAC (или аналог)
Металлоконструкция из нержавеющей стали (карнизы, ригели)
Мембрана Гидропротектум НГ (исполн. АГ-А) или аналог
Утеплитель Вентил Баттс Д (ОПТ) или аналог
Пароизоляция Технониколь Паробарьер CAS500
Профилированные листы PE 35 оцинкованный окрасочный
Металлический каркас С255, 60x4 с покрытием двухкомпонентный
составом по типу Spharplast 205, либо стали AISI 304
Конструкция металлическая КМ

Группа отделочных работ
Экструдированный пенополистирол CARBON PROF
Геотекстильное полотно ТЕХНОНИКОЛЬ 500 г/м² или аналог
Гидроизоляционная мембрана LOGE BASE V-SL или аналог
Геотекстильное полотно ТЕХНОНИКОЛЬ 500 г/м² или аналог
Фундаментная стена

Фибробетонные плиты Zolpette или аналог RAL 9016
Фасадная подсистема из нержавеющей стали MAC (или аналог)
Металлоконструкция из нержавеющей стали
Система кровли: Тит-профиль SPM из алюминия с покрытием PE
Фальцевая кровля Ветролонг, окрас. покрытие 10 лет или аналог
Пространств. констр. из оцинк. стали для кров. системы
Утеплитель KNAUF INSULATION PROF TS 034 (или аналог) -50мм
Утеплитель KNAUF INSULATION PROF TS 034 (или аналог) -80мм
Утеплитель KNAUF INSULATION PROF TS 034 (или аналог) -50мм
Пароизоляционный слой Технониколь CAS500
Профилированный лист НТЛ, s=0.9мм (13.6 кг/м²)
Конструкция металлическая КМ

Фибробетонные плиты Zolpette или аналог RAL 9016
Фасадная подсистема из нержавеющей стали MAC (или аналог)
Металлоконструкция из нержавеющей стали
Система кровли: Тит-профиль SPM из алюминия с покрытием PE
Фальцевая кровля Ветролонг, окрас. покрытие 10 лет или аналог
Пространств. констр. из оцинк. стали для кров. системы
Утеплитель KNAUF INSULATION PROF TS 034 (или аналог) -50мм
Утеплитель KNAUF INSULATION PROF TS 034 (или аналог) -80мм
Утеплитель KNAUF INSULATION PROF TS 034 (или аналог) -50мм
Пароизоляционный слой Технониколь CAS500
Профилированный лист НТЛ, s=0.9мм (13.6 кг/м²)
Конструкция металлическая КМ

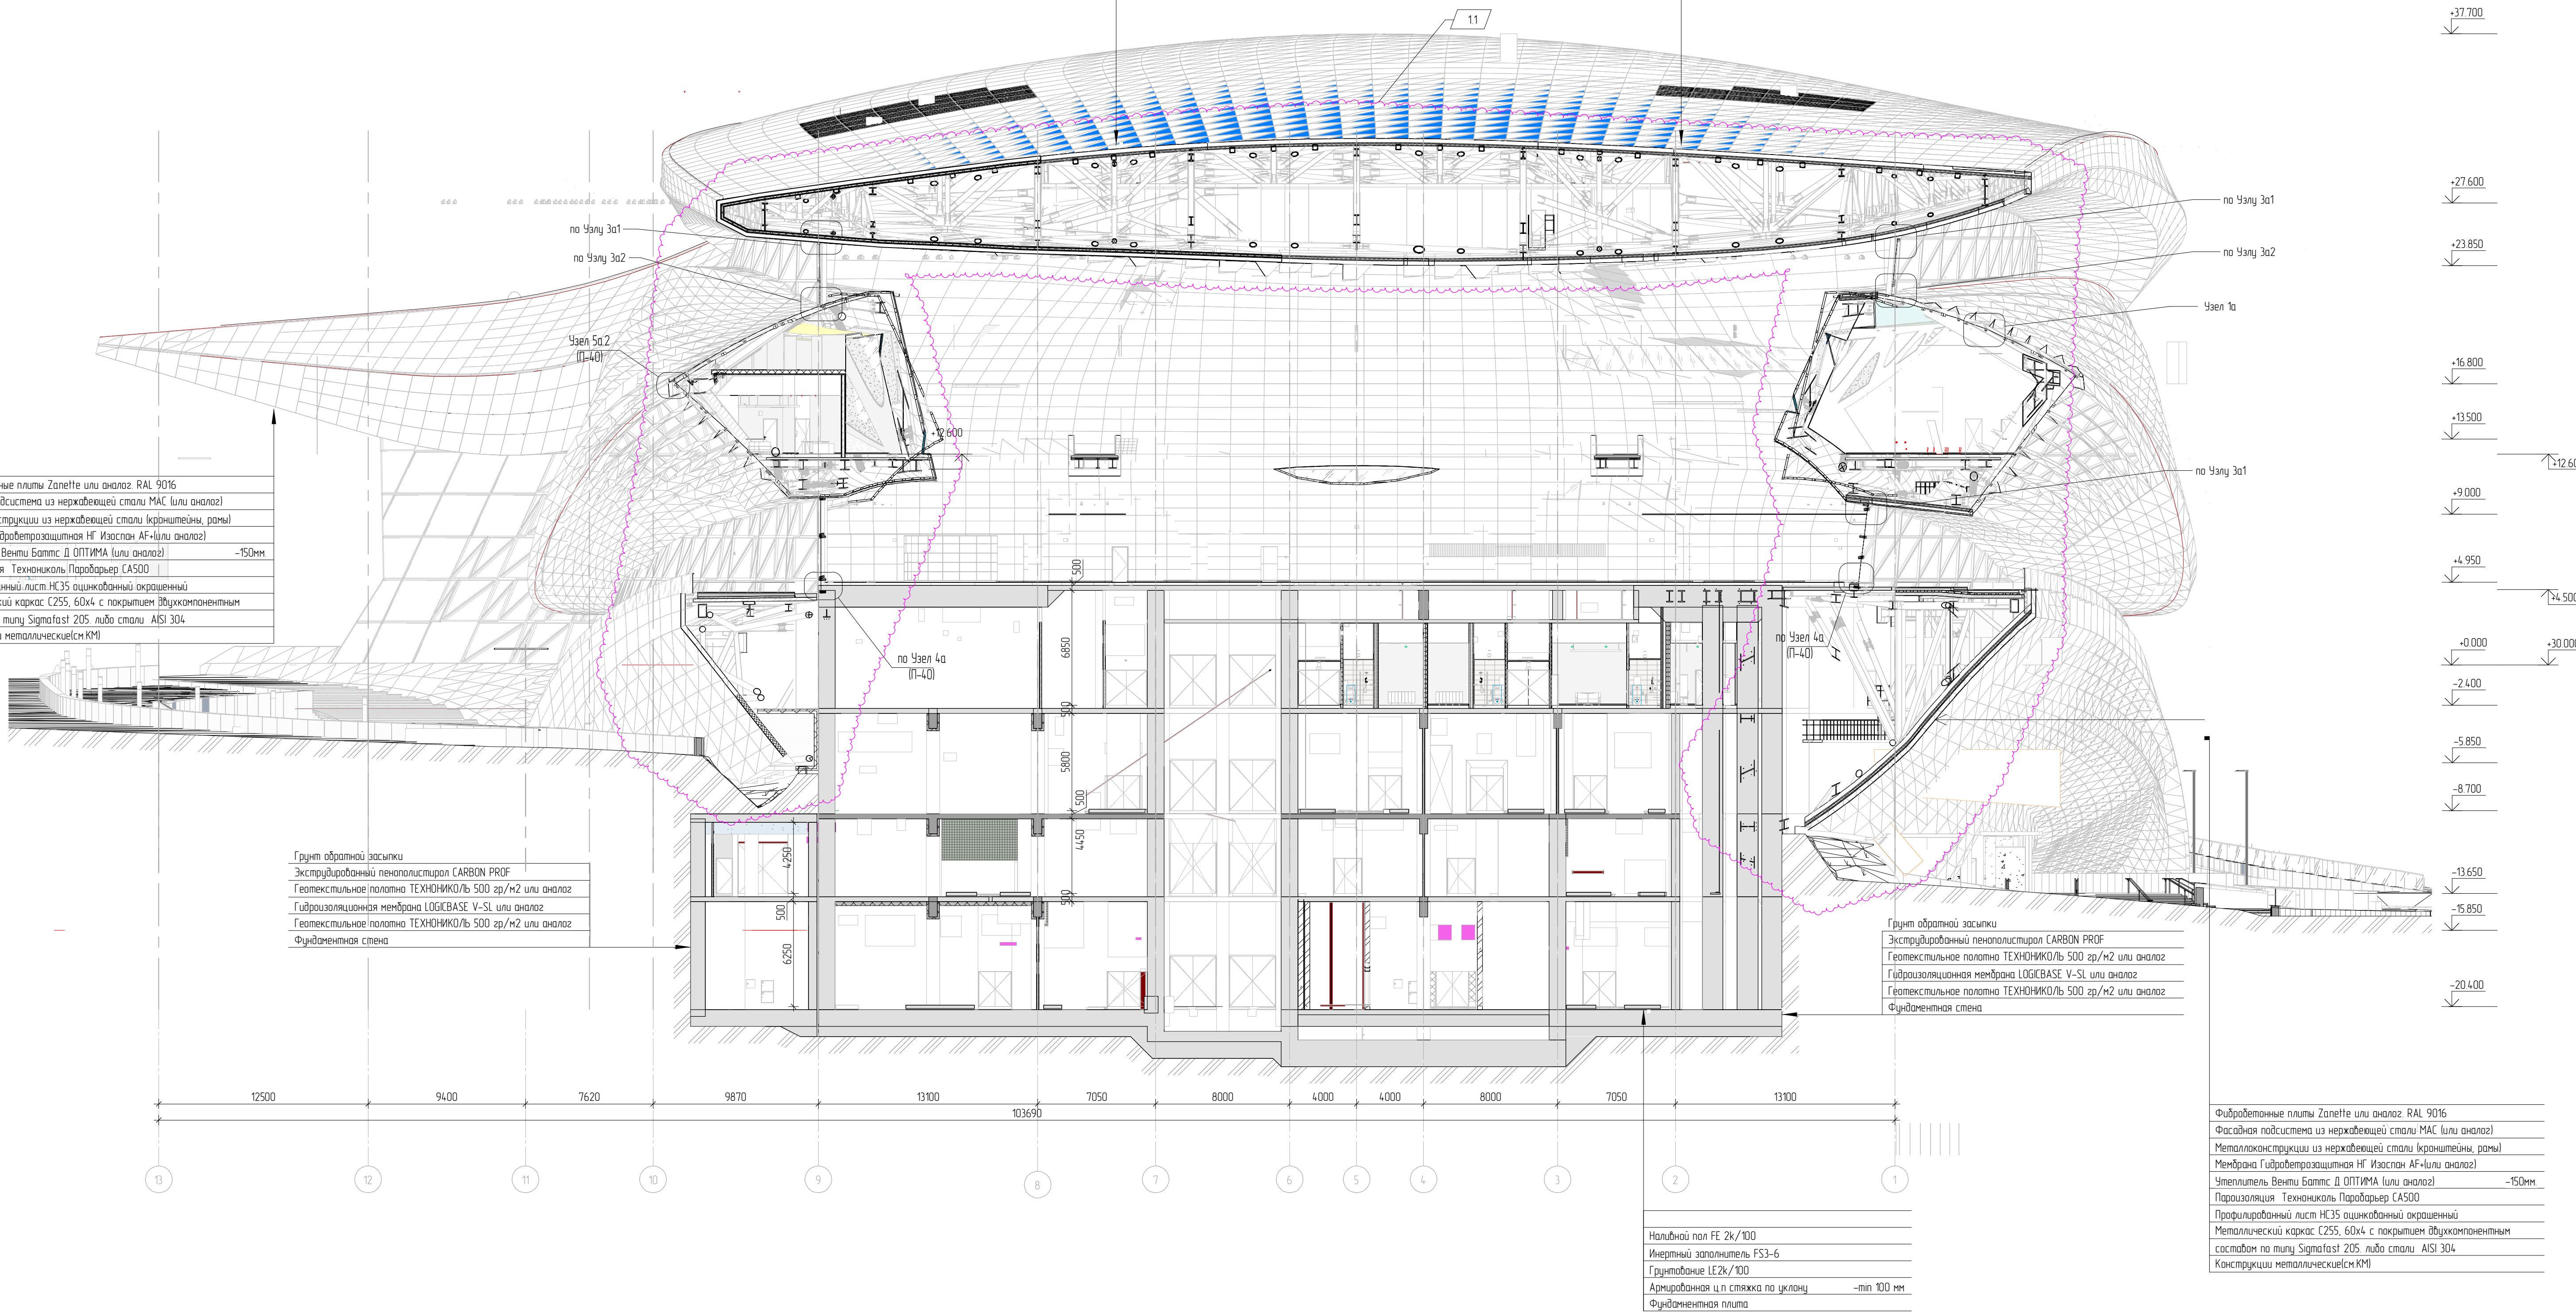


Группа отделочных работ
Экструдированный пенополистирол CARBON PROF
Геотекстильное полотно ТЕХНОНИКОЛЬ 500 г/м² или аналог
Гидроизоляционная мембрана LOGE BASE V-SL или аналог
Геотекстильное полотно ТЕХНОНИКОЛЬ 500 г/м² или аналог
Фундаментная стена

Наливной пол PE 26/100
Интерный заполнитель PS-3-6
Грунтобетон LE 26/100
Алюминиевая или стальная рама для остекления
Фундаментная плита

Фибробетонные плиты Zolpette или аналог RAL 9016
Фасадная подсистема из нержавеющей стали MAC (или аналог)
Металлоконструкция из нержавеющей стали (карнизы, ригели)
Мембрана Гидропротектум НГ (исполн. АГ-А) или аналог
Утеплитель Вентил Баттс Д (ОПТ) или аналог
Пароизоляция Технониколь Паробарьер CAS500
Профилированные листы НС35 оцинкованный окрасочный
Металлический каркас С255, 60x4 с покрытием двухкомпонентный
составом по типу Spharplast 205, либо стали AISI 304
Конструкция металлическая КМ

Сечение по рампе

(1:1 100)

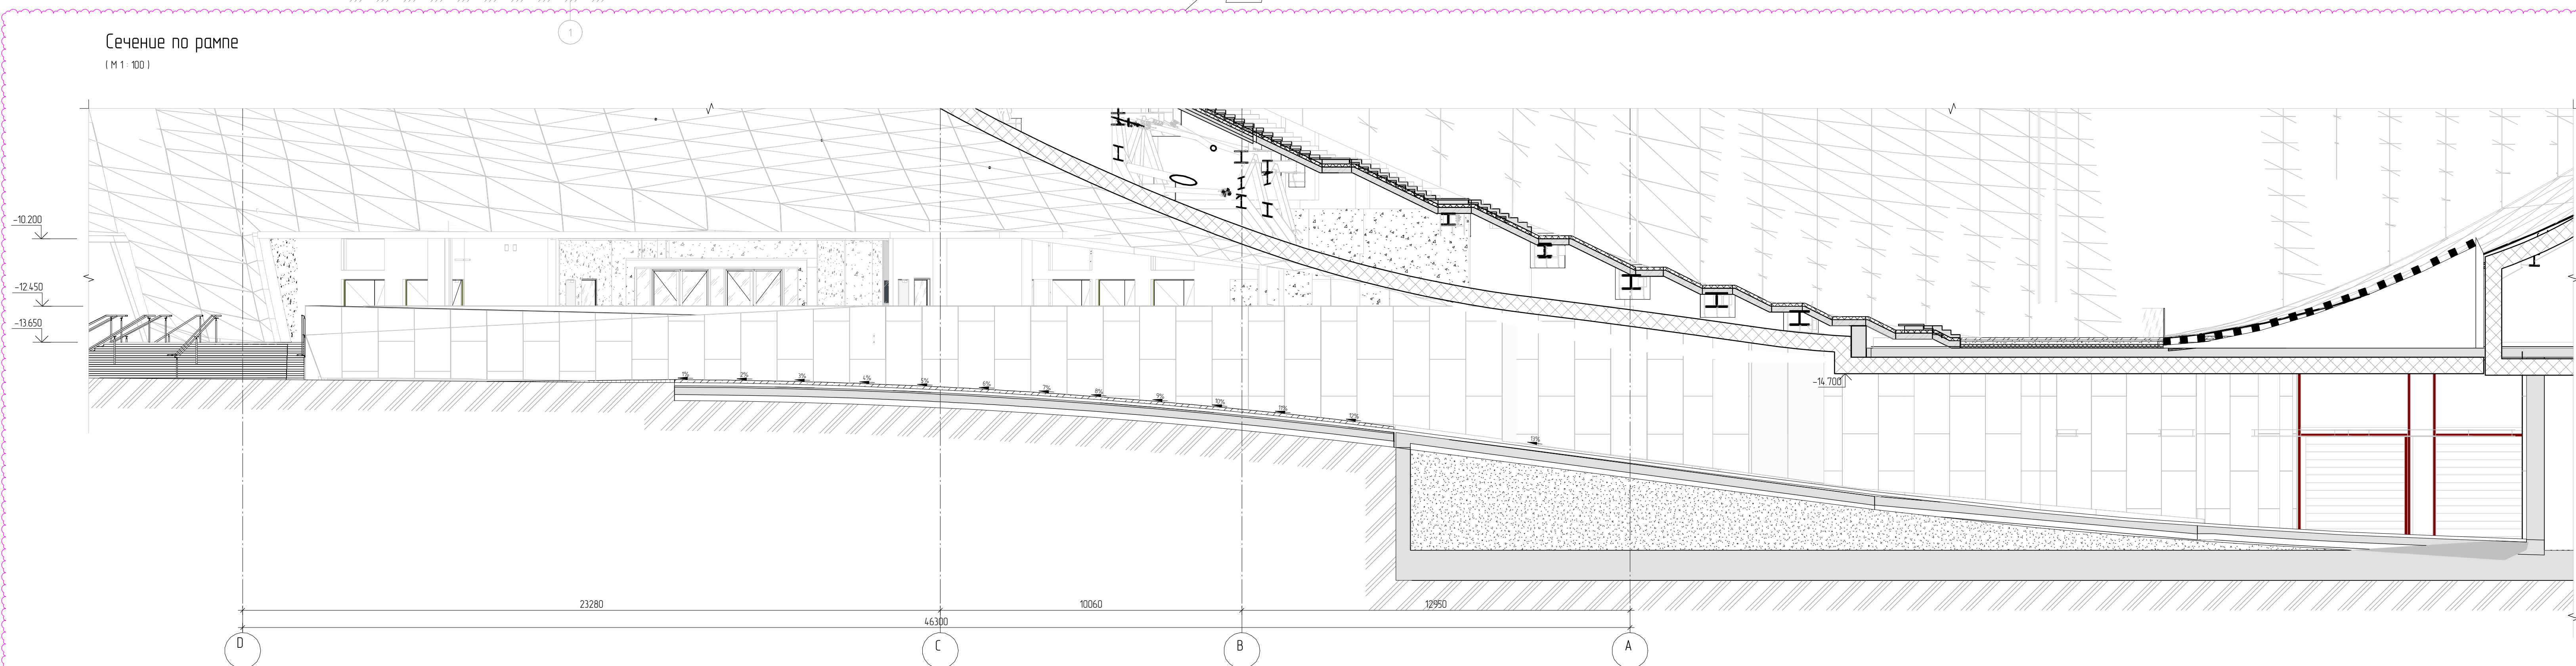

Примечания
- Чертежи см. совместно со всеми чертежами раздела
- За отсчетную высоту отметку +0.000 принята абсолютная отметка +30.000
- Проектные решения приняты на основании Спецификации Технических Заданий на проектирование проектной документации
- Стабильность оснований см. л. 35

0.000=30.00		MP-14/68П-00- AP1	
DESIGN ARCHITECT		по адресу: Российская Федерация, г. Севастополь	
COOP		РАЗРЕЗ 4-4, сечения по рампе и входу для артистов	
CONSULTANTS		МЕТРОПОЛИС	
ИТ	Зам	10.03.25	05.08.25
7	Зам	12.04.25	08.07.25
6	Зам	10.06.25	09.04.25
5	Зам	09.09.25	02.06.25
ИТ	Авт	10.03.25	05.08.25
7	Авт	12.04.25	08.07.25
6	Авт	10.06.25	09.04.25
5	Авт	09.09.25	02.06.25
ИТ	Проект	10.03.25	05.08.25
7	Проект	12.04.25	08.07.25
6	Проект	10.06.25	09.04.25
5	Проект	09.09.25	02.06.25
ИТ	Проект	10.03.25	05.08.25
7	Проект	12.04.25	08.07.25
6	Проект	10.06.25	09.04.25
5	Проект	09.09.25	02.06.25