



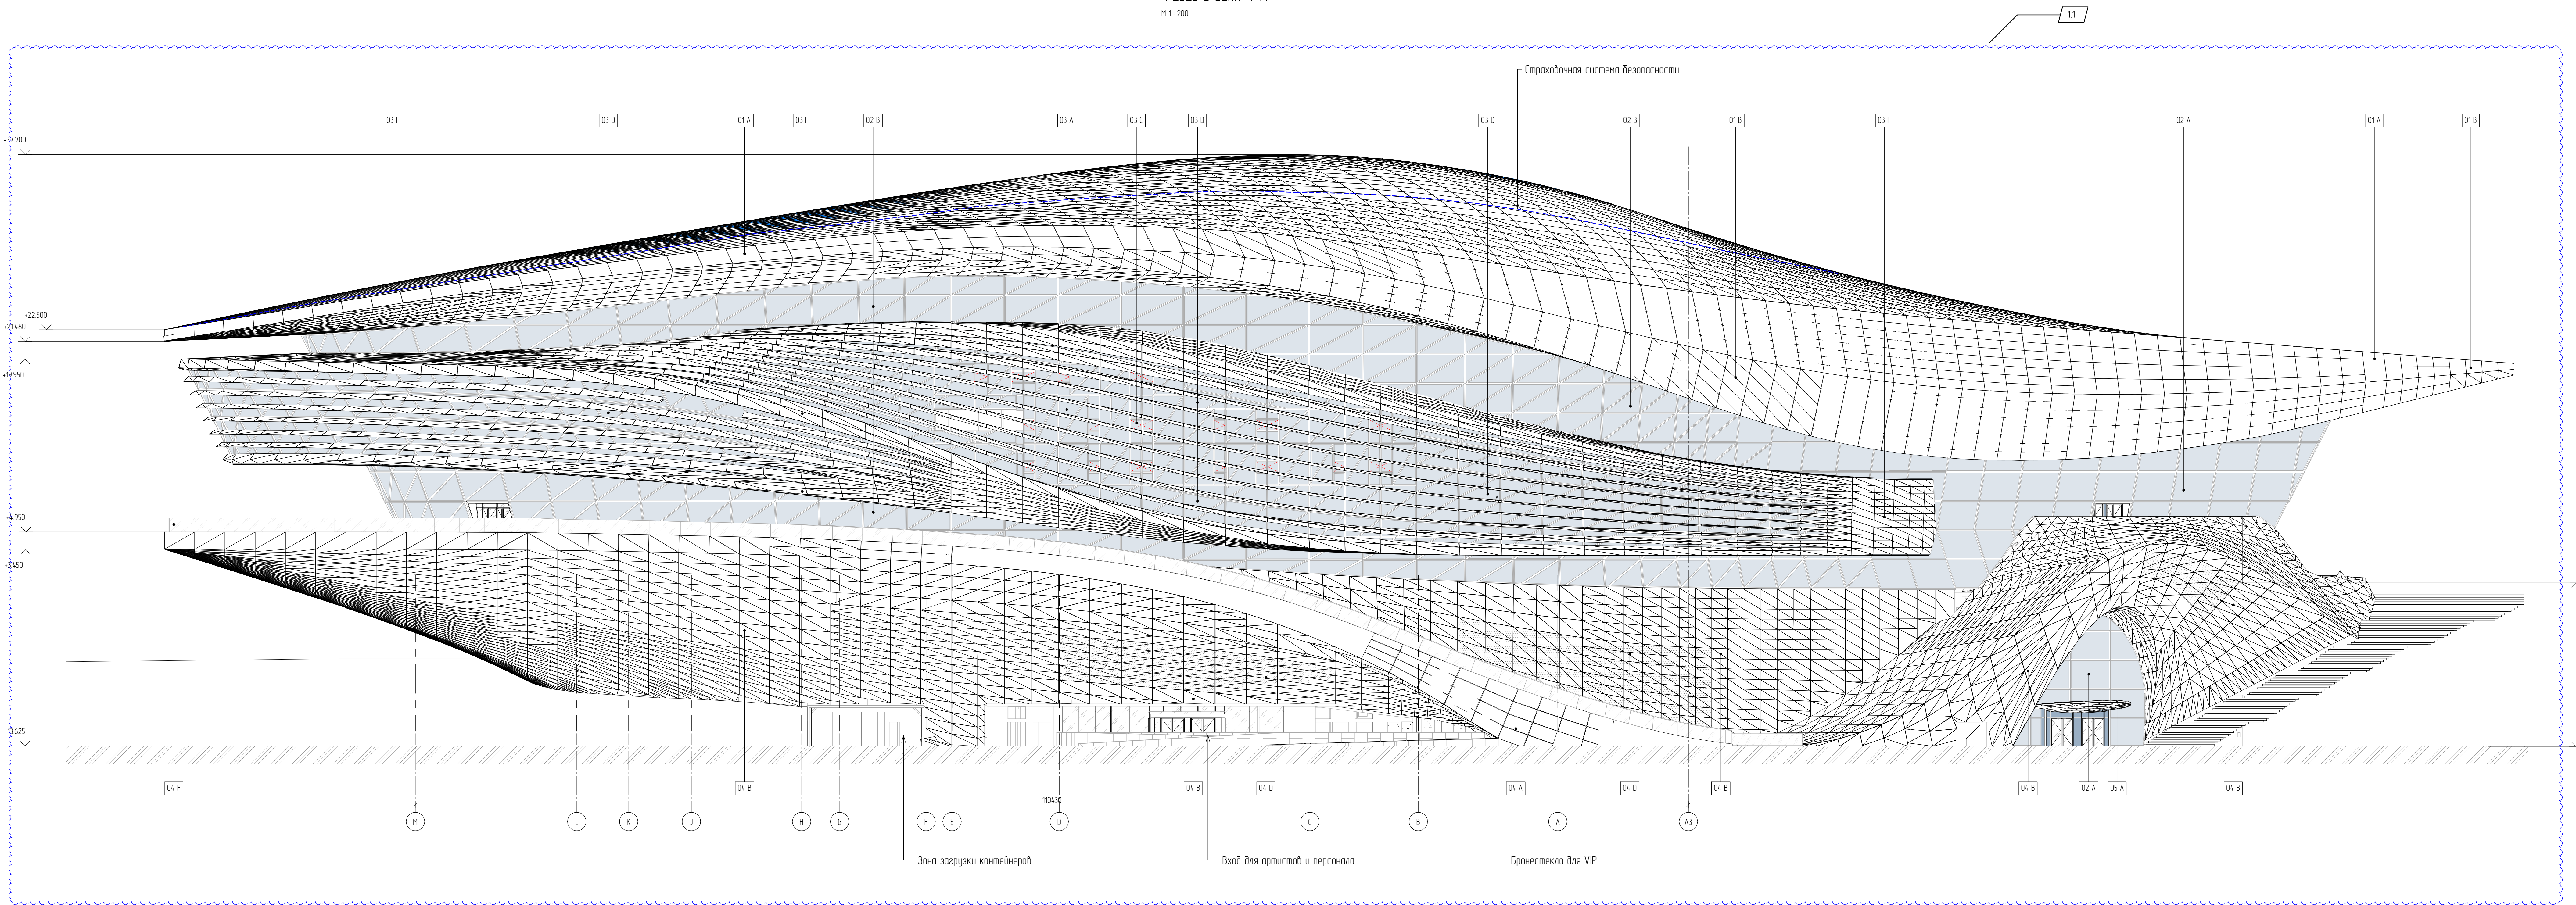

| Ведомость отделки фасадов |              |                              |                                                       |      |                    |                               |                                          |
|---------------------------|--------------|------------------------------|-------------------------------------------------------|------|--------------------|-------------------------------|------------------------------------------|
| Обозн.                    | Часть здания | Материал                     | Описание                                              | Цвет | RAL                | Артикул                       | Лист                                     |
| 01A                       | Кровля       | Zanette Панель               | Панель 4 ребра, белая, матовое покрытие               |      | 9016 Traffic White | Zanette GRC ZIP               | S 33 S 25.2 R19 R9A F2A F7A              |
| 01B                       | Кровля       | Zanette Панель               | Панель 3 ребра, белая, матовое покрытие               |      | 9016 Traffic White | Zanette GRC ZIP               | S 33 S 25.2 R19 R9A F2A F7A              |
| 01C                       | Кровля       | Фальш-фасад                  | Фальш-фасад                                           |      |                    | Имитация, материал            | S 33 S 25.2 R19 R9A F2A F7A              |
| 02A                       | Фойе         | Стеклопанель                 | Структурное остекление, панель 4 ребра                |      |                    | LataPro HD Light Blue 52      | S 34 S 35 S 25.3 S 25.4 CSA (I) CSA (II) |
| 02B                       | Фойе         | Стеклопанель                 | Структурное остекление, панель 3 ребра                |      |                    | LataPro HD Light Blue 52      | S 34 S 35 S 25.3 S 25.4                  |
| 02C                       | Фойе         | Стеклопанель                 | Структурное остекление, панель 2 ребра с отслаиванием |      |                    | LataPro HD Light Blue 52      | S 34 S 35 S 25.3 S 25.4                  |
| 02D                       | Фойе         | Стеклопанель                 | Структурное остекление, панель 1 ребра с отслаиванием |      |                    | LataPro HD Light Blue 52      | S 34 S 35 S 25.3 S 25.4                  |
| 03A                       | Скоба        | Стеклопанель                 | Панель 3 ребра                                        |      |                    | LataPro HD Light Blue 52      | S 35 S 39 CSA (I) CSA (II)               |
| 03B                       | Скоба        | Стеклопанель                 | Панель 2 ребра с отслаиванием                         |      |                    | LataPro HD Light Blue 52      | S 35 S 39                                |
| 03C                       | Скоба        | Стеклопанель                 | Остекление обшивки, с отслаиванием                    |      |                    | LataPro HD Light Blue 52      | S 35 S 39                                |
| 03D                       | Скоба        | Стеклопанель                 | Непрозрачная панель 3 ребра                           |      |                    | LataPro HD Light Blue 52      | S 35 S 39                                |
| 03E                       | Скоба        | Zanette панель               | Панель 4 ребра, белая, матовое покрытие               |      | 9016 Traffic White | Zanette GRC ZIP               | S 35 S 39 CSA                            |
| 03F                       | Скоба        | Zanette панель               | Панель 3 ребра, белая, матовое покрытие               |      | 9016 Traffic White | Zanette GRC ZIP               | S 35 S 39                                |
| 03G                       | Скоба        | Армированное стекло          | Армированное стекло с покрытием black-out             |      |                    | LataPro HD Light Blue 52 BP-3 | S 35 S 39                                |
| 04A                       | Цоколь       | Zanette панель               | Панель 4 ребра, белая, матовое покрытие               |      | 9016 Traffic White | Zanette GRC ZIP               | S 35 S 39 R9B F4A R9B F4A                |
| 04B                       | Цоколь       | Zanette панель               | Панель 3 ребра, белая, матовое покрытие               |      | 9016 Traffic White | Zanette GRC ZIP               | S 35 S 39 R9B F4A                        |
| 04C                       | Цоколь       | Zanette панель               | Панель 2 ребра, белая, матовое покрытие               |      | 9016 Traffic White | Zanette GRC ZIP               | S 35 S 39                                |
| 04D                       | Цоколь       | Стеклопанель                 | Панель 1 ребра, белая, матовое покрытие               |      | 9016 Traffic White | LataPro HD Light Blue 52 R6T8 | S 40 R9B                                 |
| 04E                       | Цоколь       | Модуль из натурального камня | Пешеходная зона                                       |      |                    | LataPro HD Light Blue 52      | S 40                                     |
| 04F                       | Цоколь       | Стекло                       | Ограждение                                            |      |                    | Zanette GRC ZIP               | S 40                                     |
| 05A                       | Вход         | Zanette панель               | Коридор, белый, матовое покрытие                      |      | 9016 Traffic White | Zanette GRC ZIP               | S 34 S 35 E4B E3B                        |
| 05B                       | Вход         | Стеклопанель                 | Остекление входного портала                           |      |                    | LataPro HD Light Blue 52      | S 34 S 35                                |
| 05C                       | Вход         | Стеклопанель                 | Остекление, панель 4 ребра с отслаиванием             |      |                    | LataPro HD Light Blue 52      | S 34 S 35                                |
| 05D                       | Вход         | Металл                       | Обивочная алюминиевая панель                          |      | 9016 Traffic White | Color to Match Fibre C        | S 34 S 35                                |
| 06A                       | Холодильник  | Zanette панель               | Панель 4 ребра, белая, матовое покрытие               |      | 9016 Traffic White | Zanette GRC ZIP               | S 40                                     |
| 06B                       | Холодильник  | Zanette панель               | Панель 3 ребра, белая, матовое покрытие               |      | 9016 Traffic White | Zanette GRC ZIP               | S 40                                     |

Объем материалов см. ведомость на листе 29 б

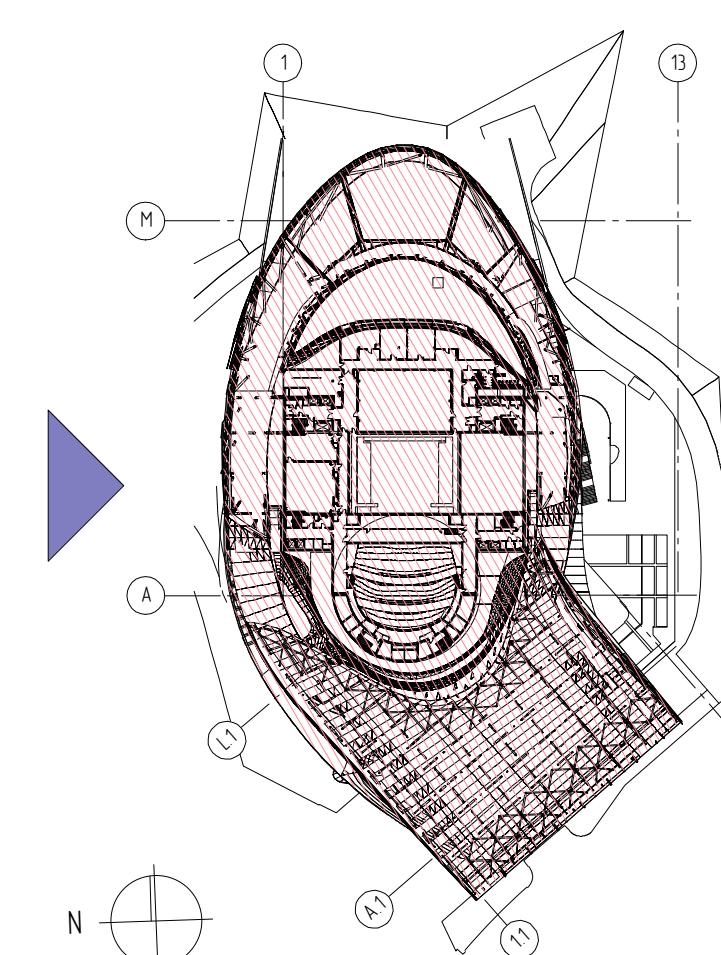

0.000-30.000

0.000-30.00

DESIGN ARCHITECT

COOP

CONSULTANTS

MP-1468П-00- AP1

по адресу: Российская Федерация, г. Спбасмол.

Подраздел 1 Архитектурные решения

Фасад в осях N-A

Масштаб

Лист

27

Масштаб

Масштаб

Масштаб

Масштаб

Масштаб