



Фасад в осях А-Н
М 1: 200

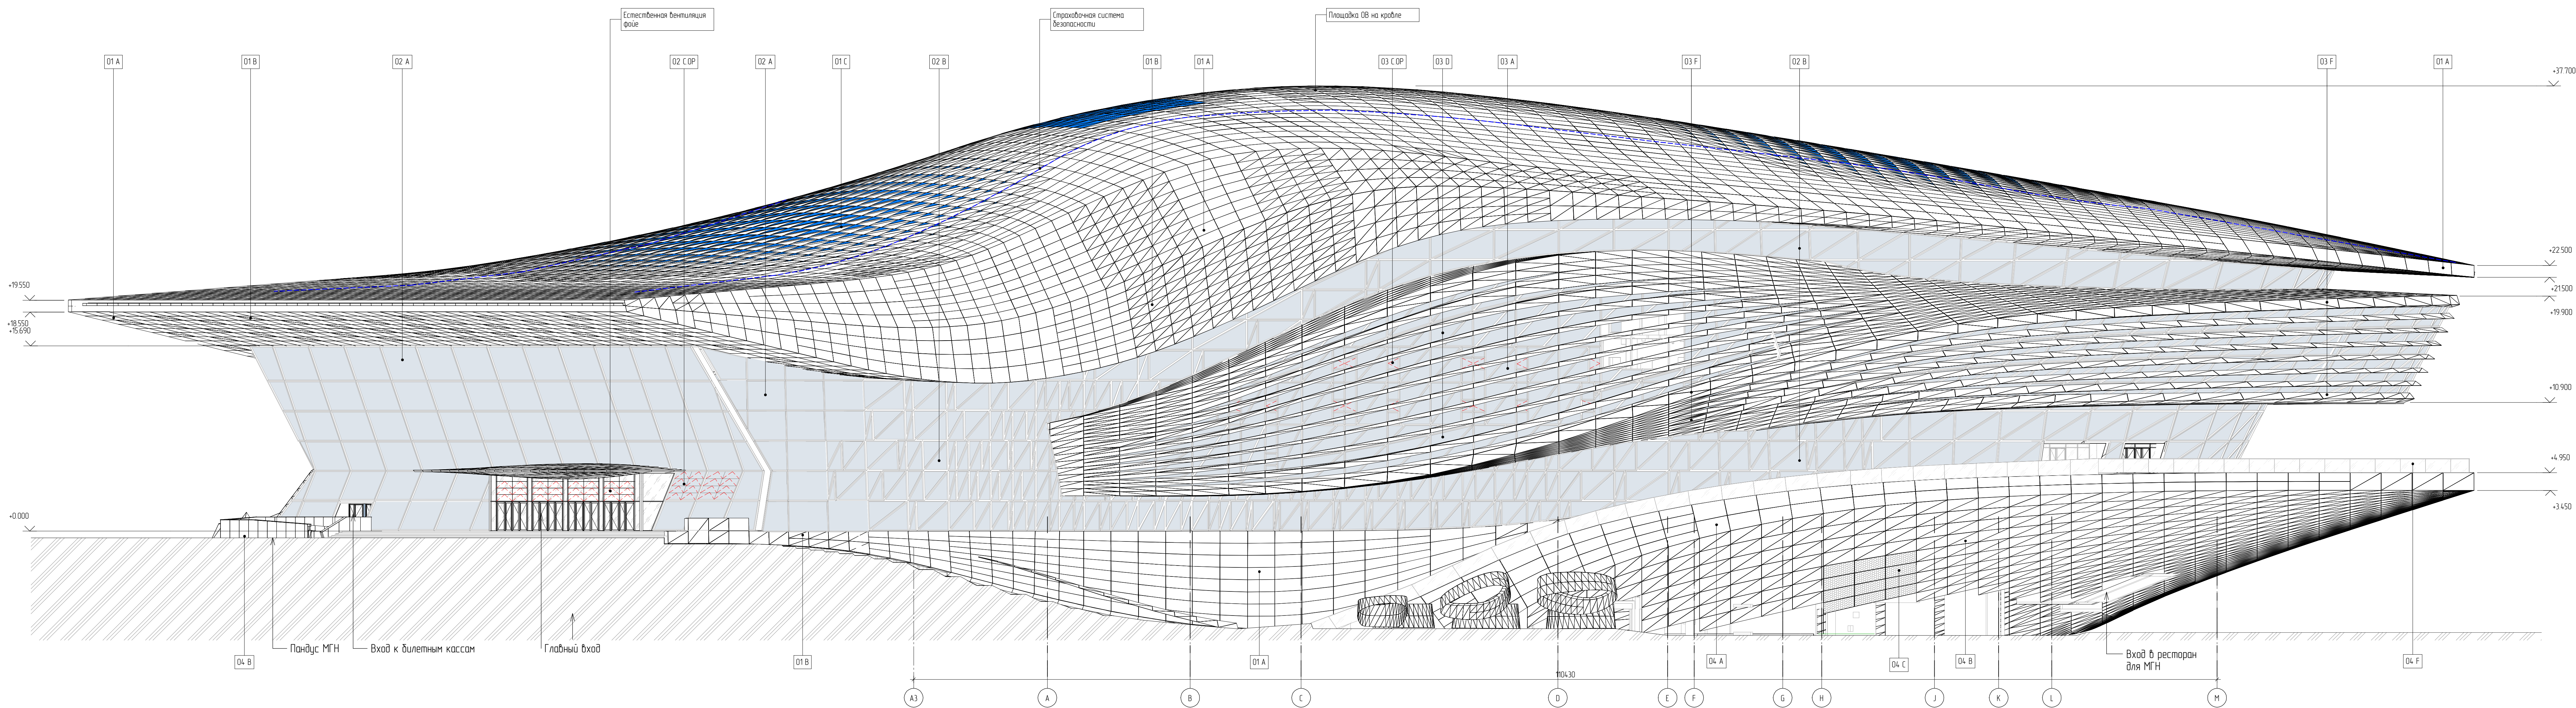

Ведомость отделки фасадов							
Обозн.	Часть здания	Материал	Описание	Цвет	RAL	Артикул	Лист
01.А	Кровля	Zanette Панель	Панель 4 ребра, белая, матовое покрытие		9016 Traffic White	Zanette GRC ZIP	S 33
01.В	Кровля	Zanette Панель	Панель 3 ребра, белая, матовое покрытие		9016 Traffic White	Zanette GRC ZIP	S 25.2
01.С	Кровля	Фальш-фонарь	Фальш-фонарь			Индикатор, изготовлен	S 33
02.А	Фойе	Стеклопакет	Структурное остекление, панель 4 ребра			LataPro HD Light Blue 52	S 34 S 35
02.В	Фойе	Стеклопакет	Структурное остекление, панель 3 ребра			LataPro HD Light Blue 52	S 25.3 S 25.4
02.С	Фойе	Стеклопакет	Структурное остекление, панель 4 ребра с опоясывающим			LataPro HD Light Blue 52	S 34 S 35
02.Д	Фойе	Стеклопакет	Структурное остекление, панель 3 ребра с опоясывающим			LataPro HD Light Blue 52	S 25.3 S 25.4
03.А	Сюба	Стеклопакет	Панель 3 ребра			LataPro HD Light Blue 52	S 35 S 39
03.В	Сюба	Стеклопакет	Панель 3 ребра с опоясывающим			LataPro HD Light Blue 52	S 35 S 39
03.С	Сюба	Стеклопакет	Остекление балконов, с опоясывающим			LataPro HD Light Blue 52	S 35 S 39
03.Д	Сюба	Стеклопакет	Необработанная панель 3 ребра			LataPro HD Light Blue 52	S 35 S 39
03.Е	Сюба	Zanette панель	Панель 4 ребра, белая, матовое покрытие		9016 Traffic White	Zanette GRC ZIP	S 35 S 39
03.В	Сюба	Zanette панель	Панель 3 ребра, белая, матовое покрытие		9016 Traffic White	Zanette GRC ZIP	S 35 S 39
03.С	Сюба	Армированное стекло	Армированное стекло с покрытием black-out			LataPro HD Light Blue 52	S 35 S 39
04.А	Цоколь	Zanette панель	Панель 4 ребра, белая, матовое покрытие		9016 Traffic White	Zanette GRC ZIP	S 40
04.В	Цоколь	Zanette панель	Панель 3 ребра, белая, матовое покрытие		9016 Traffic White	Zanette GRC ZIP	S 40
04.С	Цоколь	Цокольный металл	Цокольный металл			LataPro HD Light Blue 52	S 40
04.Д	Цоколь	Цокольный металл	Цокольный металл			LataPro HD Light Blue 52	S 40
04.Е	Цоколь	Цокольный металл	Цокольный металл			LataPro HD Light Blue 52	S 40
05.А	Вход	Zanette панель	Корырек, белая, матовое покрытие		9016 Traffic White	Zanette GRC ZIP	S 34
05.В	Вход	Стеклопакет	Остекление входного портала			LataPro HD Light Blue 52	S 34
05.С	Вход	Стеклопакет	Остекление, панель 4 ребра с опоясывающим			LataPro HD Light Blue 52	S 34
06.А	Вход	Металл	Облицовочная алюминиевая панель		9016 Traffic White	Color to Match Fibre C	S 34
06.В	Хлацинтер	Zanette панель	Панель 4 ребра, белая, матовое покрытие		9016 Traffic White	Zanette GRC ZIP	S 40
06.С	Хлацинтер	Zanette панель	Панель 3 ребра, белая, матовое покрытие		9016 Traffic White	Zanette GRC ZIP	S 40

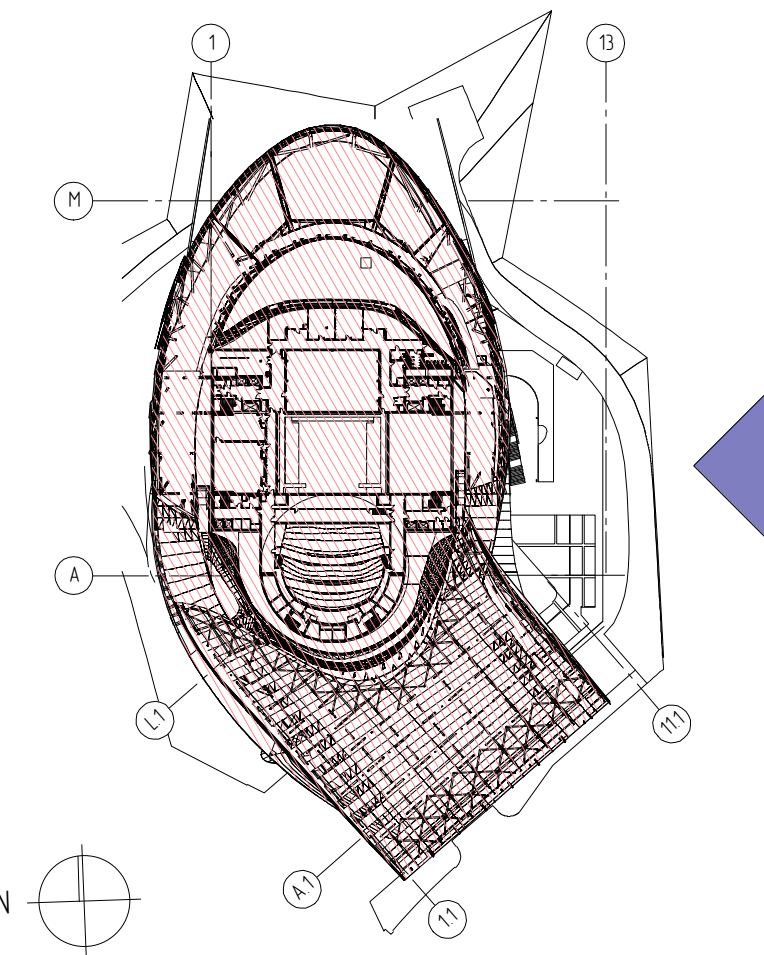

0.000=30.000

0.000=30.000

DESIGN ARCHITECT
COOP II MM ELBIAU
Hof & Pichler Partner G.m.b.H.

TEL: +43 (0) 516 66-0
FAX: +43 (0) 516 66-600

SPRINGERGASSE
37 A - 1050 WIEN

CONSULTANTS

MP-1468П-00- AP1

«Творчество и Дизайн»
по адресу: Российская Федерация, г. Санкт-Петербург

Разработчик: АСУП
Проектировщик: АСУП
Исполнитель: АСУП
Дата: 06.06.2015

Лист: 29

Фасад в осях А-Н

МЕТРОПОЛИС