


Фасады 10, 11 (1'-15, Л-Н) существующий (1 : 100)

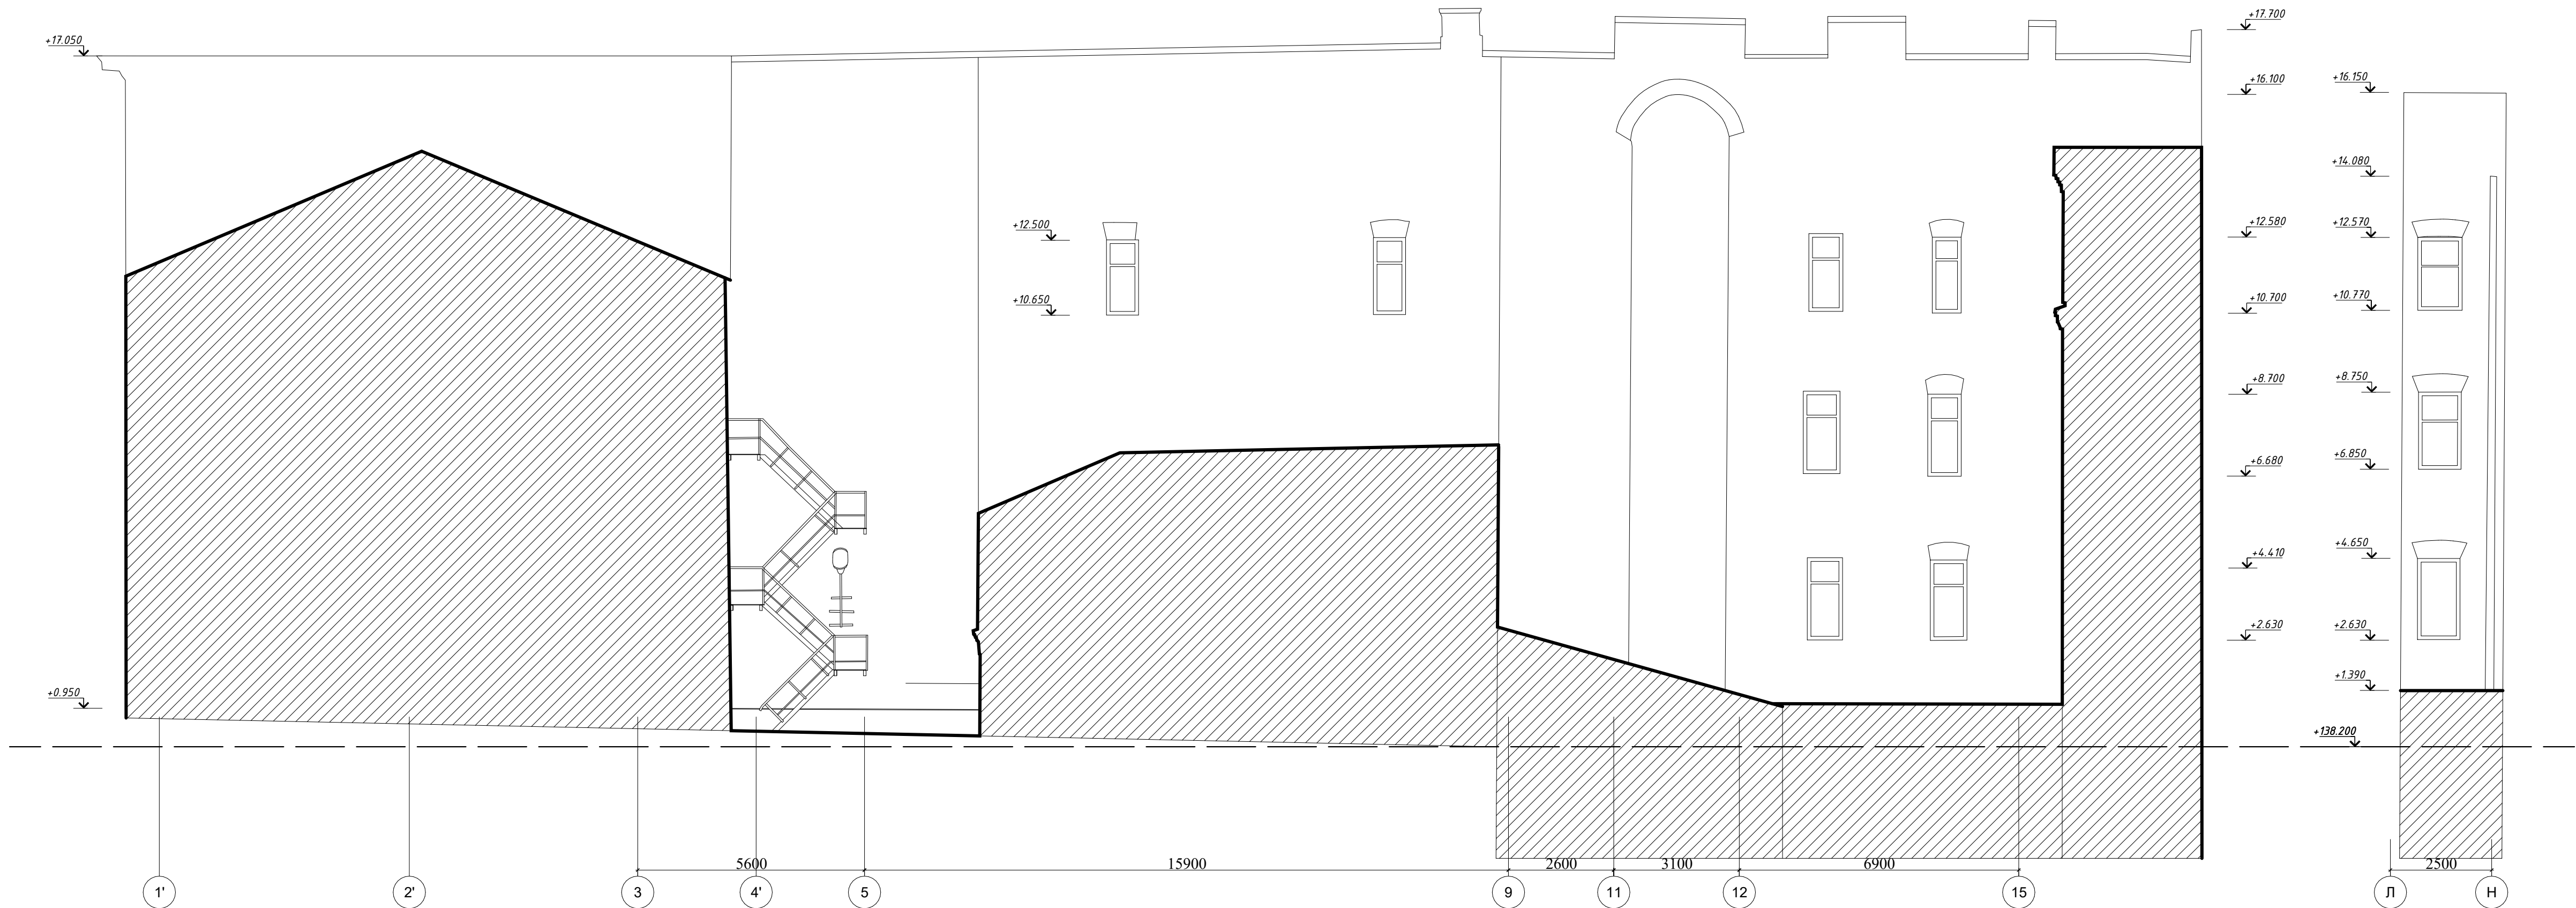

УСЛОВНЫЕ
ОБОЗНАЧЕНИЯ

- утраты отделки
- сырость

Согласовано					
Согласовано					
Инд. № подл.	Взам. инд. №	Подп. и дата			

						006/01/0048-20 - АР			
						Капитальный ремонт здания ФГБУ РГБ по адресу: г. Москва, ул Воздвиженка 1			
Изм.	Кол.уч.	Лист	№ док.	Подп.	Дата	Корпус К.	Стадия	Лист	Листов
ГИП		Григорьев К.В.					РД	42	110
ГАП		Щетинин А.В.				Фасады 10,11 (1'-15, Л-Н) существующие.	 ИНСТИТУТ проектирования и строительства		
Разработал		Щетинин А.В.							
Н. контр.		Рожков А.Ф.							Формат А1А