


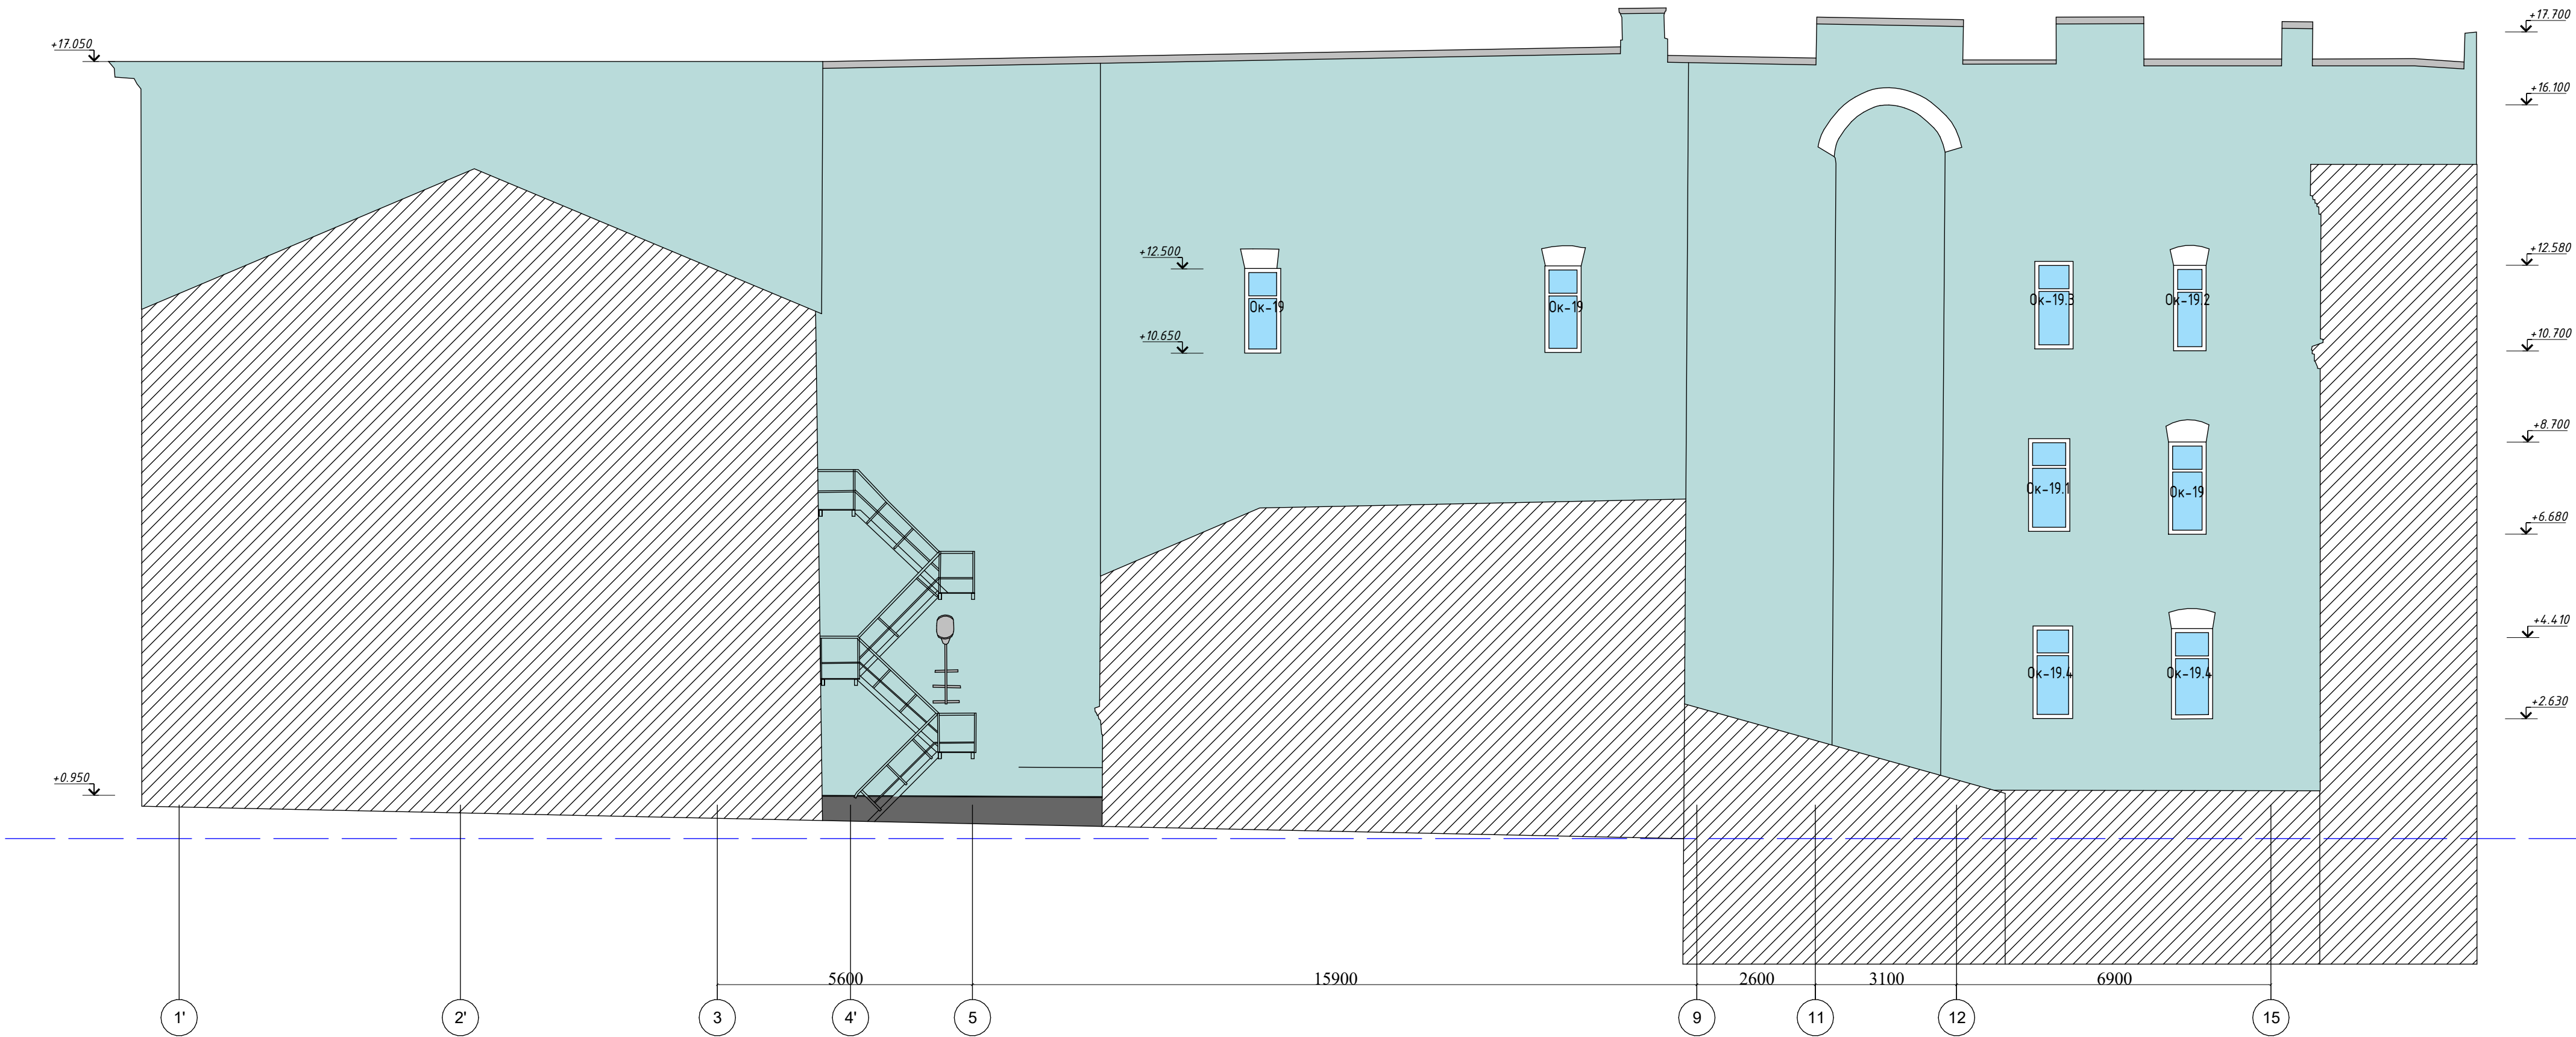

- УСЛОВНЫЕ
ОБОЗНАЧЕНИЯ**
- серый гранит
 - лепнина (RAL 9010)
 - основной цвет фасада (RAL 6027)
 - цвет кровли (оцинкованный металл)

Ведомость отделки Фасадов 10,11				
Наименование фасада	Площадь стен	Площадь отделки и покраски силиконовой краской RAL9010	Площадь отделки и покраски силиконовой краской RAL6027	Площадь полного восстановления утраченной отделки
Фасад 10,11 (1'-24)	1195,21	107,09	1116,70	478,08
Общий итог	1195,21	107,09	1116,70	478,08

						006/01/0048-20 - АР			
						Капитальный ремонт здания ФГБУ РГБ по адресу: г. Москва, ул Воздвиженка 1			
Изм.	Кол.ч.	Лист	№ док.	Подп.	Дата	Корпус К.	Стадия	Лист	Листов
ГИП			Григорьев К.В.				РД	43	110
ГАП			Щетинин А.В.			Фасады 10,11 (1'-15, Л-Н) после ремонта.	 ИНСТИТУТ проектирования и строительства		
Разработал			Щетинин А.В.						
Н. контр.			Рожков А.Ф.						